

Kitchen

1

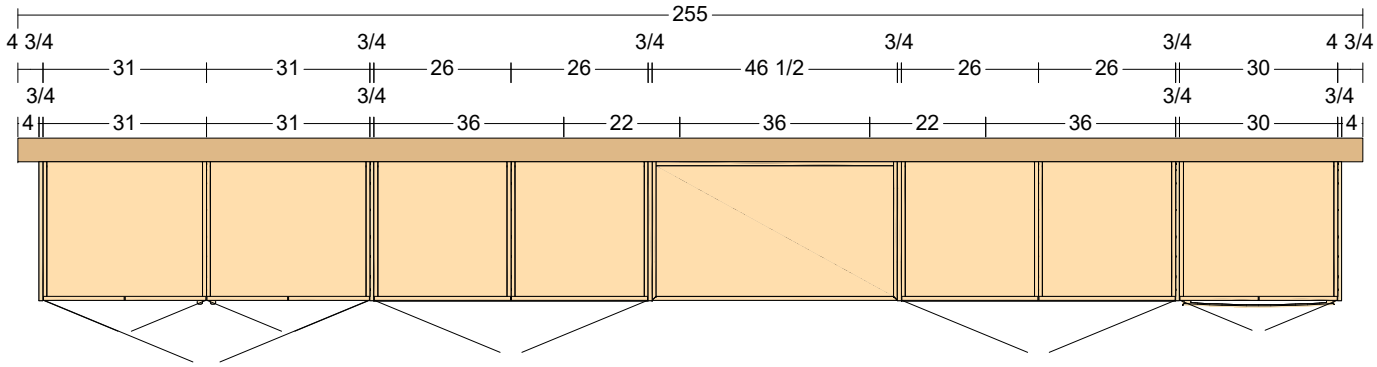


2

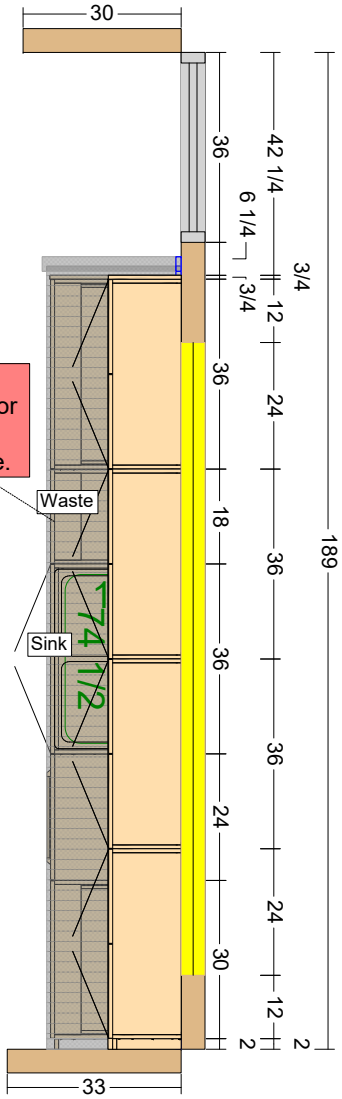

Builder Note:
Outlet needed inside for Waste roll out push to open electric hardware.

3

Builder Note:
Outlet needed inside for Waste roll out push to open electric hardware.

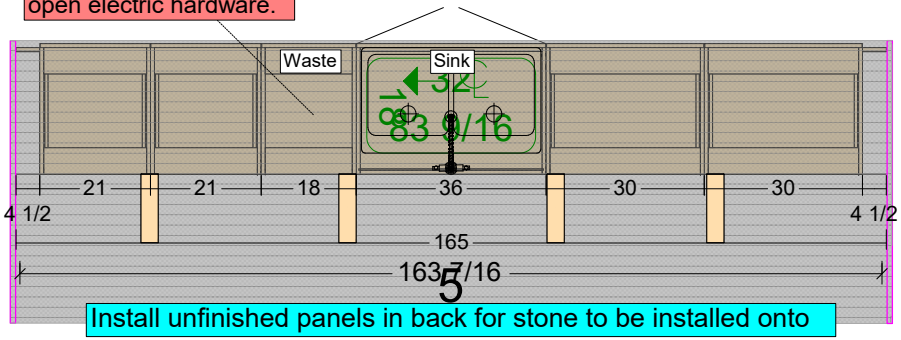

5

Install unfinished panels in back for stone to be installed onto

Stone will be on the back of the island

4

Peppermint Cabinets & More	Job: RAC-Oak Valley Estates 5	Address:	Scale: 1/2" = 1'	Page: 1/11
	Drawing Title: *Kitchen Top View*	Phone:	Date: 08/27/2026	
		E-Mail:	Revision: 1.0	











Peppermint Cabinets & More

Job: RAC-Oak Valley Estates 5	Address:	Scale: 1/2" = 1'	Page: 2/11
Drawing Title: *Kltchen*	Phone:	Date: 08/27/2026	
	E-Mail:	Revision: 1.0	


Wall #1

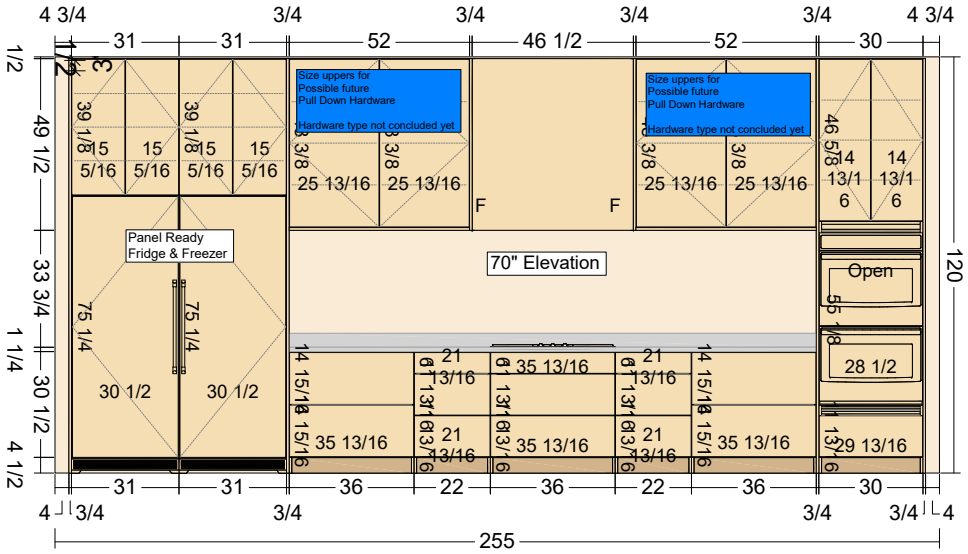


Wall #3

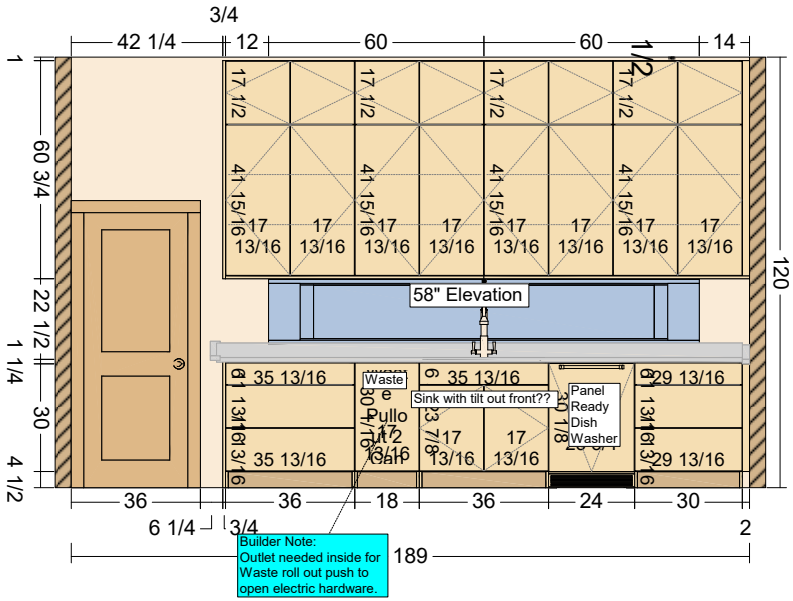

Wall #5

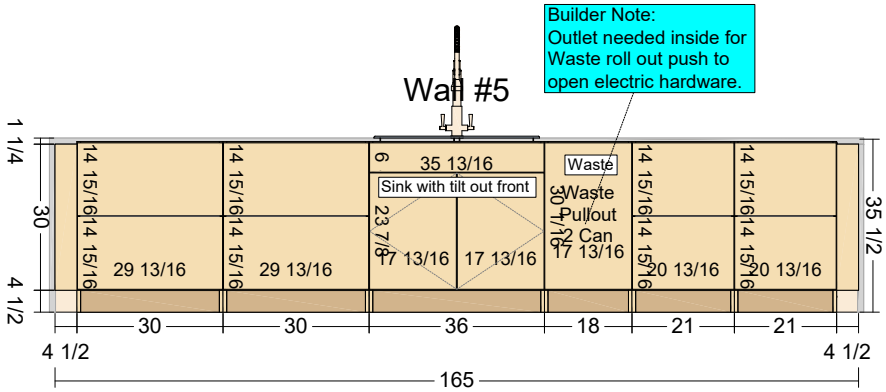


Wall #5 Back

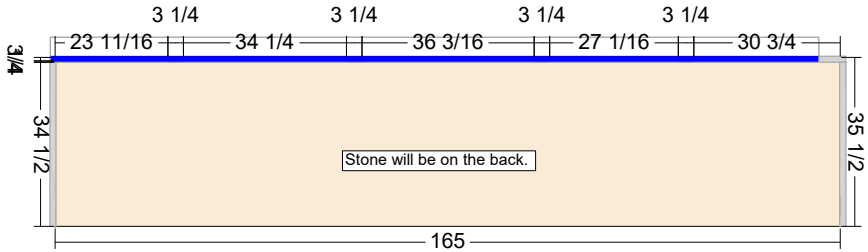


Peppermint Cabinets & More	Job: RAC-Oak Valley Estates 5	Address:	Scale: 1/2" = 1'	Page: 3/11
	Drawing Title: *Kitchen Elevations*	Phone:	Date: 08/27/2026	
		E-Mail:	Revision: 1.0	

Pantry

1

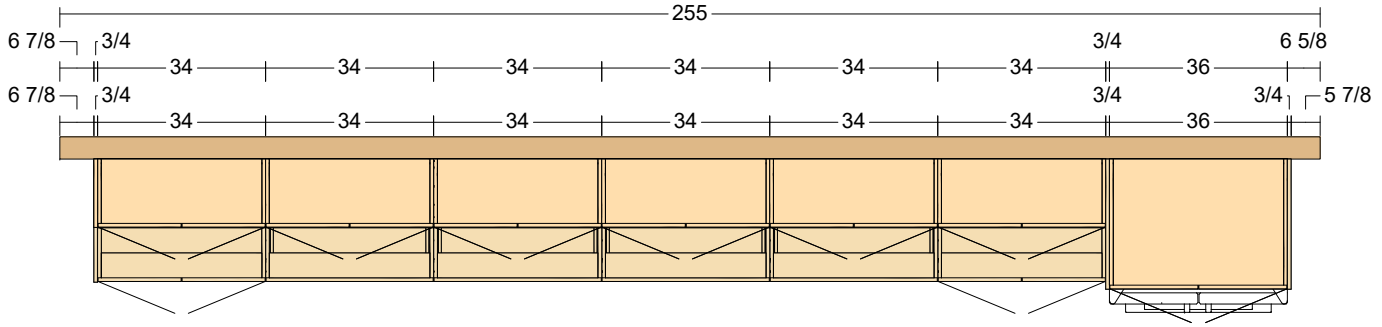

Wall #1

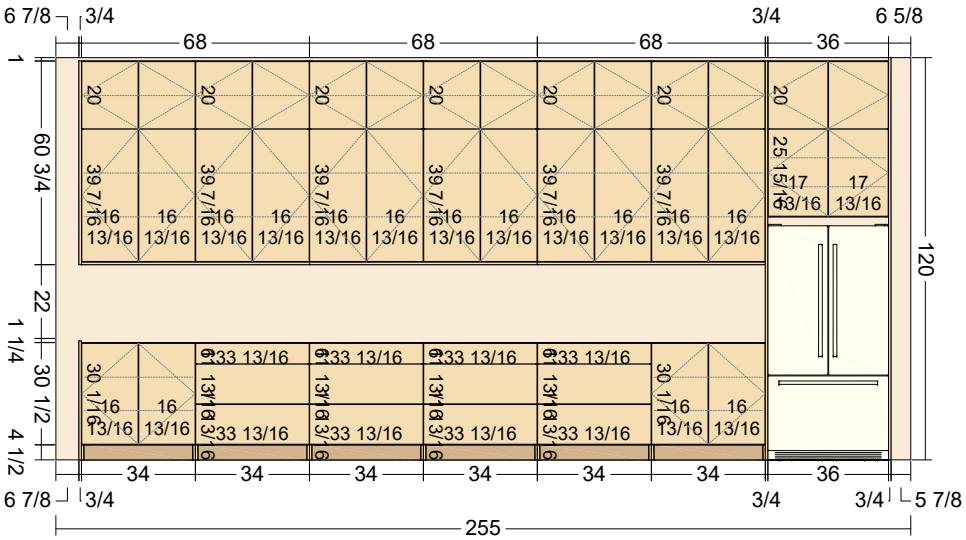




Peppermint Cabinets & More	Job: RAC-Oak Valley Estates 5	Address:	Scale: 1/2" = 1'	Page: 4/11
	Drawing Title: *Pantry*	Phone:	Date: 08/27/2026	
		E-Mail:	Revision: 1.0	


Powder Bath

2

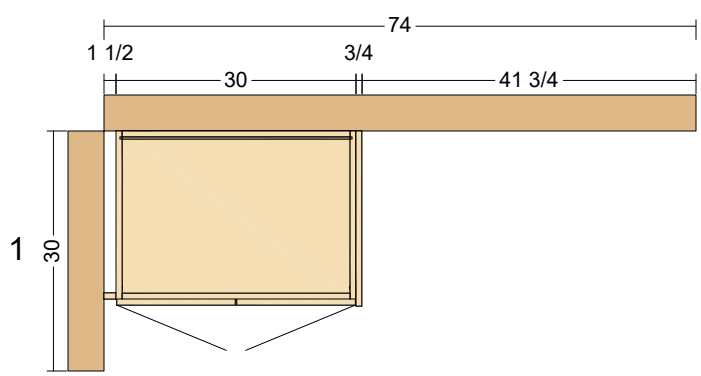




Wall #2

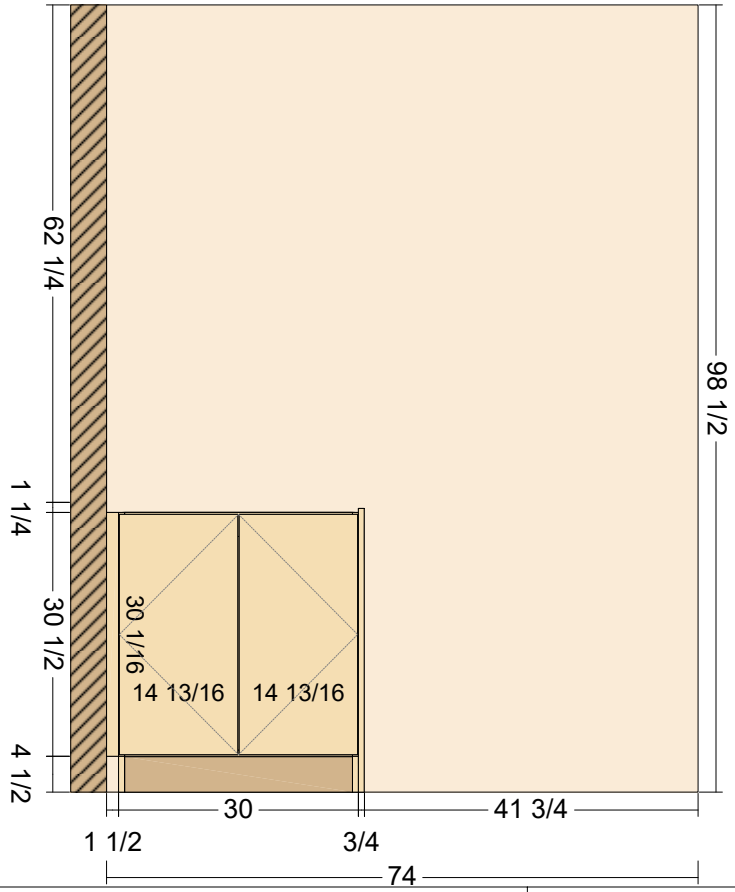


Peppermint Cabinets & More

Job: RAC-Oak Valley Estates 5	Address:	Scale: 1/2" = 1'	Page: 5/11
Drawing Title: ***Powder Bath***	Phone:	Date: 08/27/2026	
	E-Mail:	Revision: 1.0	

Office Bath

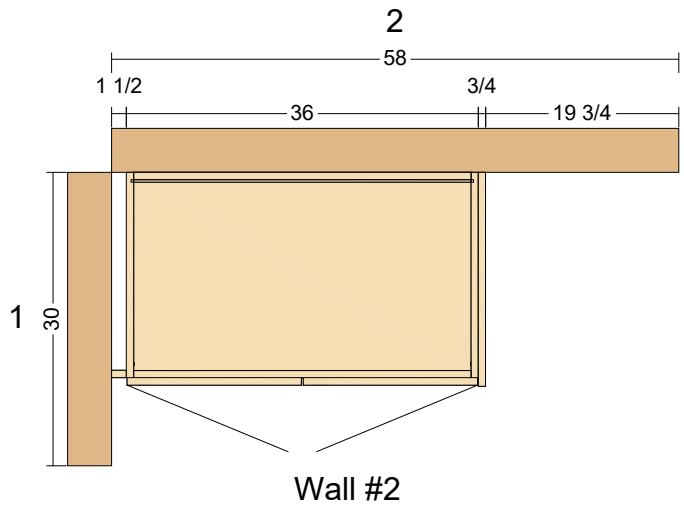



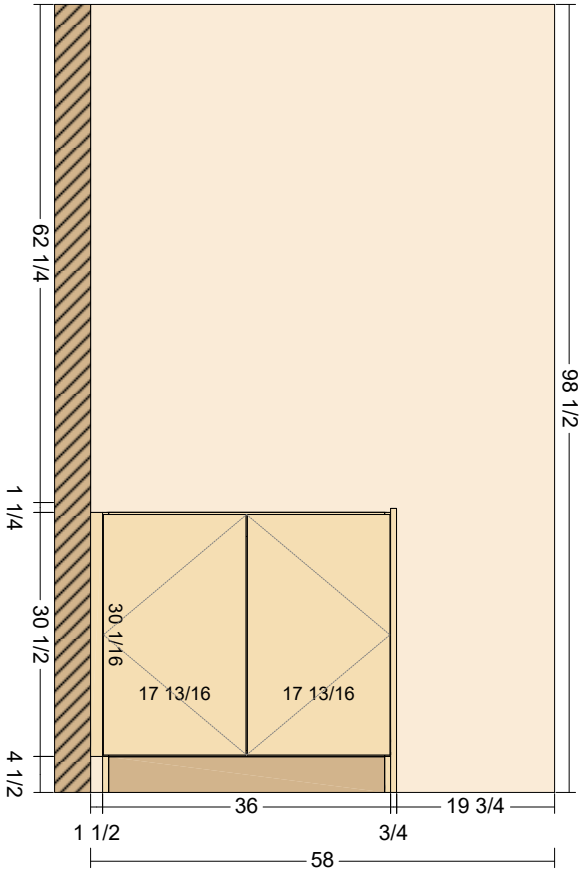


Peppermint Cabinets & More

Job: RAC-Oak Valley Estates 5	Address:	Scale: 1/2" = 1'	Page: 6/11
Drawing Title: *Office Bath*	Phone:	Date: 08/27/2026	
	E-Mail:	Revision: 1.0	


Master Bath

1

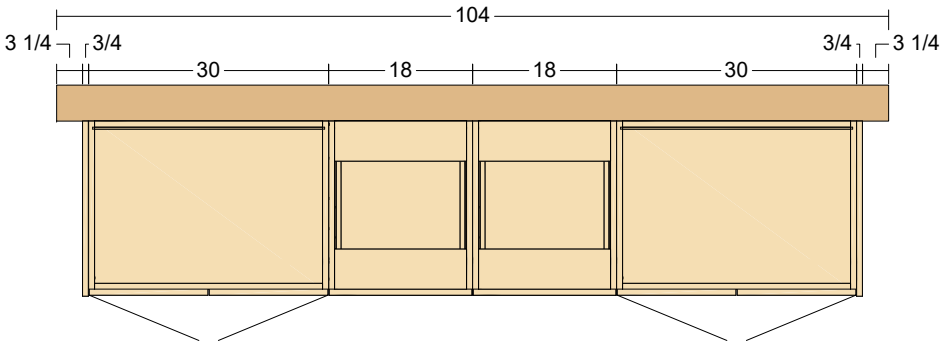




Wall #1

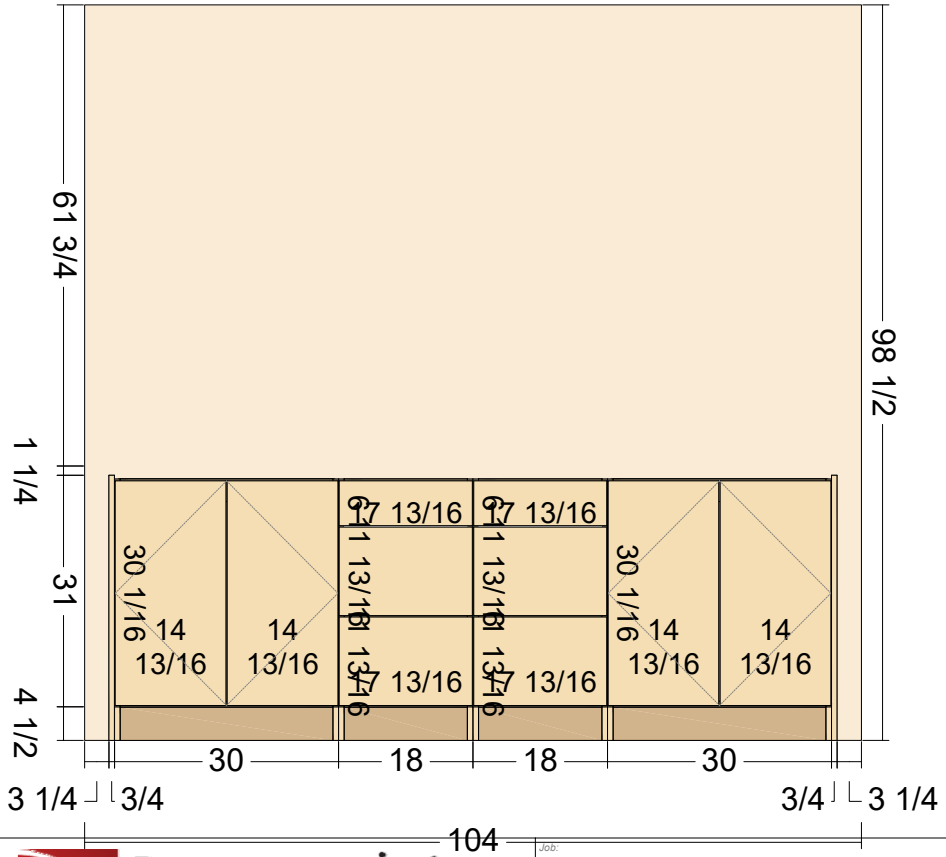

Peppermint Cabinets & More	Job: RAC-Oak Valley Estates 5	Address:	Scale: 1/2" = 1'	Page: 7/11
	Drawing Title: *Master Bath*	Phone:	Date: 08/27/2026	
		E-Mail:	Revision: 1.0	

Casita Kitchen

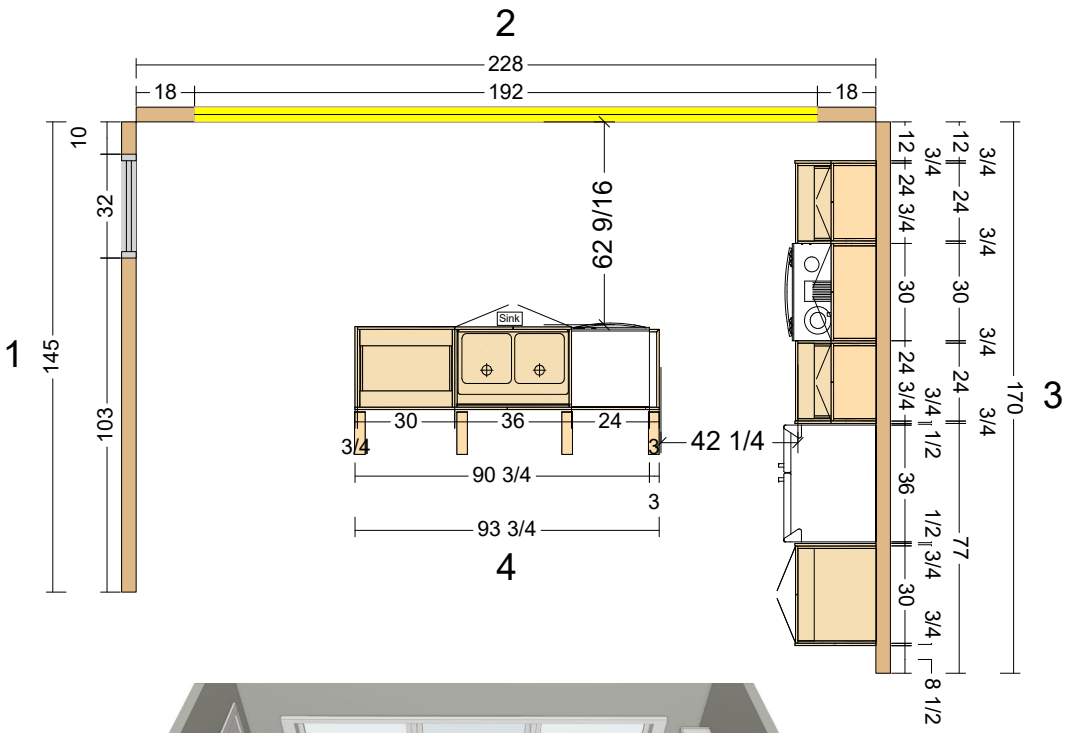











Peppermint Cabinets & More	Job: **RAC-Oak Valley Estates 5**	Address:	Scale: **1/2" = 1'**	Page: **8/11**
	Drawing Title: ***Casita Kitchen***	Phone:	Date: **08/27/2026**	
		E-Mail:	Revision: **1.0**	

Wall #3

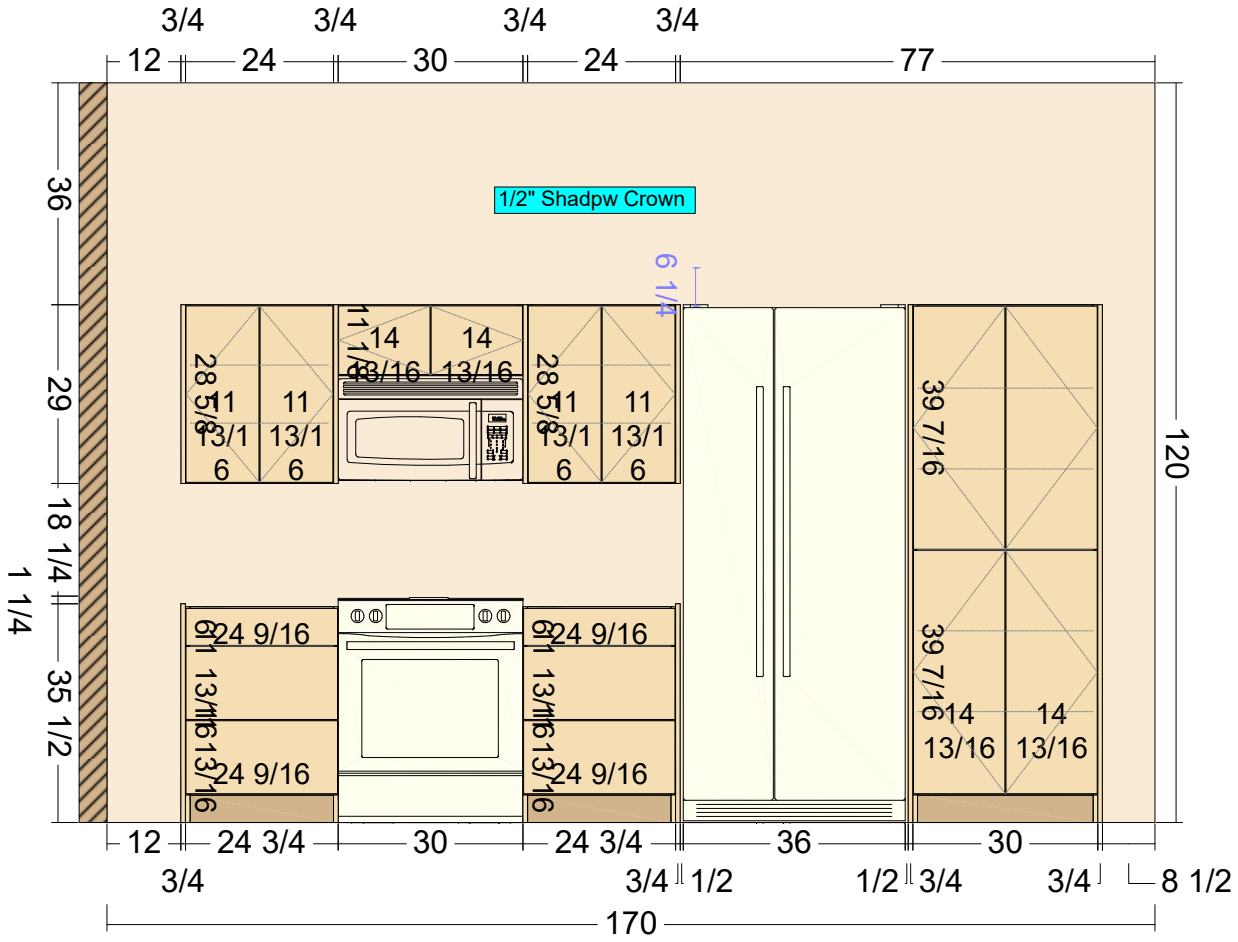

Wall #4

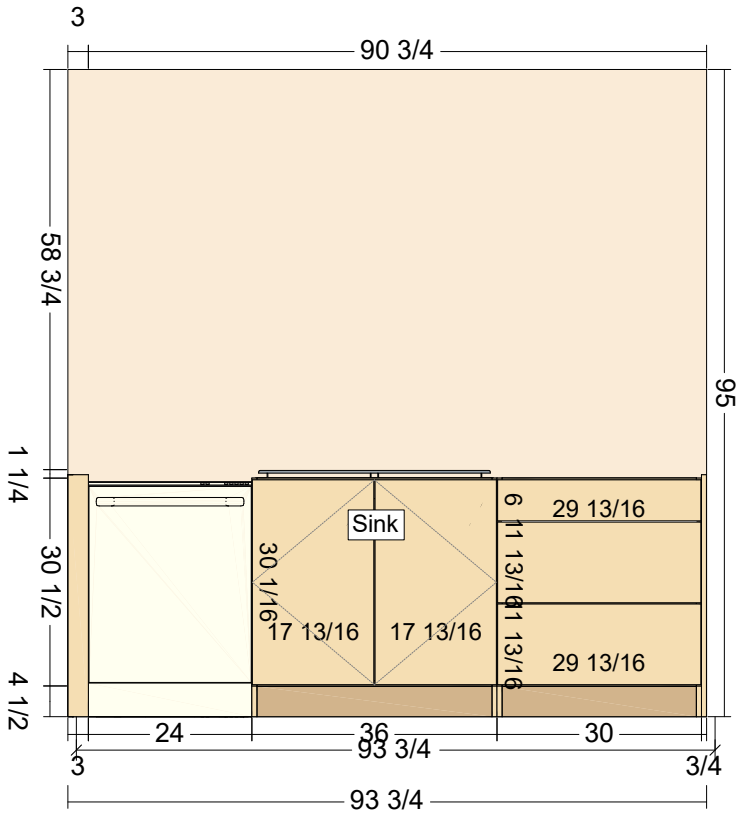


Peppermint Cabinets & More

Job: RAC-Oak Valley Estates 5	Address:	Scale: 1/2" = 1'	Page: 9/11
Drawing Title: *Casita Kitchen Elevations*	Phone:	Date: 08/27/2026	
	E-Mail:	Revision: 1.0	


Casita Bath ADU

1

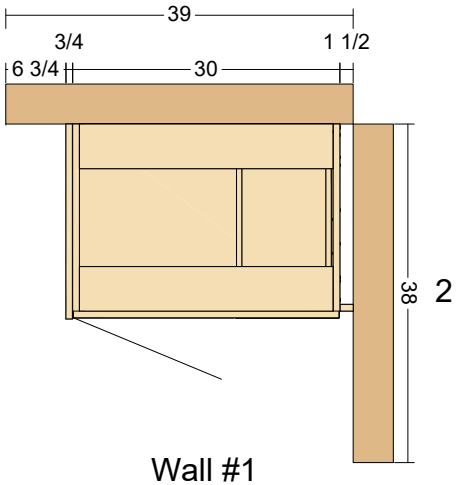




Wall #1

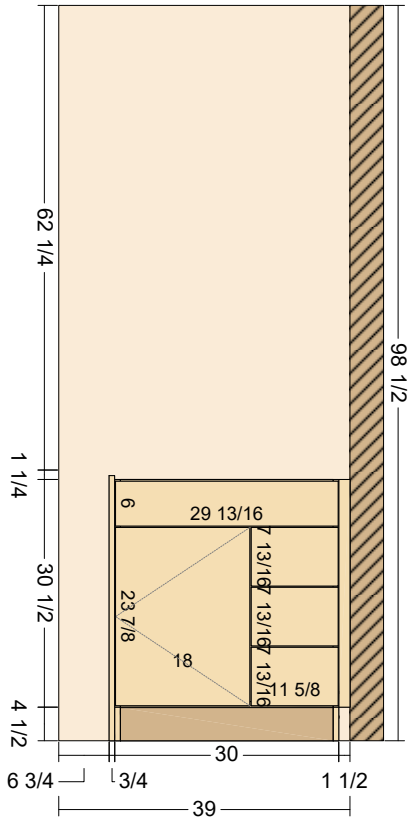


Peppermint Cabinets & More	Job: **RAC-Oak Valley Estates 5**	Address:	Scale: **1/2" = 1'**	Page: **10/11**
	Drawing Title: ***Casita Bath/ADU***	Phone:	Date: **08/27/2026**	
		E-Mail:	Revision: **1.0**	

Basement Bathroom



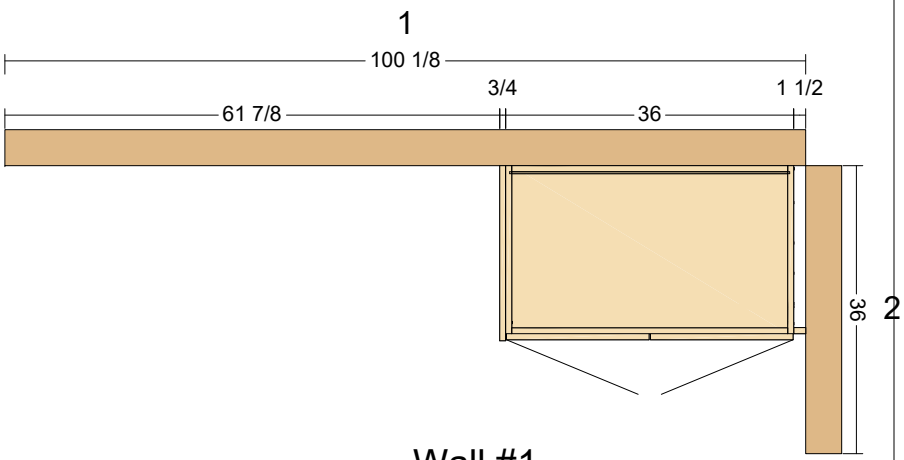

Wall #1

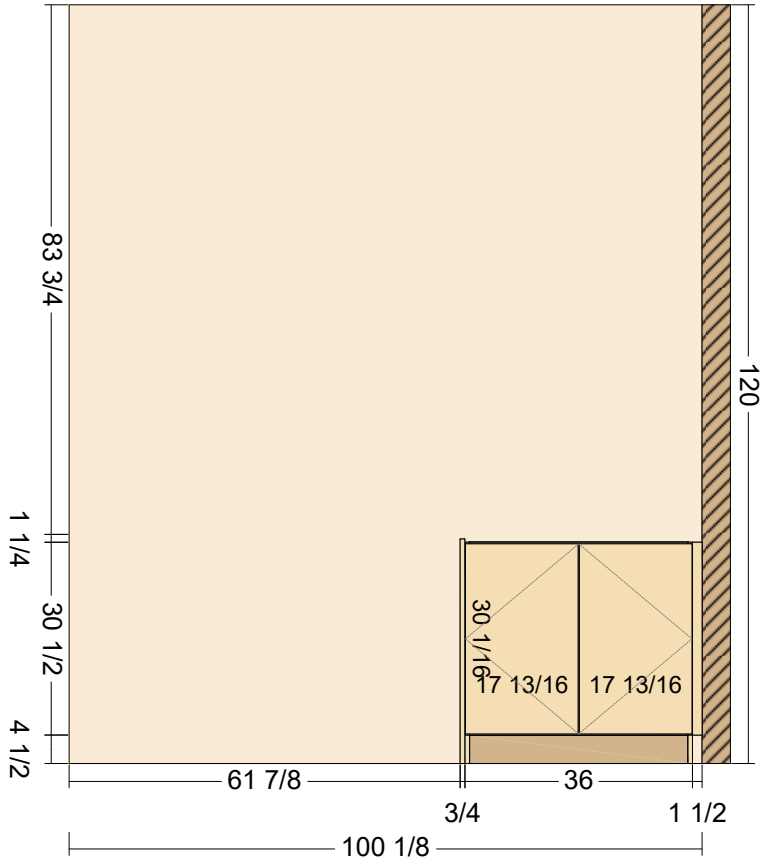

Peppermint Cabinets & More	Job: RAC-Oak Valley Estates 5	Address:	Scale: 1/2" = 1'	Page: 11/11
	Drawing Title: *Basement Bathroom*	Phone:	Date: 08/27/2026	
		E-Mail:	Revision: 1.0	