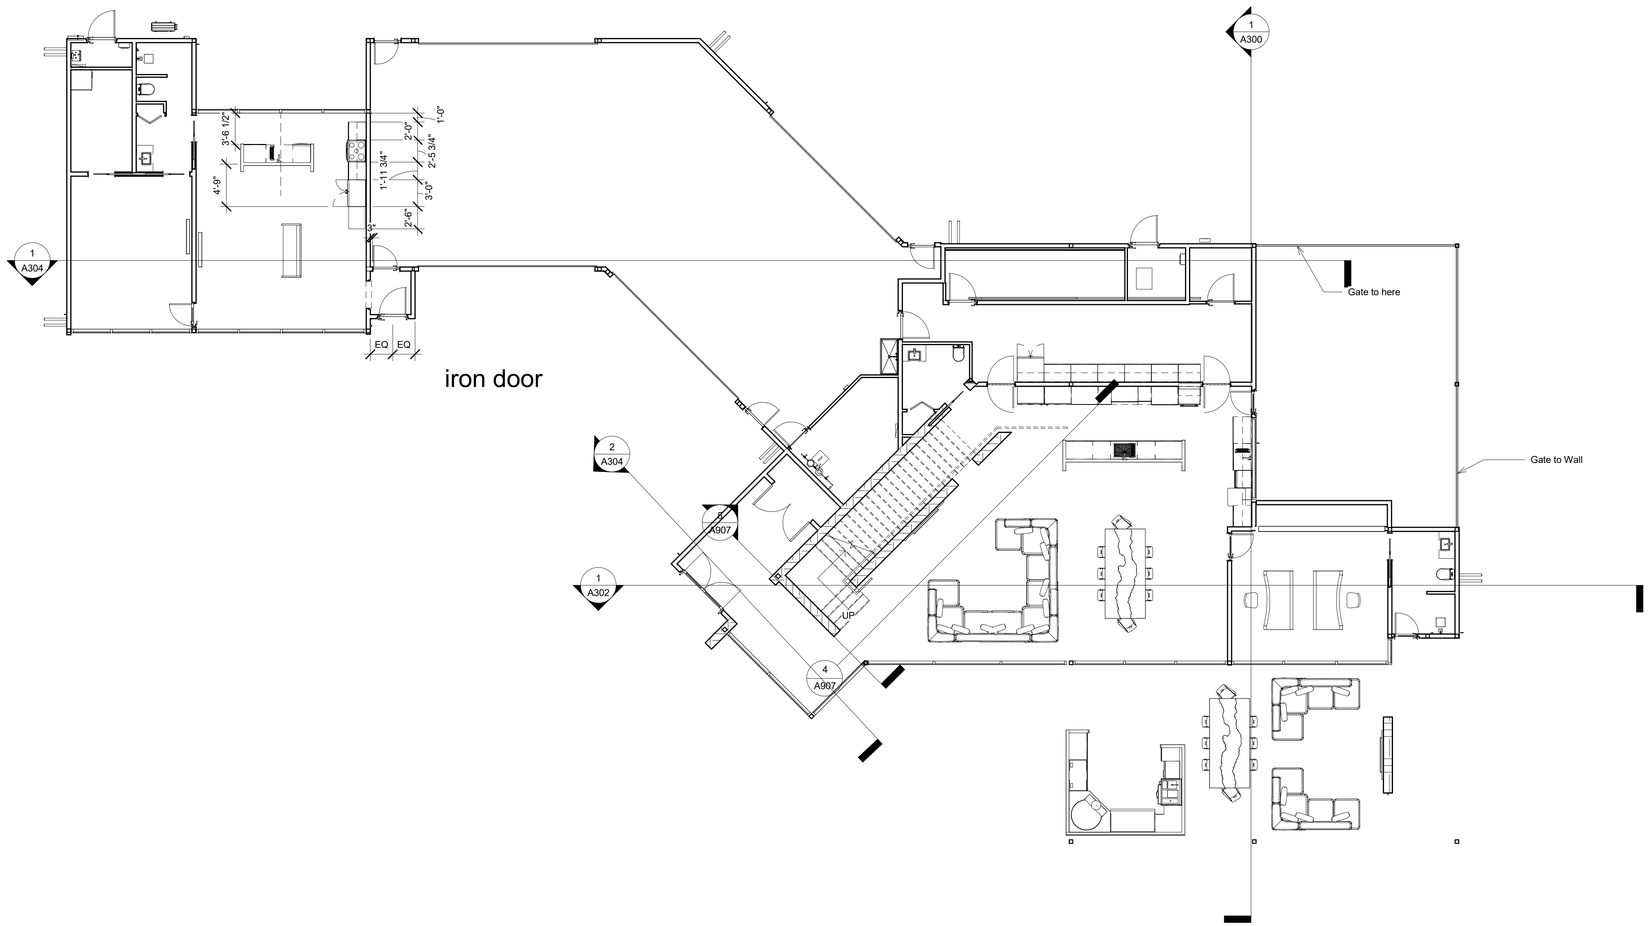


1 2-Main
1/8" = 1'-0"

RAC Development

Consultant Craig Engel
Firm RAC Development
Address 1267 N., 1390 W . St. George UT
Phone (435) 229-7360
Fax
e-mail racinc19@gmail.com

Consultant
Firm
Address
Phone
Fax
e-mail

Consultant
Firm
Address
Phone
Fax
e-mail

Consultant
Firm
Address
Phone
Fax
e-mail

Consultant
Firm
Address
Phone
Fax
e-mail

No.	Description	Date

Mr. & Mrs. Rodriguez

Oak Valley Estates #5


Main

Project number	Project Number
Date	Issue Date
Drawn by	Author
Checked by	Checker

A100

Scale 1/8" = 1'-0"

7/22/2026 2:17:57 PM

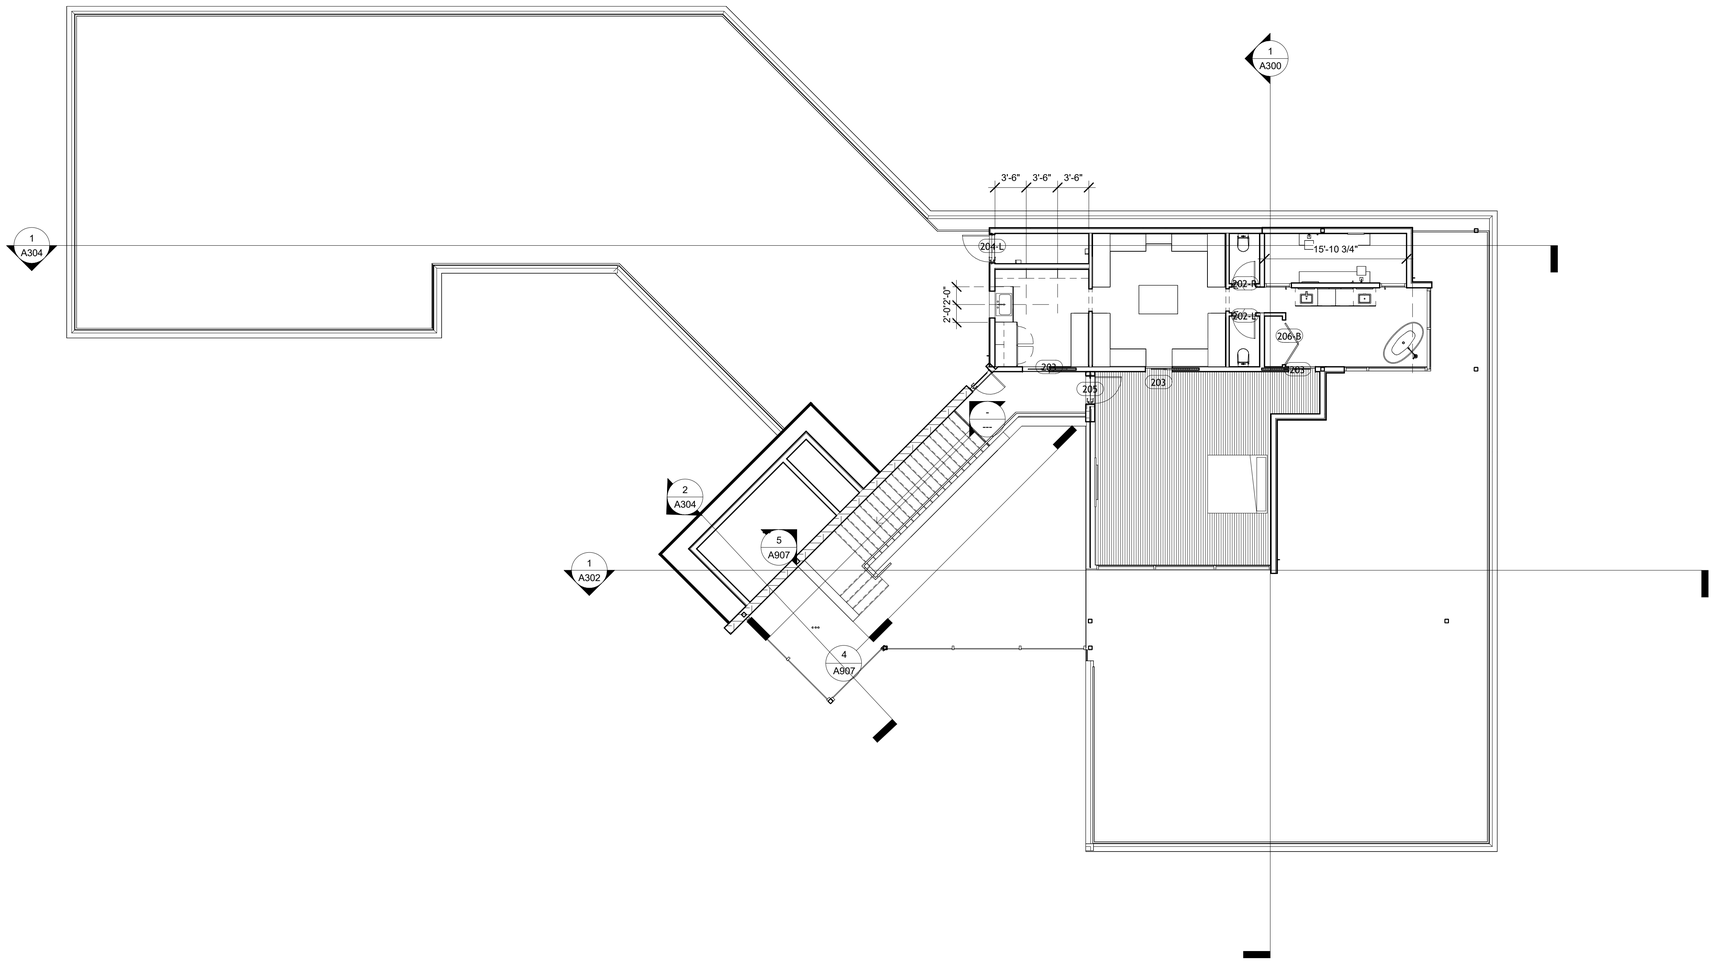

1 3-Upper
1/8" = 1'-0"

Consultant Craig Engel
Firm RAC Development
Address 1267 N.. 1390 W . St. George UT
Phone (435) 229-7360
Fax
e-mail racinc19@gmail.com

Consultant
Firm
Address
Phone
Fax
e-mail

Consultant
Firm
Address
Phone
Fax
e-mail

Consultant
Firm
Address
Phone
Fax
e-mail

Consultant
Firm
Address
Phone
Fax
e-mail

No.	Description	Date

Mr. & Mrs. Rodriguez

Oak Valley Estates #5


Upper

Project number	Project Number
Date	Issue Date
Drawn by	Author
Checked by	Checker


A102

Scale 1/8" = 1'-0"


7/22/2026 2:17:58 PM

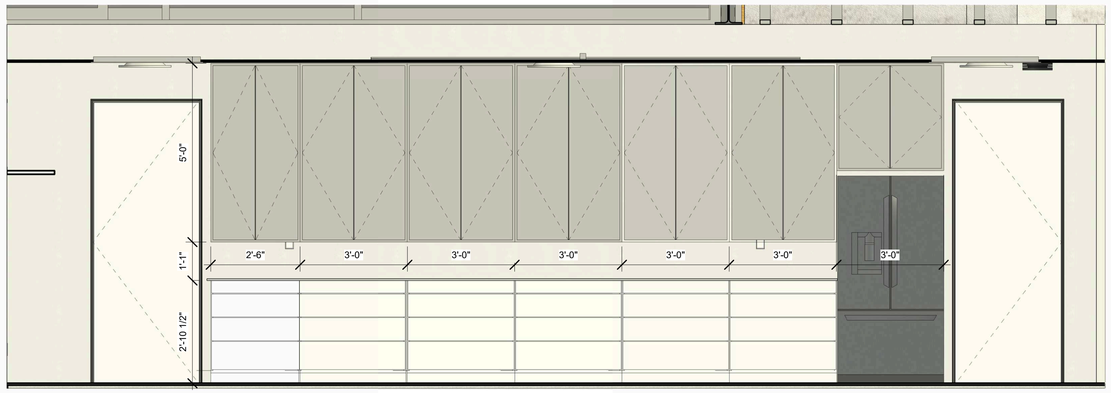


6 Cab Pantry
1/2" = 1'-0"

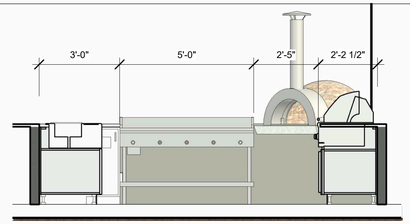


7 Cab Outdoor East
3/8" = 1'-0"

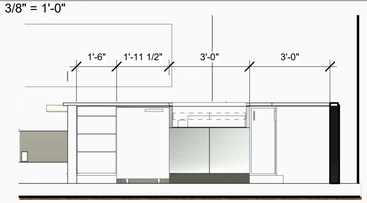

8 Cab Outdoor North
3/8" = 1'-0"

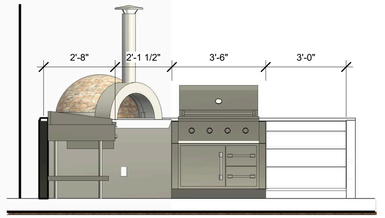

9 Cab Outdoor South
3/8" = 1'-0"

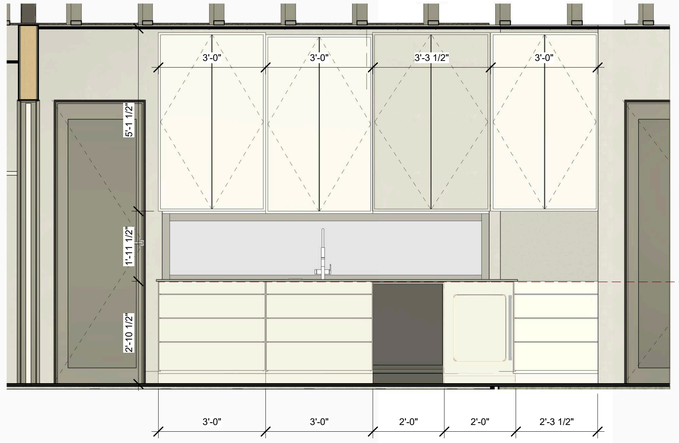





4 Cab Office Bath
1/2" = 1'-0"



5 Cab Powder
1/2" = 1'-0"

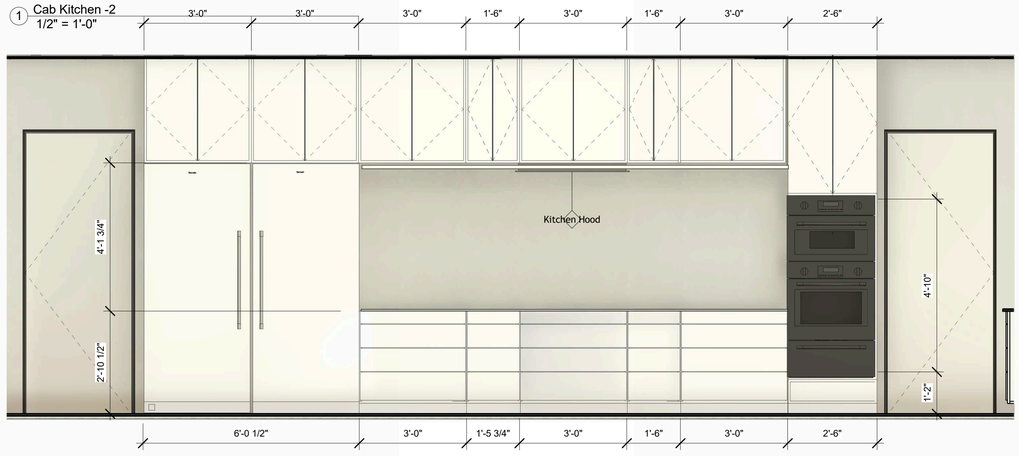

1 Cab Kitchen -2
1/2" = 1'-0"

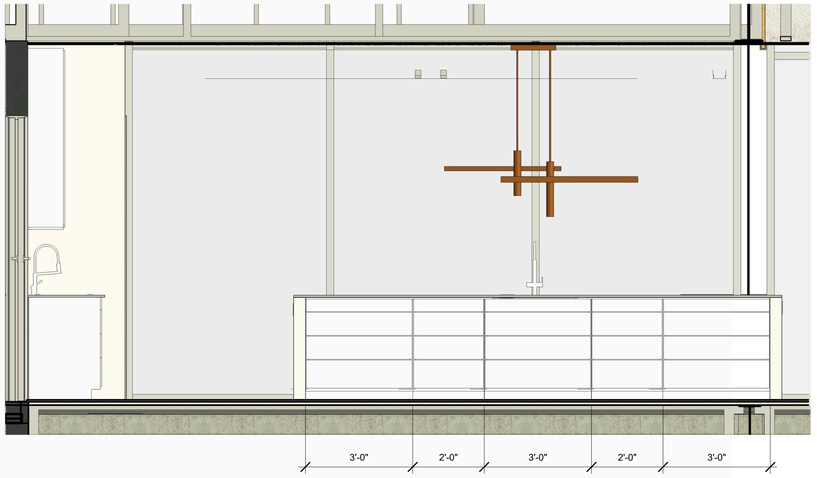

2 Cab Kitchen ISL-1
1/2" = 1'-0"

3 Cab KItchen-1
1/2" = 1'-0"

RAC Development

Consultant Craig Engel
Firm RAC Development
Address 1267 N.. 1390 W . St. George UT
Phone (435) 229-7360
Fax
e-mail racinc19@gmail.com

Consultant
Firm
Address
Phone
Fax
e-mail

Consultant
Firm
Address
Phone
Fax
e-mail

Consultant
Firm
Address
Phone
Fax
e-mail

Consultant
Firm
Address
Phone
Fax
e-mail

No.	Description	Date

Mr. & Mrs. Rodriguez

Oak Valley Estates #5


Cabinets Main

Project number	Project Number
Date	Issue Date
Drawn by	Author
Checked by	Checker

A901

Scale As indicated

7/22/2026 2:18:08 PM

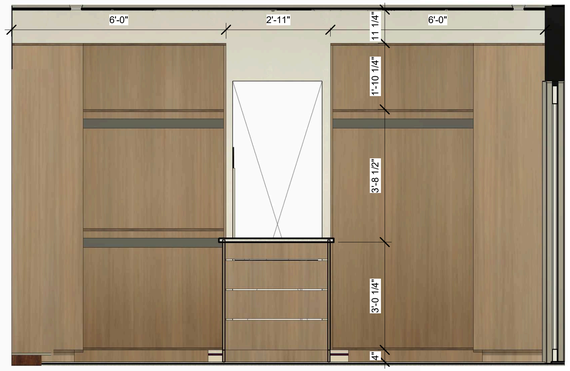


2 Cab P-Closet North
1/2" = 1'-0"



3 Cab P-Closet South
1/2" = 1'-0"




1 Cab Laundry North
1/2" = 1'-0"

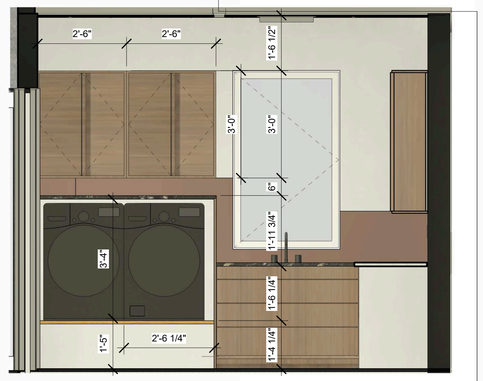


4 Cab Laundry South
1/2" = 1'-0"


12 Cab Upper East
1/2" = 1'-0"

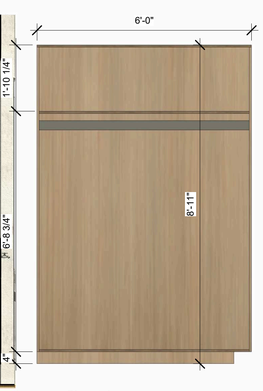


5 Closet 1
1/2" = 1'-0"

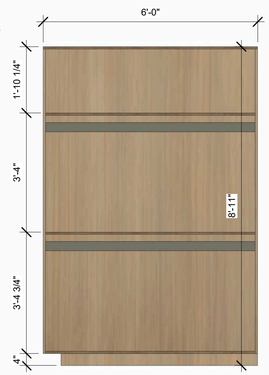


6 Closet 2
1/2" = 1'-0"

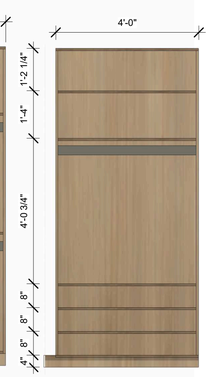

7 Closet 3
1/2" = 1'-0"

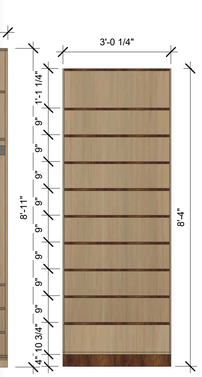

8 Closet 4
1/2" = 1'-0"

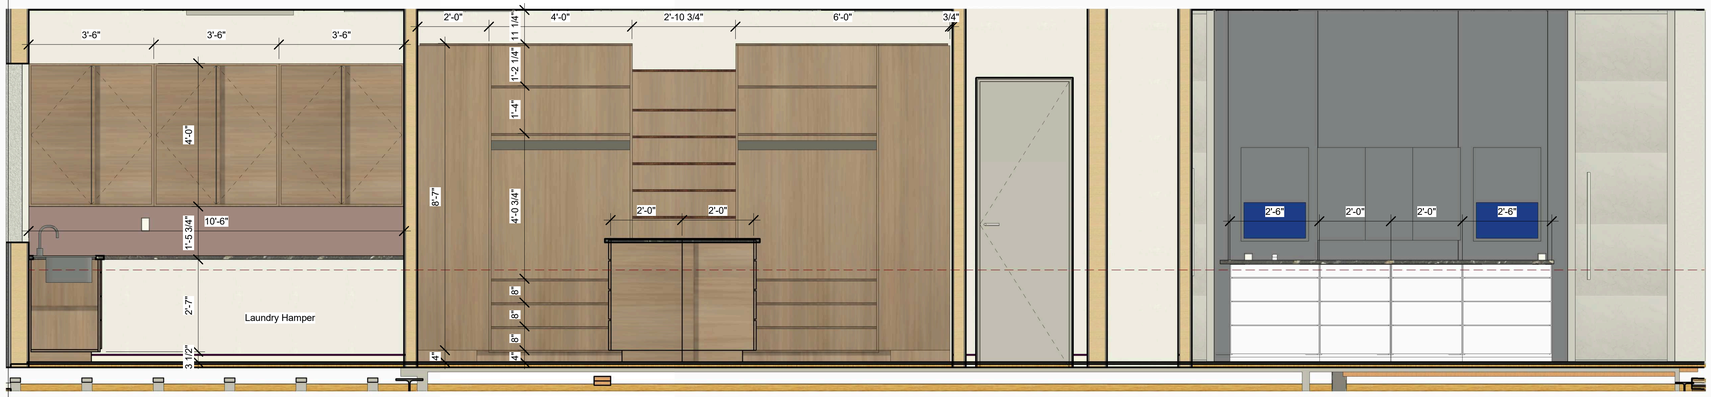

13 Cab Upper West
1/2" = 1'-0"

RAC Development

Consultant Craig Engel
Firm RAC Development
Address 1267 N.. 1390 W . St. George UT
Phone (435) 229-7360
Fax
e-mail racinc19@gmail.com

Consultant
Firm
Address
Phone
Fax
e-mail

Consultant
Firm
Address
Phone
Fax
e-mail

Consultant
Firm
Address
Phone
Fax
e-mail

Consultant
Firm
Address
Phone
Fax
e-mail

No.	Description	Date


Mr. & Mrs. Rodriguez
Oak Valley Estates #5
Cabinets Upper

Project number	Project Number
Date	Issue Date
Drawn by	Author
Checked by	Checker


A902

Scale 1/2" = 1'-0"


7/22/2026 2:18:18 PM

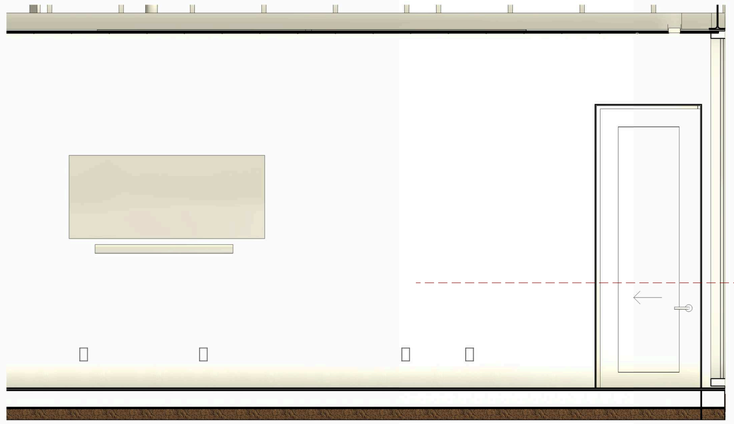


4 Cab ADU-2
1/2" = 1'-0"

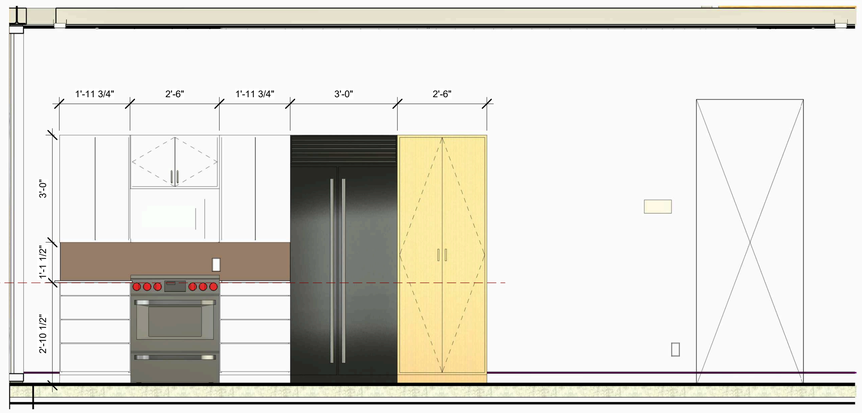


1 Cab ADU -1
1/2" = 1'-0"

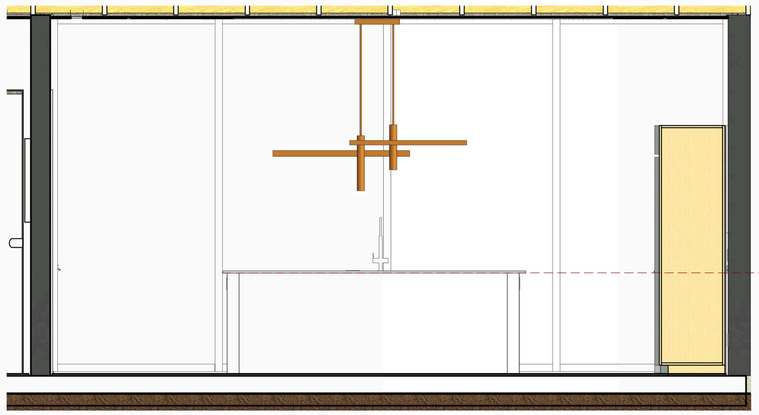


3 Cab ADU ISL-1
1/2" = 1'-0"

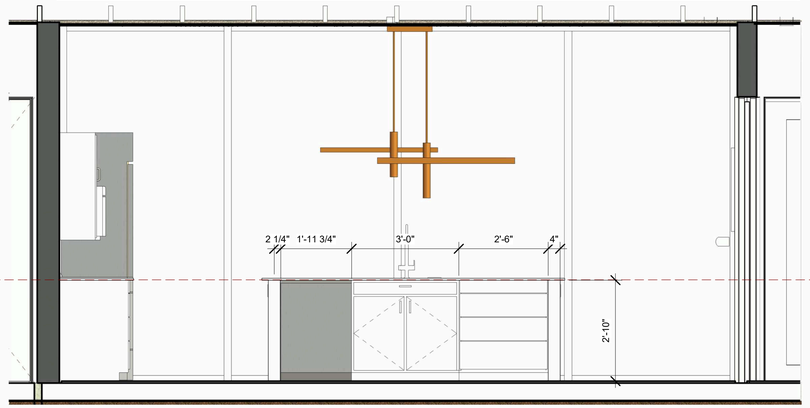


5 Cab ADU ISL-2
1/2" = 1'-0"

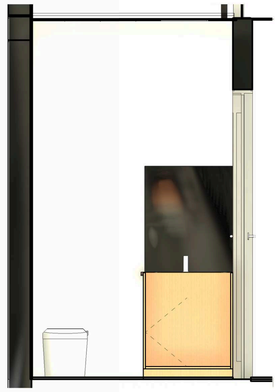

7 Cab Lower-1
1/2" = 1'-0"

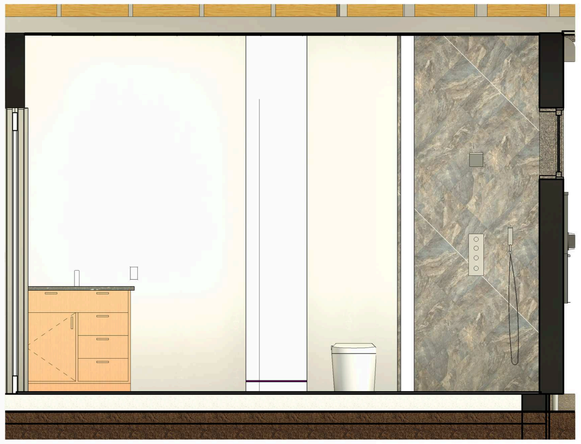

2 Cab ADU Bath
1/2" = 1'-0"

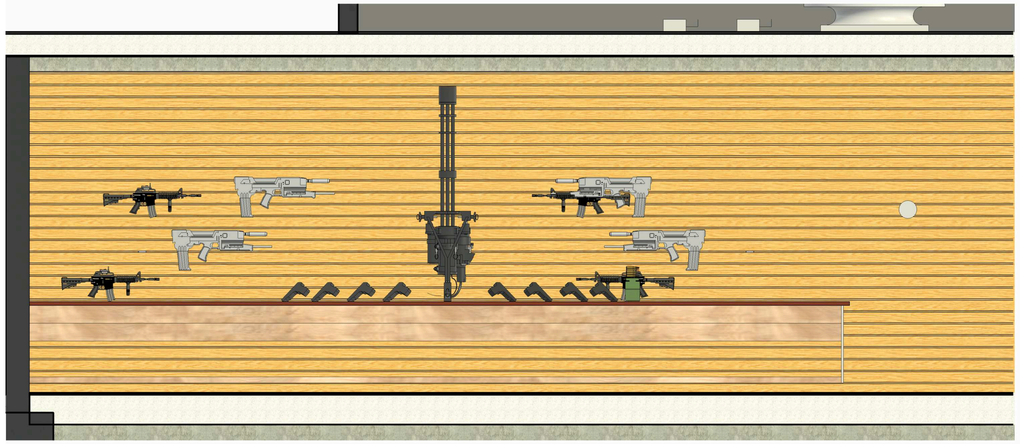

6 Cab Gun Room
1/2" = 1'-0"

RAC Development

Consultant Craig Engel
Firm RAC Development
Address 1267 N.. 1390 W . St. George UT
Phone (435) 229-7360
Fax
e-mail racinc19@gmail.com

Consultant
Firm
Address
Phone
Fax
e-mail

Consultant
Firm
Address
Phone
Fax
e-mail

Consultant
Firm
Address
Phone
Fax
e-mail

Consultant
Firm
Address
Phone
Fax
e-mail

No.	Description	Date

Mr. & Mrs. Rodriguez

Oak Valley Estates #5

Cabniets ADU/Lower

Project number	Project Number
Date	Issue Date
Drawn by	Author
Checked by	Checker

A903

Scale 1/2" = 1'-0"

7/22/2026 2:18:27 PM