

1


255
4 3/4
3/4
16 3/4
3/4
3/4
16 3/4
3/4
4 3/4
31
31
35 3/4
45 1/2
35 3/4
30
43/4
1
3/4
3/4
3/4
4
30
30
36
22
36
22
36
30

2


30
36
4
3/4
30
30
24
24
28
Sink
Waste
40
3/4
27
27
28
27
27
3/4
189
3/4
11 1/2
11 1/2
33


3

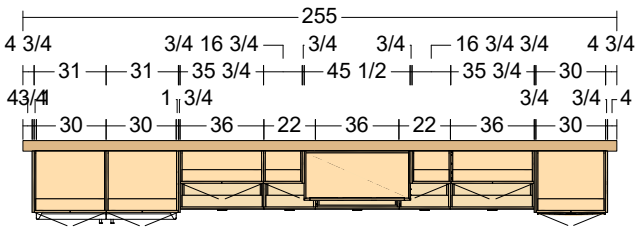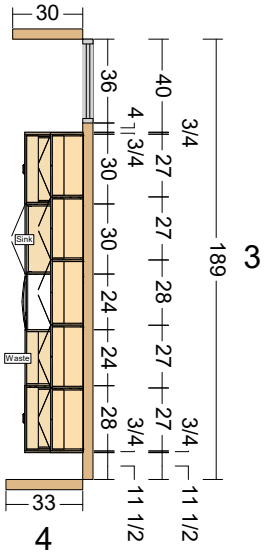






5

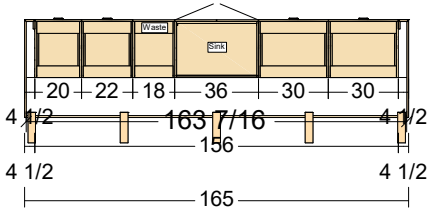

Waste
Sink
20
22
18
36
30
30
4 1/2
163 7/16
4 1/2
156
4 1/2
4 1/2
165

4


Wall #1

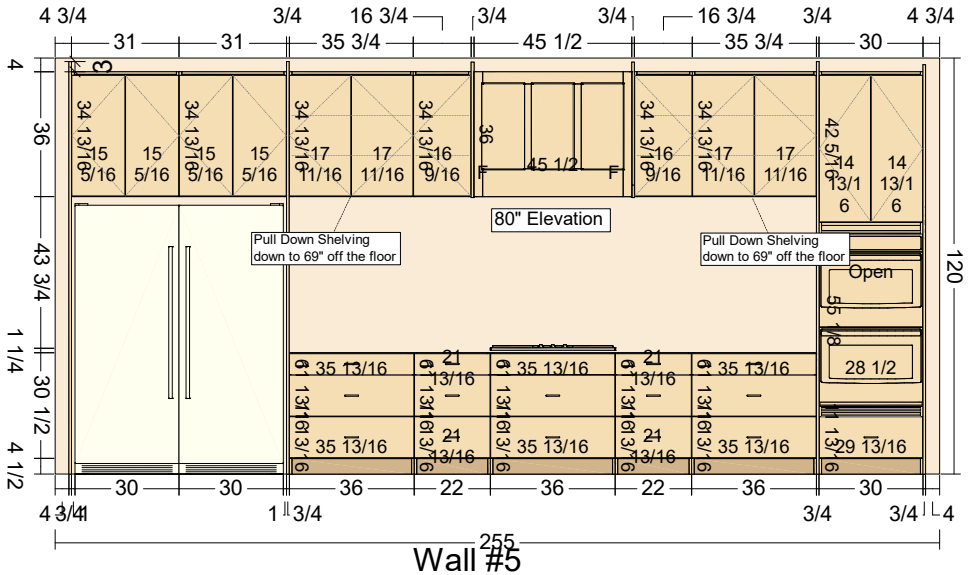


Wall #3

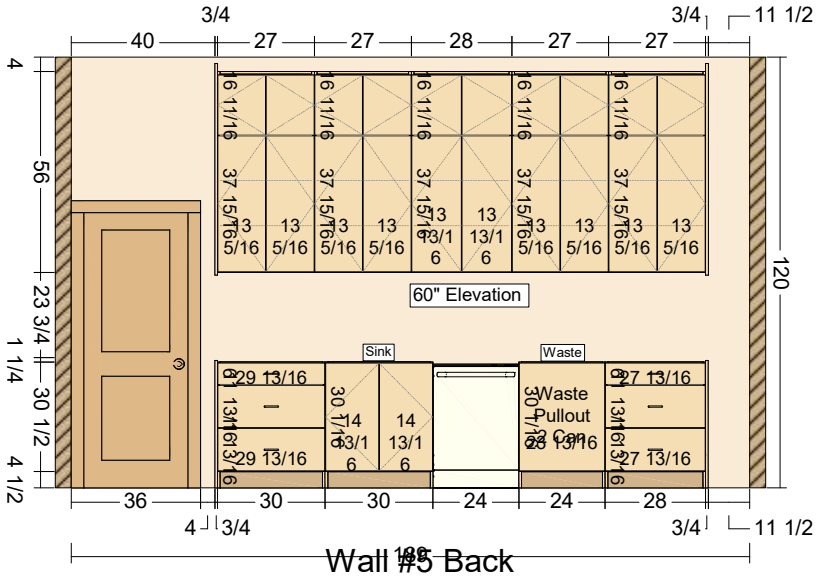

Wall #5

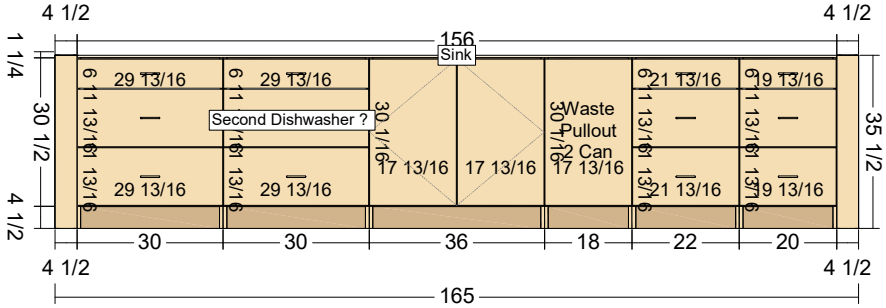

Wall #5 Back

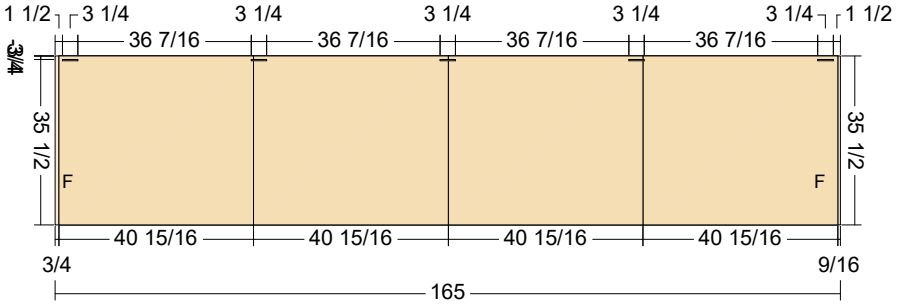




Peppermint Cabinets & More	Job: RAC-OVE lot 5	Address:	Scale: 1/2" = 1'	Page: 2/9
	Drawing Title: *Kitchen Elevations*	Phone:	Date: 03/25/2026	
		E-Mail:	Revision: 1.0	




Pantry

1

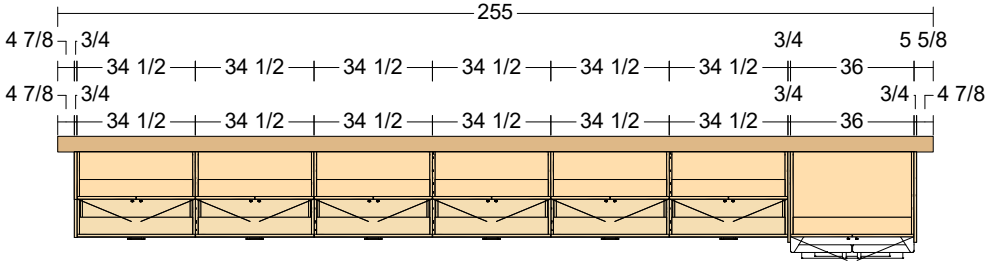


Wall #1

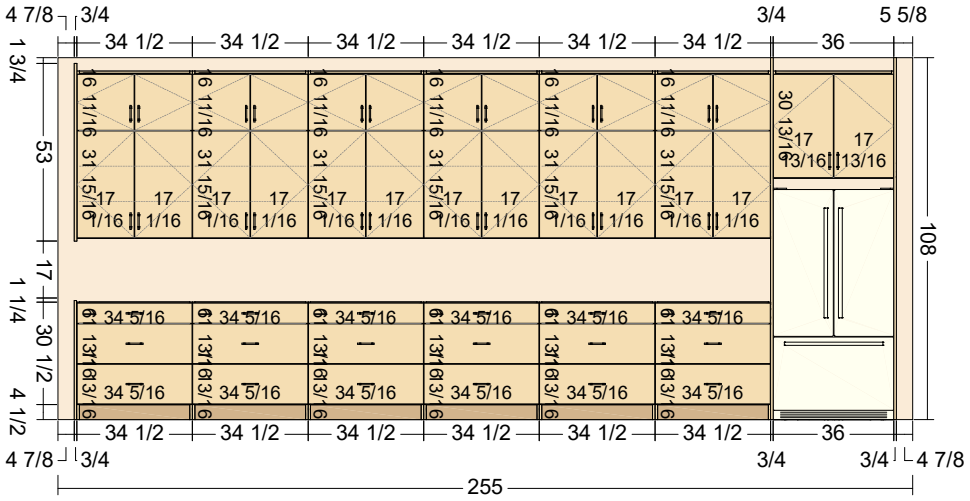

Peppermint Cabinets & More	Job: **RAC-OVE lot 5**	Address:	Scale: **1/2" = 1'**	Page: **3/9**
	Drawing Title: ***Pantry***	Phone:	Date: **03/25/2026**	
		E-Mail:	Revision: **1.0**	


Powder Bath

2

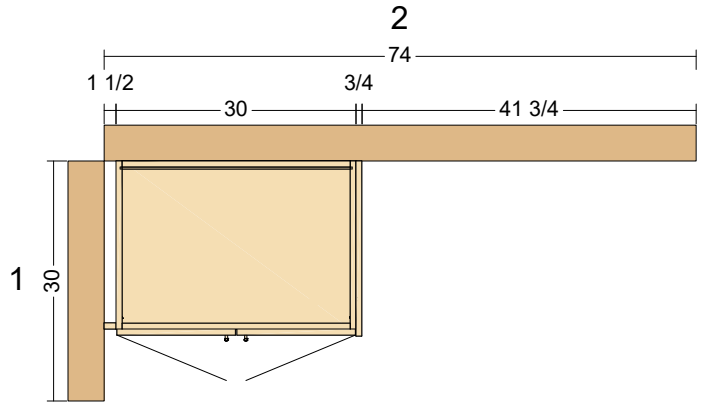




Wall #2

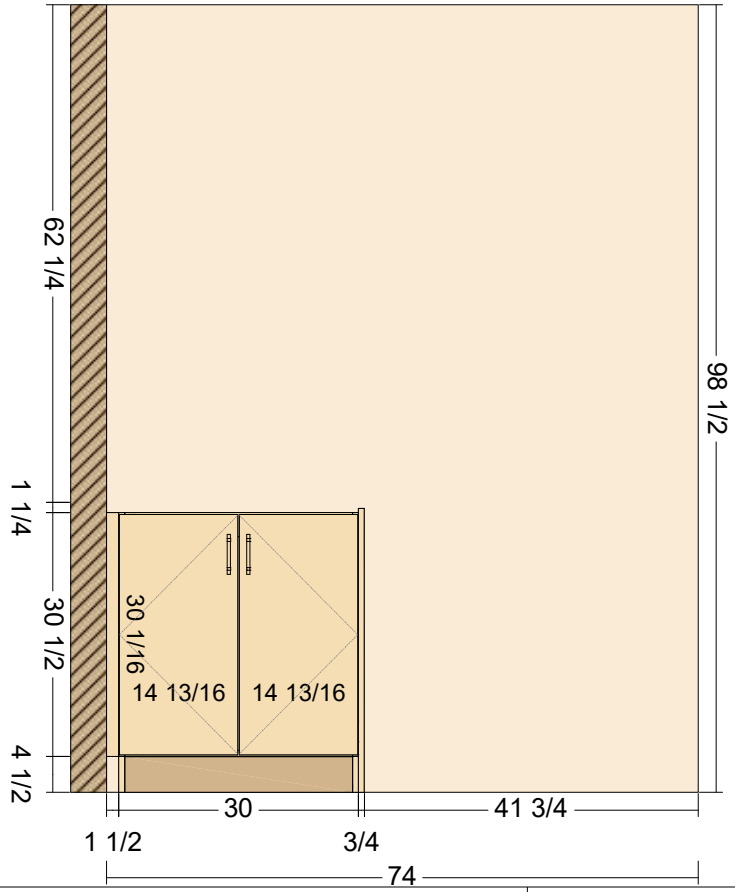

Peppermint Cabinets & More	Job: **RAC-OVE lot 5**	Address:	Scale: **1/2" = 1'**	Page: **4/9**
	Drawing Title: ***Powder Bath***	Phone:	Date: **03/25/2026**	
		E-Mail:	Revision: **1.0**	


Office Bath

2

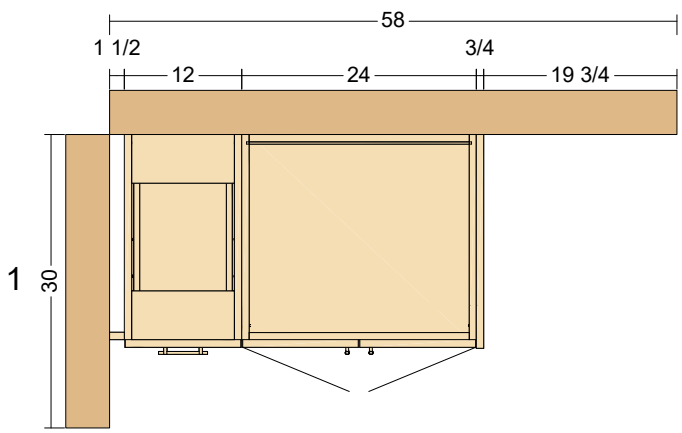

Wall #2




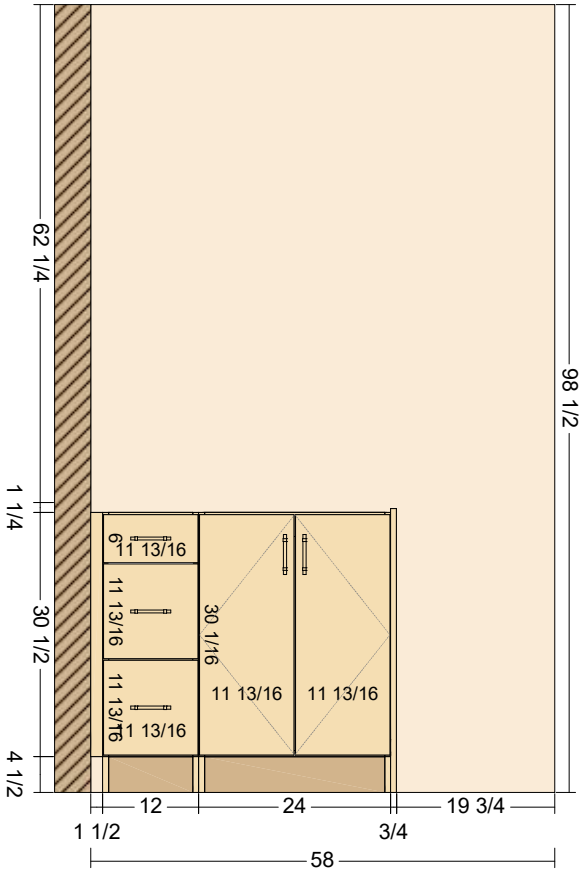

Peppermint Cabinets & More	Job: **RAC-OVE lot 5**	Address:	Scale: **1/2" = 1'**	Page: **5/9**
	Drawing Title: ***Office Bath***	Phone:	Date: **03/25/2026**	
		E-Mail:	Revision: **1.0**	


Master Bath

1

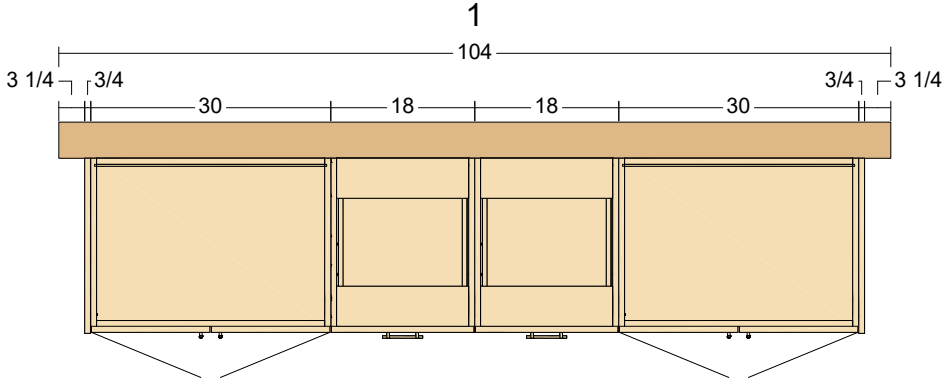




Wall #1

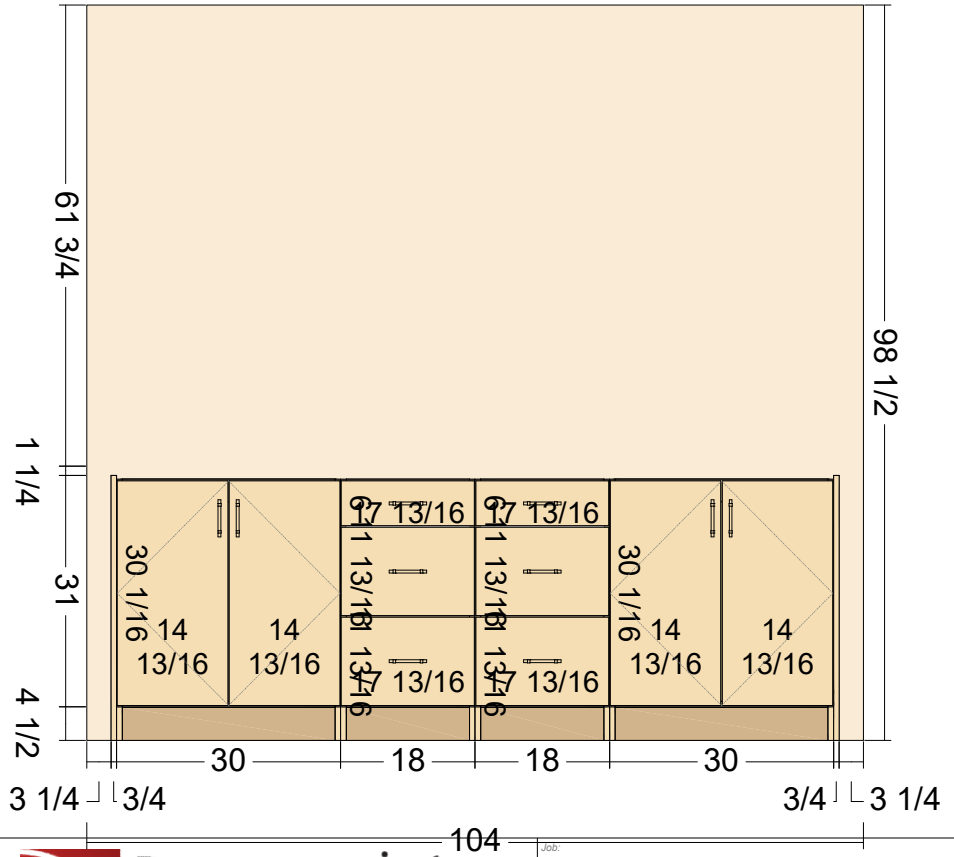

Peppermint Cabinets & More	Job: RAC-OVE lot 5	Address:	Scale: 1/2" = 1'	Page: 6/9
	Drawing Title: *Master Bath*	Phone:	Date: 03/25/2026	
		E-Mail:	Revision: 1.0	

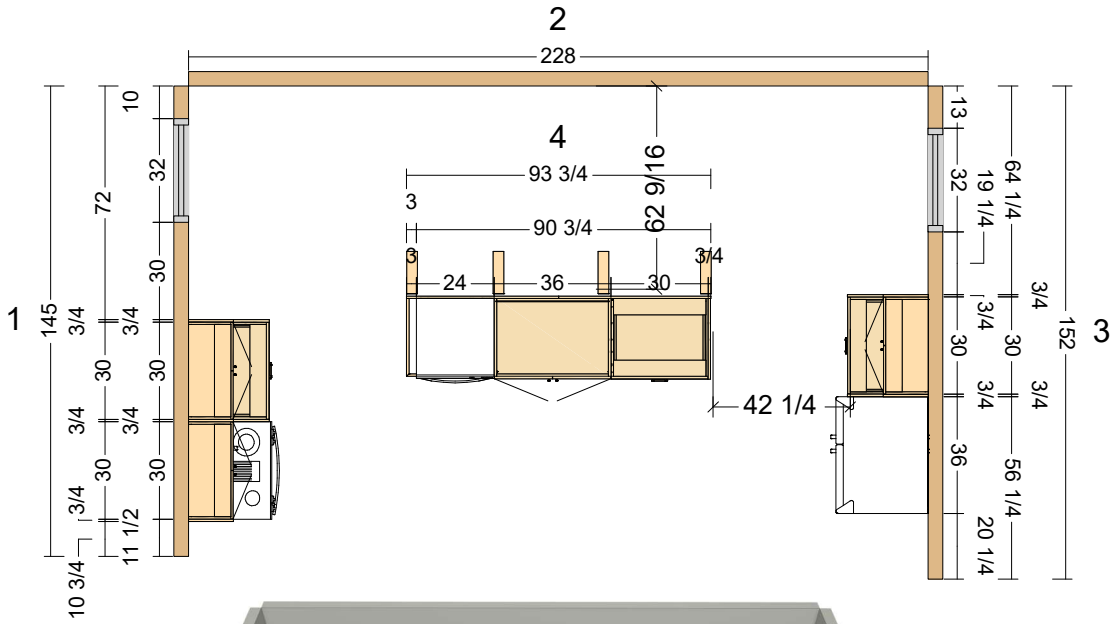











Peppermint Cabinets & More	Job: **RAC-OVE lot 5**	Address:	Scale: **1/2" = 1'**	Page: **7/9**
	Drawing Title: ***Casita Kitchen***	Phone:	Date: **03/25/2026**	
		E-Mail:	Revision: **1.0**	


Wall #1

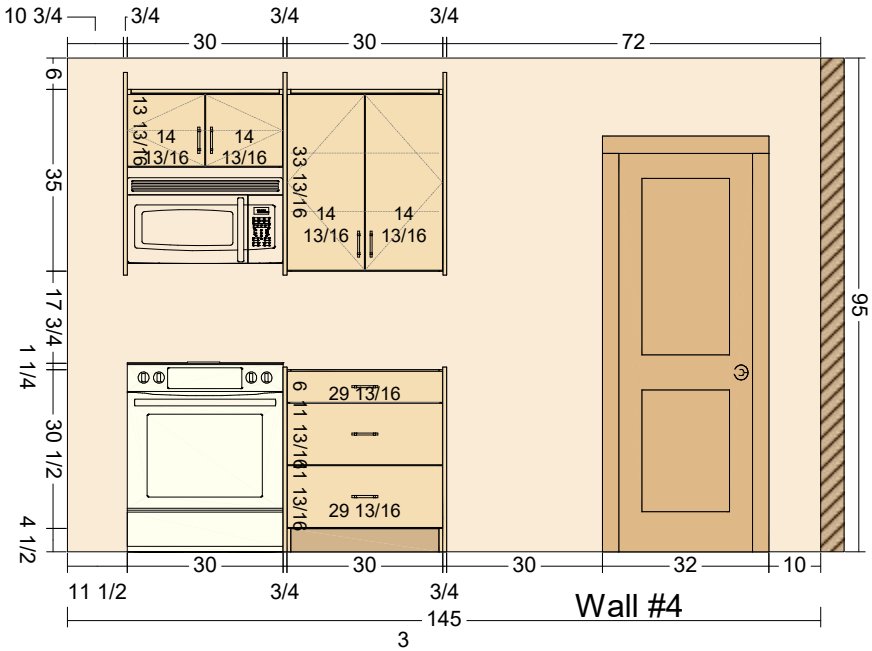


Wall #3

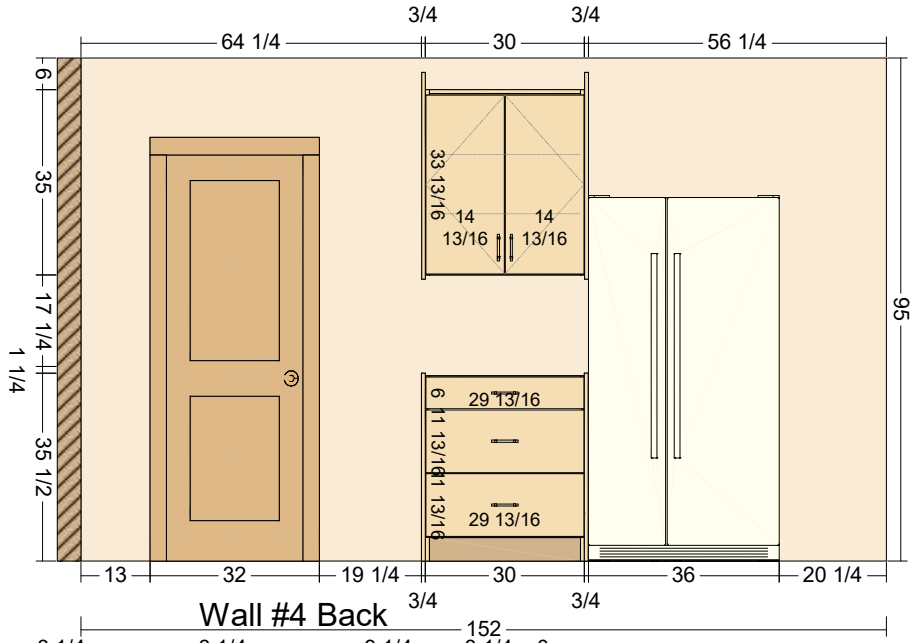

Wall #4

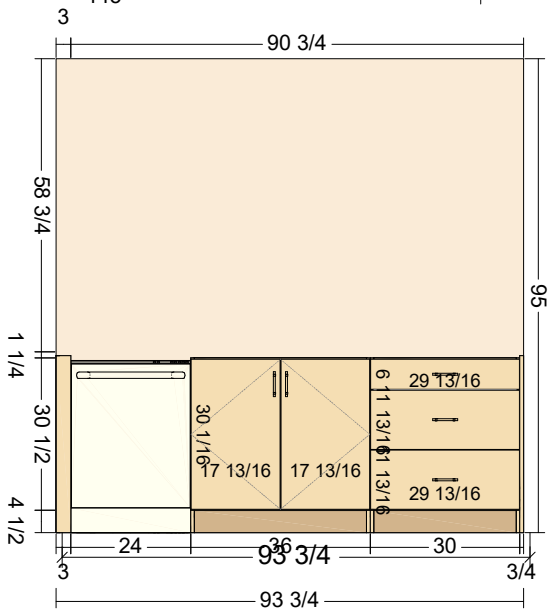

Wall #4 Back

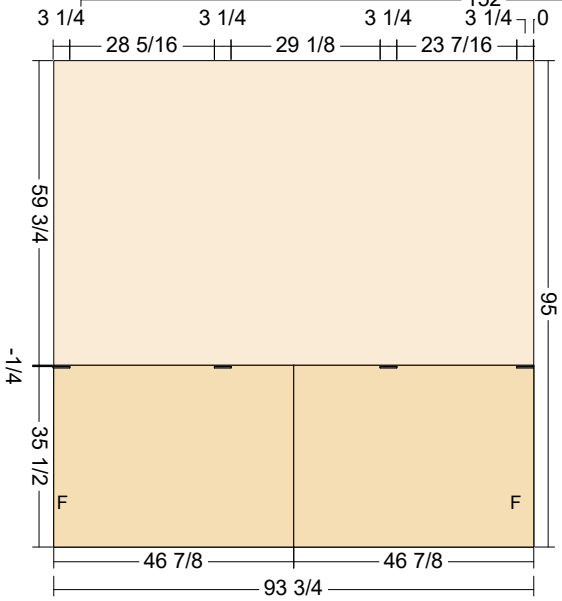


Peppermint Cabinets & More


Job: **RAC-OVE lot 5**	Address:	Scale: **1/2" = 1'**	Page: **8/9**
Drawing Title: ***Casita Kitchen Elevations***	Phone:	Date: **03/25/2026**	
	E-Mail:	Revision: **1.0**	

Casita Bath

1

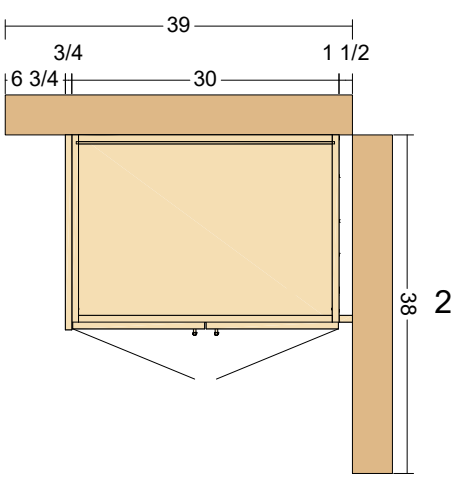

Wall #1

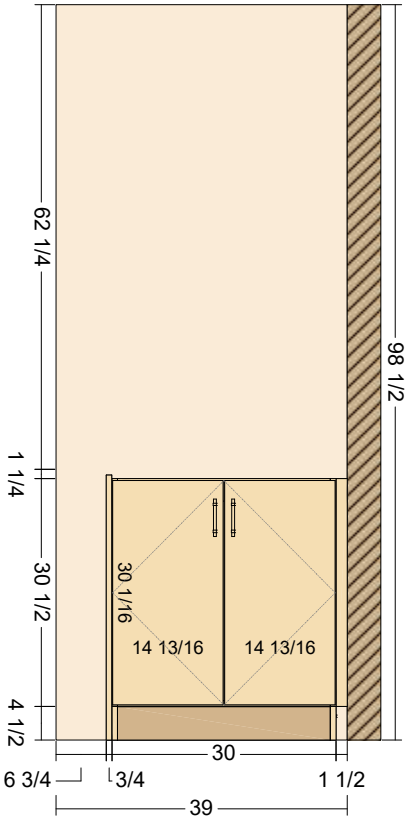



Peppermint Cabinets & More	Job: RAC-OVE lot 5	Address:	Scale: 1/2" = 1'	Page: 9/9
	Drawing Title: *Casita Bath*	Phone:	Date: 03/25/2026	
		E-Mail:	Revision: 1.0	