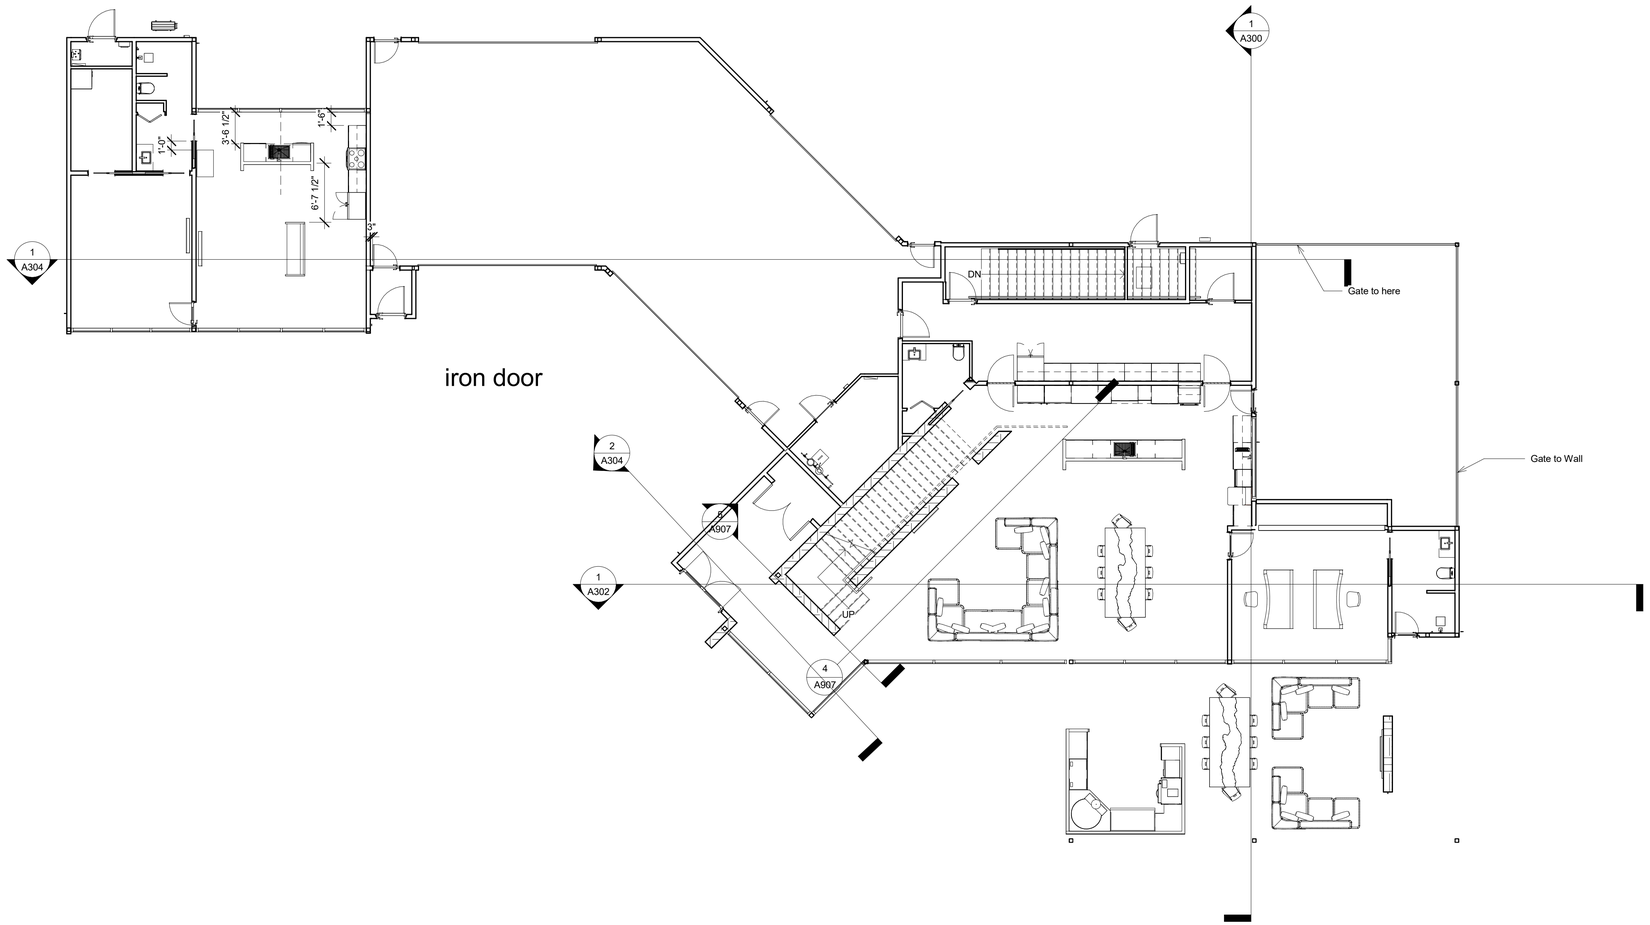


1 2-Main
1/8" = 1'-0"

RAC Development

Consultant Craig Engel
Firm RAC Development
Address 1267 N., 1390 W . St. George UT
Phone (435) 229-7360
Fax
e-mail racinc19@gmail.com

Consultant
Firm
Address
Phone
Fax
e-mail

Consultant
Firm
Address
Phone
Fax
e-mail

Consultant
Firm
Address
Phone
Fax
e-mail

Consultant
Firm
Address
Phone
Fax
e-mail

No.	Description	Date

Mr. & Mrs. Rodriguez

Oak Valley Estates #5


Main


Project number	Project Number
Date	Issue Date
Drawn by	Author
Checked by	Checker

A100


Scale 1/8" = 1'-0"

7/1/2026 8:33:40 AM

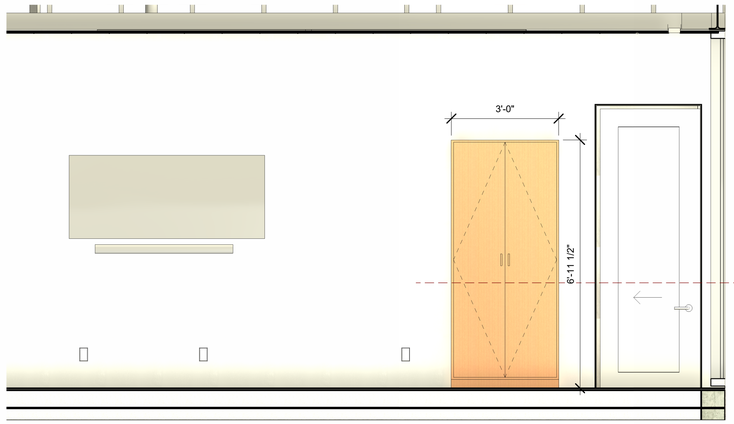

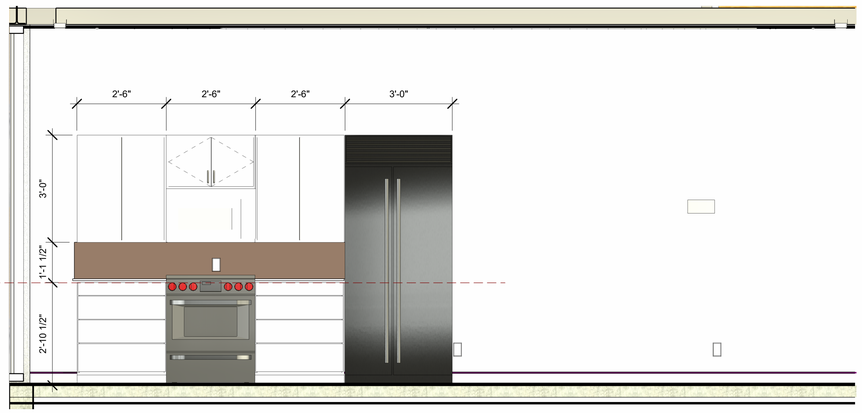


4 Cab ADU-2
1/2" = 1'-0"

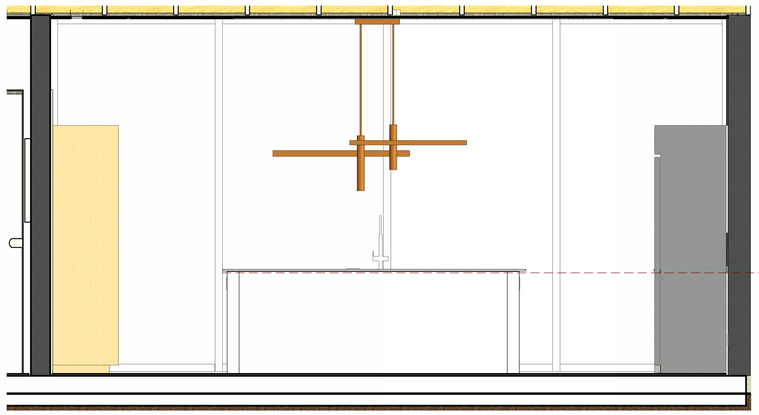


3 Cab ADU ISL-1
1/2" = 1'-0"

1 Cab ADU -1
1/2" = 1'-0"

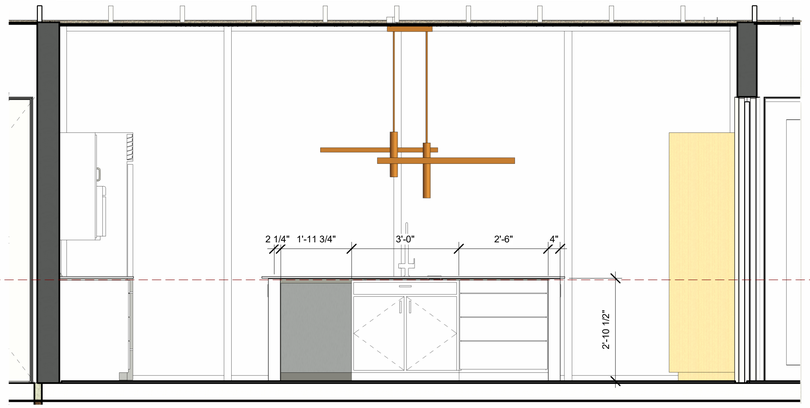


5 Cab ADU ISL-2
1/2" = 1'-0"

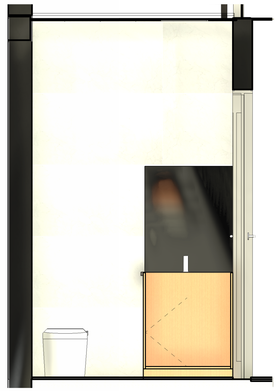

7 Cab Lower-1
1/2" = 1'-0"



2 Cab ADU Bath
1/2" = 1'-0"

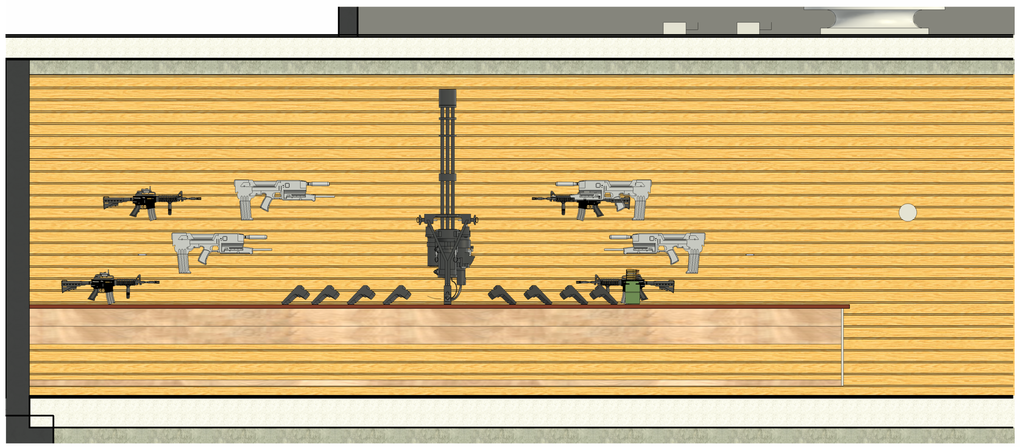

6 Cab Gun Room
1/2" = 1'-0"

RAC Development

Consultant Craig Engel
Firm RAC Development
Address 1267 N.. 1390 W . St. George UT
Phone (435) 229-7360
Fax
e-mail racinc19@gmail.com

Consultant
Firm
Address
Phone
Fax
e-mail

Consultant
Firm
Address
Phone
Fax
e-mail

Consultant
Firm
Address
Phone
Fax
e-mail

Consultant
Firm
Address
Phone
Fax
e-mail

No.	Description	Date

Mr. & Mrs. Rodriguez

Oak Valley Estates #5

Cabniets ADU/Lower

Project number	Project Number
Date	Issue Date
Drawn by	Author
Checked by	Checker

A903

Scale	1/2" = 1'-0"

7/1/2026 8:33:46 AM