



RM#1 - Kitchen	
Base Material:	Lochsa Rosewood 1mm, White Int.
Upper Material:	Lochsa Rosewood 1mm, White Int.
Construction:	Cabinets - Doweled
Drawer Box Style:	5/8 W/Dado Undermount
Door Specs	
Base Door Style:	Slab CC Door, Lochsa Rosewood 1mm
Upper Door Style:	Slab CC Door, Lochsa Rosewood 1mm
Drawer Front Style:	Slab CC Door, Lochsa Rosewood 1mm
Countertop/Moulding	
Countertop:	Supplied By Others, Granite
Moulding:	None, Lochsa Rosewood 3/4
Hardware Specs	
Drawer Guide:	PRO 600
Hinges:	Soft Silentia 120 Degree Euro
Handles:	Metro SN (Stock) STUP822BSN-128

Need Appliance Specs


All Vertical Grain

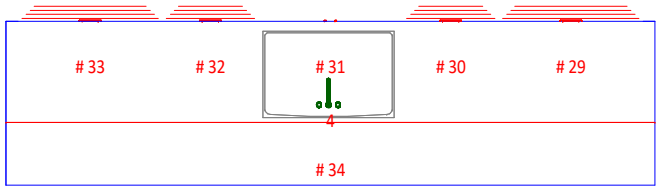

Island Top, Waterfall Ends, & Back Panel By Other Top Company

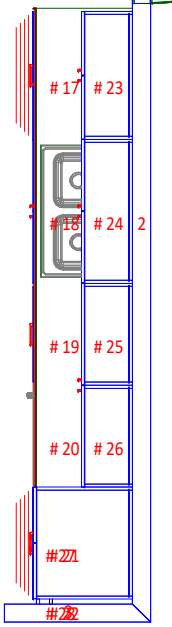


CLOSET CREATIONS	**Closet Creations** 4058 S. River Road St. George, UT 84790 Phone: 435-656-5564 Fax:	**P26-0305** RAC Inc. Craig Engel (435) 229-7360 1267 N 1390 W St. George, UT 84770	**RAC Inc - Rodriguez Res** Rodriguez Residence Oak Valley Estates Lot 5 Kanarraville, UT Design: 05/27/26	**Approval**

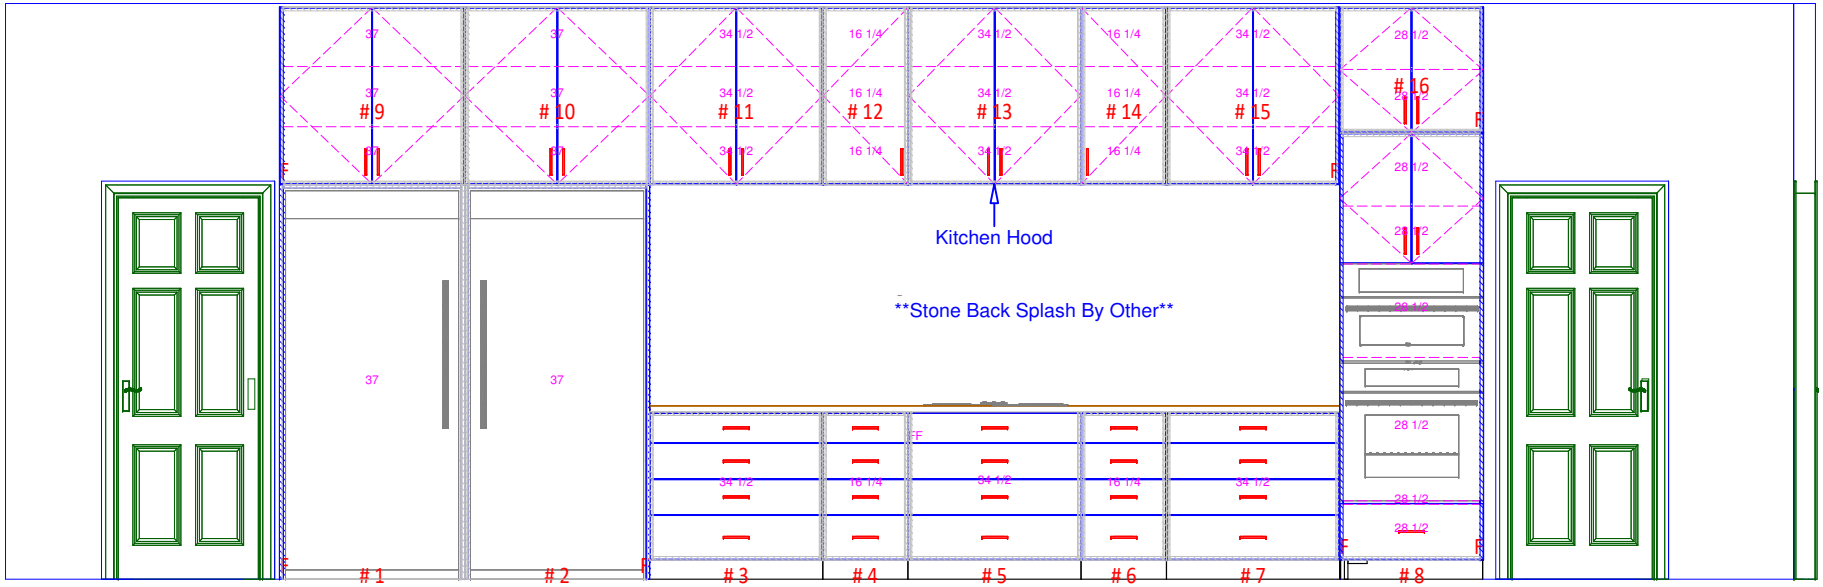

Wall 1
1 : 40

RM#1 - Kitchen Elev 1


CLOSET CREATIONS	**Closet Creations** 4058 S. River Road St. George, UT 84790 Phone: 435-656-5564 Fax:	**P26-0305** RAC Inc. Craig Engel (435) 229-7360 1267 N 1390 W St. George, UT 84770	**RAC Inc - Rodriguez Res** Rodriguez Residence Oak Valley Estates Lot 5 Kanarraville, UT Design: 05/27/26	**Approval**

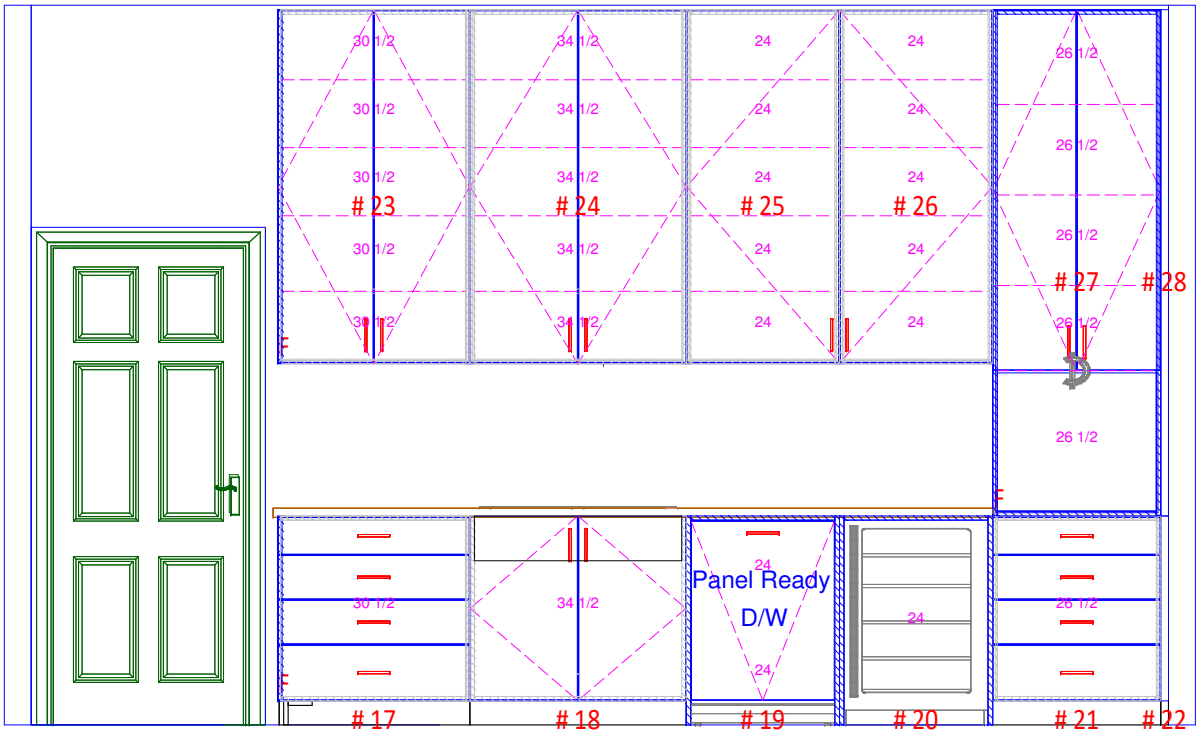

Wall 2
3/8 " = 1 '

RM#1 - Kitchen Elev 2

CLOSET CREATIONS	**Closet Creations** 4058 S. River Road St. George, UT 84790 Phone: 435-656-5564 Fax:	**P26-0305** RAC Inc. Craig Engel (435) 229-7360 1267 N 1390 W St. George, UT 84770	**RAC Inc - Rodriguez Res** Rodriguez Residence Oak Valley Estates Lot 5 Kanarraville, UT Design: 05/27/26	**Approval**

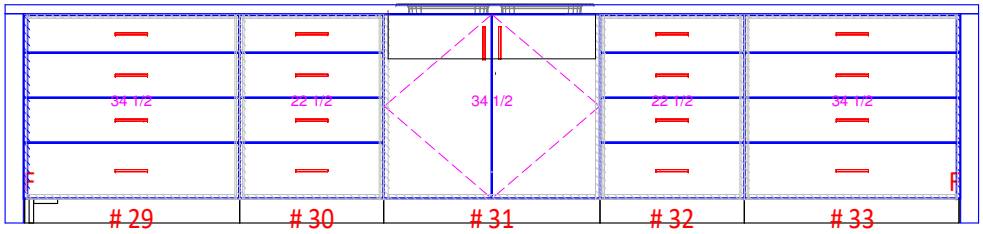

Wall 4
3/8" = 1'
RM#1 - Kitchen Elev 4


CLOSET CREATIONS	**Closet Creations** 4058 S. River Road St. George, UT 84790 Phone: 435-656-5564 Fax:	**P26-0305** RAC Inc. Craig Engel (435) 229-7360 1267 N 1390 W St. George, UT 84770	**RAC Inc - Rodriguez Res** Rodriguez Residence Oak Valley Estates Lot 5 Kanarraville, UT Design: 05/27/26	**Approval**




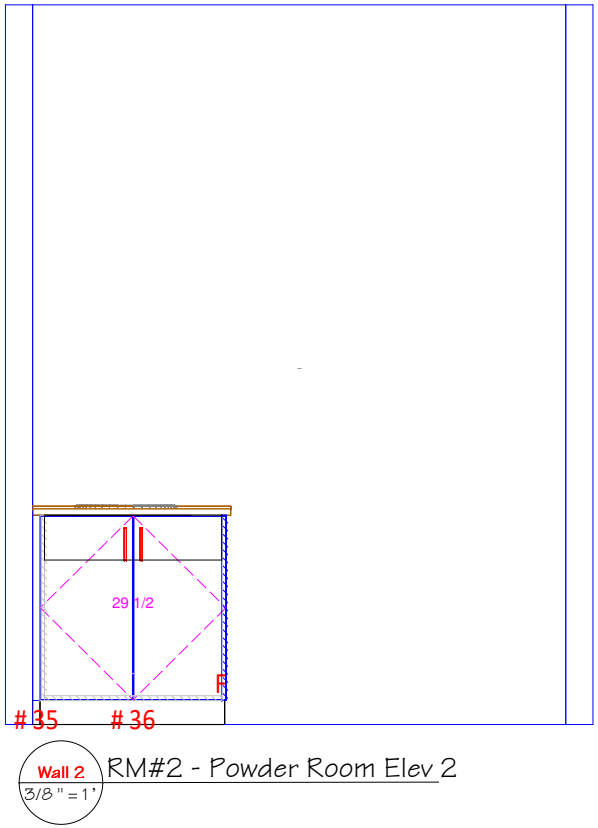


RM#2 - Powder Room Elev 2

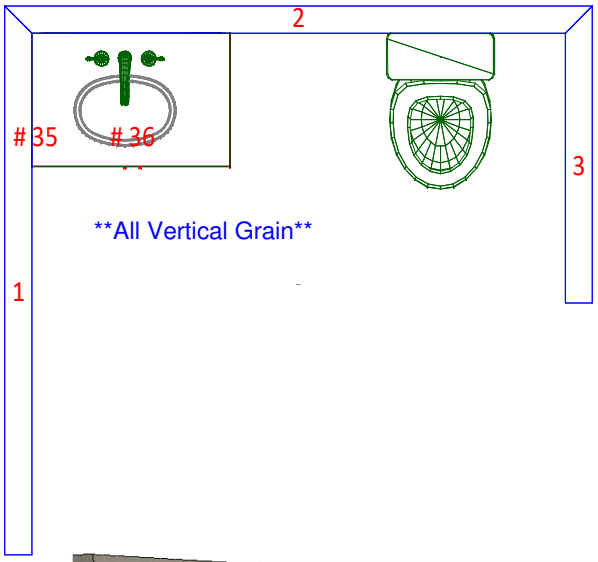

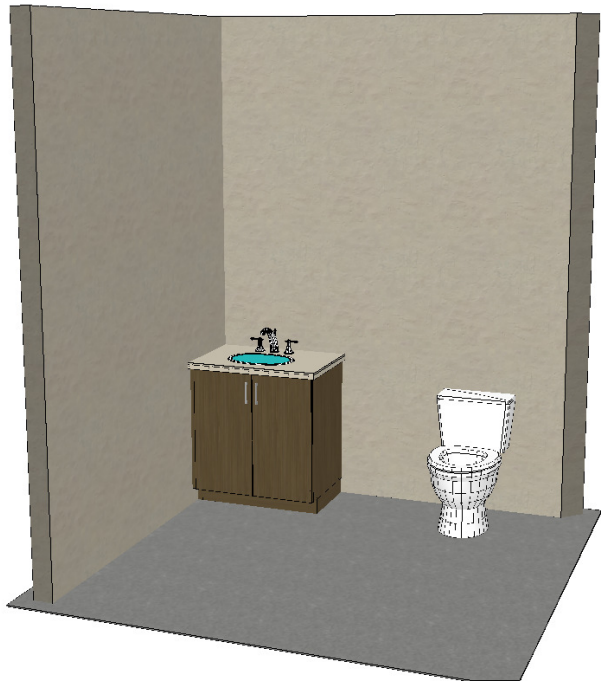


RM#2 - Powder Room	
Base Material:	Lochsa Rosewood 1mm, White Int.
Upper Material:	Lochsa Rosewood 1mm, White Int.
Construction:	Cabinets - Doweled
Drawer Box Style:	None
Door Specs	
Base Door Style:	Slab CC Door, Lochsa Rosewood 1mm
Upper Door Style:	Slab CC Door, Lochsa Rosewood 1mm
Drawer Front Style:	None, None
Countertop/Moulding	
Countertop:	Supplied By Others, Supplied By Other
Moulding:	None, Lochsa Rosewood 3/4
Hardware Specs	
Drawer Guide:	None
Hinges:	Soft Silentia 120 Degree Euro
Handles:	Metro SN (Stock) STUP822BSN-128

CLOSET CREATIONS	**Closet Creations** 4058 S. River Road St. George, UT 84790 Phone: 435-656-5564 Fax:	**P26-0305** RAC Inc. Craig Engel (435) 229-7360 1267 N 1390 W St. George, UT 84770	**RAC Inc - Rodriguez Res** Rodriguez Residence Oak Valley Estates Lot 5 Kanarraville, UT Design: 05/27/26	**Approval**

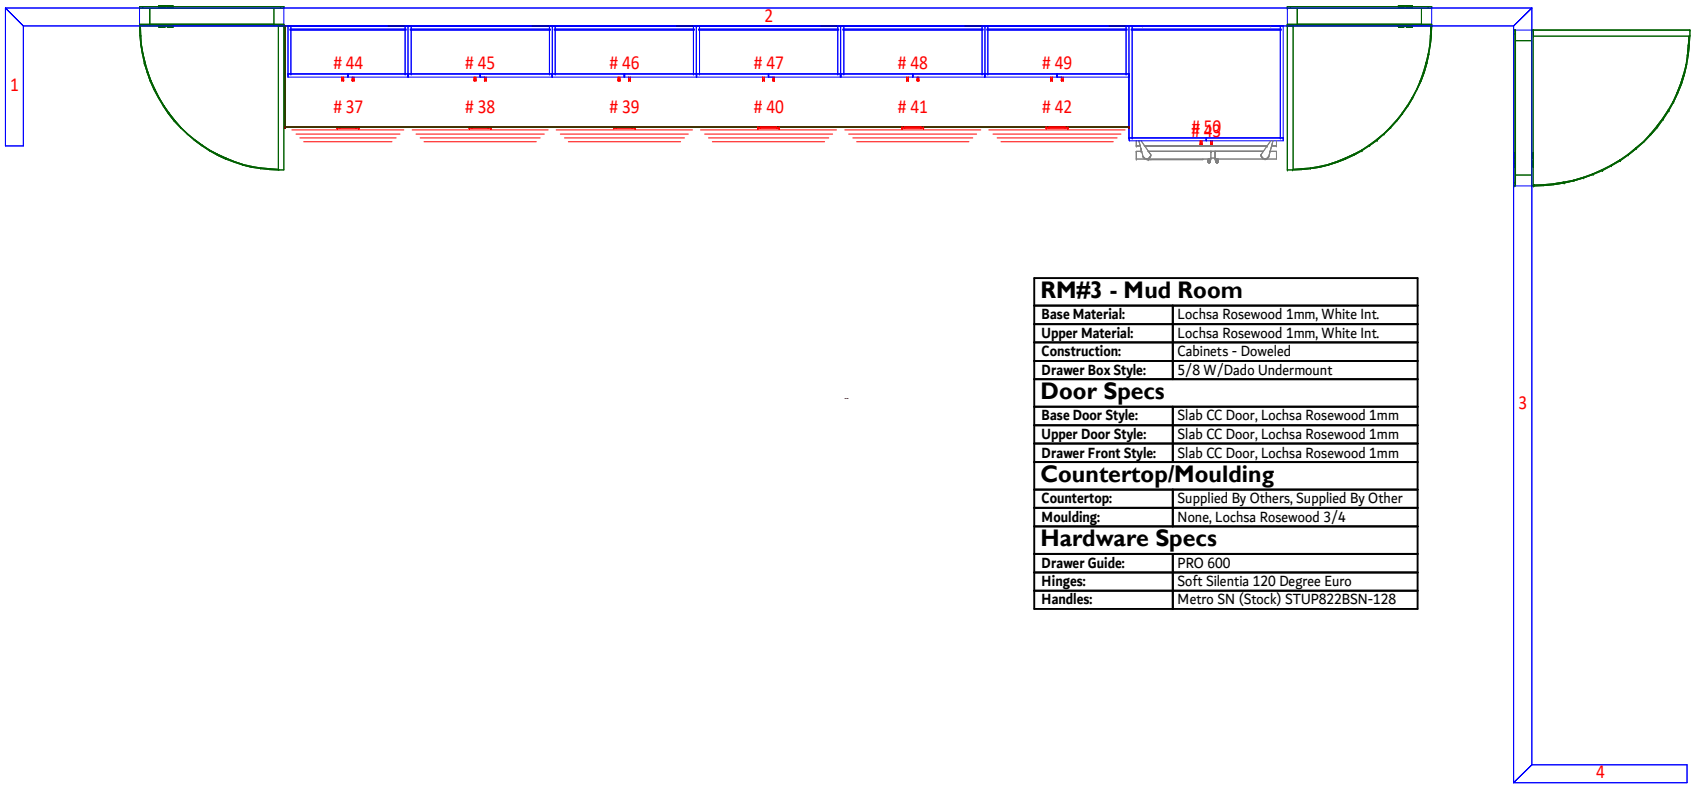


RM#3 - Mud Room	
Base Material:	Lochsa Rosewood 1mm, White Int.
Upper Material:	Lochsa Rosewood 1mm, White Int.
Construction:	Cabinets - Doweled
Drawer Box Style:	5/8 W/Dado Undermount
Door Specs	
Base Door Style:	Slab CC Door, Lochsa Rosewood 1mm
Upper Door Style:	Slab CC Door, Lochsa Rosewood 1mm
Drawer Front Style:	Slab CC Door, Lochsa Rosewood 1mm
Countertop/Moulding	
Countertop:	Supplied By Others, Supplied By Other
Moulding:	None, Lochsa Rosewood 3/4
Hardware Specs	
Drawer Guide:	PRO 600
Hinges:	Soft Silentia 120 Degree Euro
Handles:	Metro SN (Stock) STUP822BSN-128


CLOSET CREATIONS	**Closet Creations** 4058 S. River Road St. George, UT 84790 Phone: 435-656-5564 Fax:	**P26-0305** RAC Inc. Craig Engel (435) 229-7360 1267 N 1390 W St. George, UT 84770	**RAC Inc - Rodriguez Res** Rodriguez Residence Oak Valley Estates Lot 5 Kanarraville, UT Design: 05/27/26	**Approval**

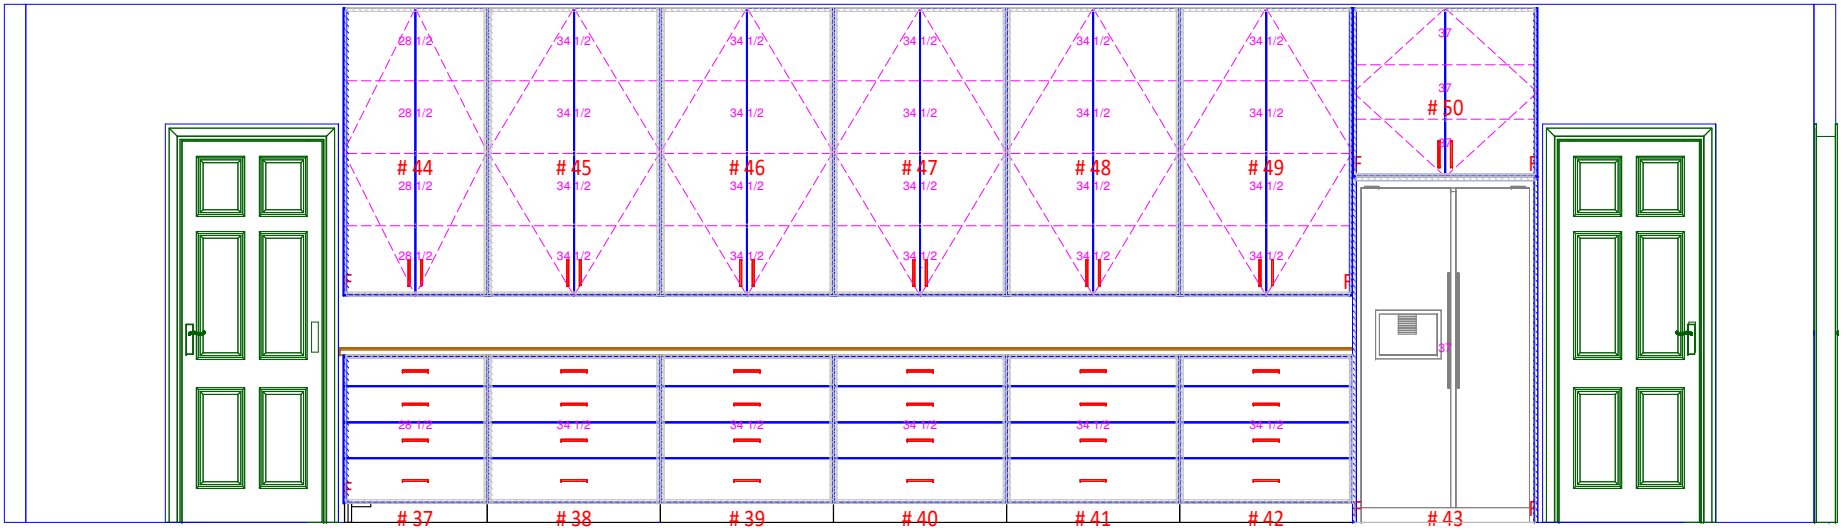

Wall 2
1 : 40
RM#3 - Mud Room Elev 2

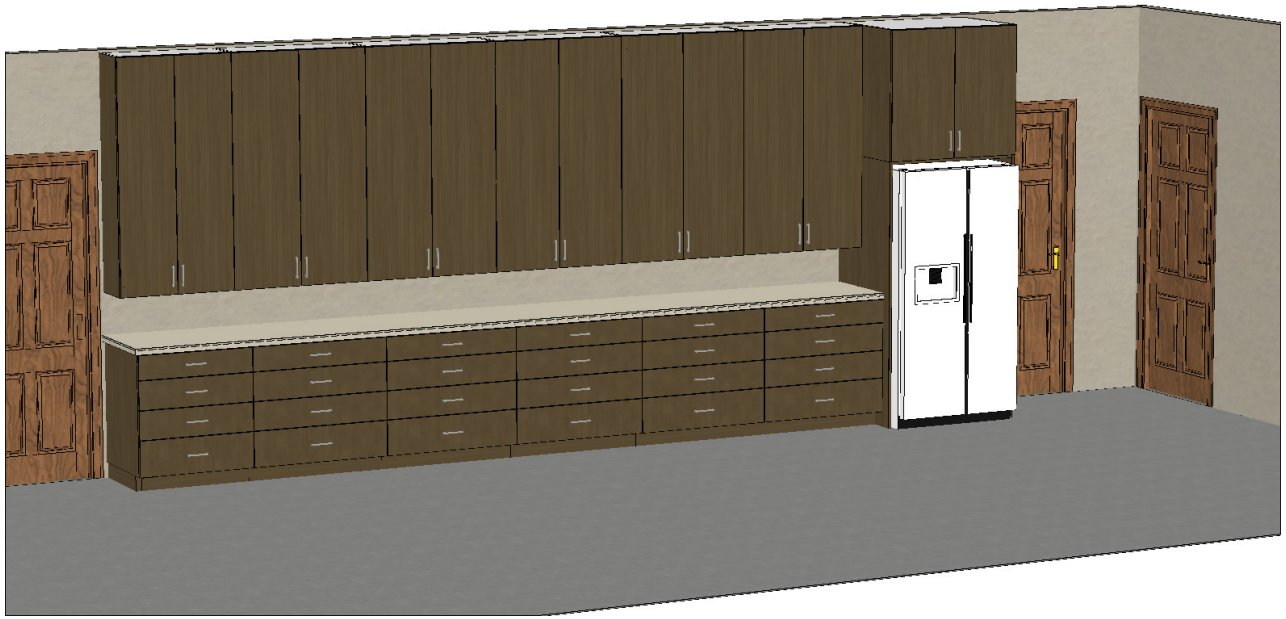


CLOSET CREATIONS	**Closet Creations** 4058 S. River Road St. George, UT 84790 Phone: 435-656-5564 Fax:	**P26-0305** RAC Inc. Craig Engel (435) 229-7360 1267 N 1390 W St. George, UT 84770	**RAC Inc - Rodriguez Res** Rodriguez Residence Oak Valley Estates Lot 5 Kanarraville, UT Design: 05/27/26	**Approval**

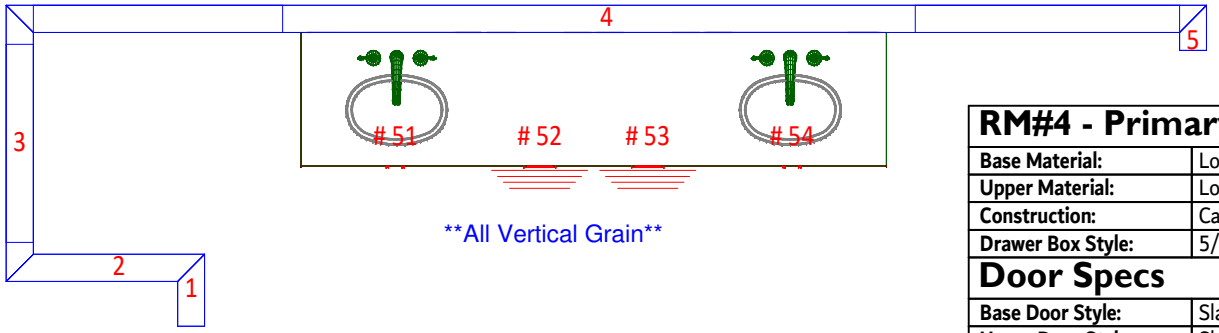

RM#4 - Primary Bath	
Base Material:	Lochsa Rosewood 1mm, White Int.
Upper Material:	Lochsa Rosewood 1mm, White Int.
Construction:	Cabinets - Doweled
Drawer Box Style:	5/8 W/Dado Undermount
Door Specs	
Base Door Style:	Slab CC Door, Lochsa Rosewood 1mm
Upper Door Style:	Slab CC Door, Lochsa Rosewood 1mm
Drawer Front Style:	Slab CC Door, Lochsa Rosewood 1mm
Countertop/Moulding	
Countertop:	Supplied By Others, Supplied By Other
Moulding:	None, Lochsa Rosewood 3/4
Hardware Specs	
Drawer Guide:	PRO 600
Hinges:	Soft Silentia 120 Degree Euro
Handles:	Metro SN (Stock) STUP822BSN-128




CLOSET CREATIONS	**Closet Creations** 4058 S. River Road St. George, UT 84790 Phone: 435-656-5564 Fax:	**P26-0305** RAC Inc. Craig Engel (435) 229-7360 1267 N 1390 W St. George, UT 84770	**RAC Inc - Rodriguez Res** Rodriguez Residence Oak Valley Estates Lot 5 Kanarraville, UT Design: 05/27/26	**Approval**

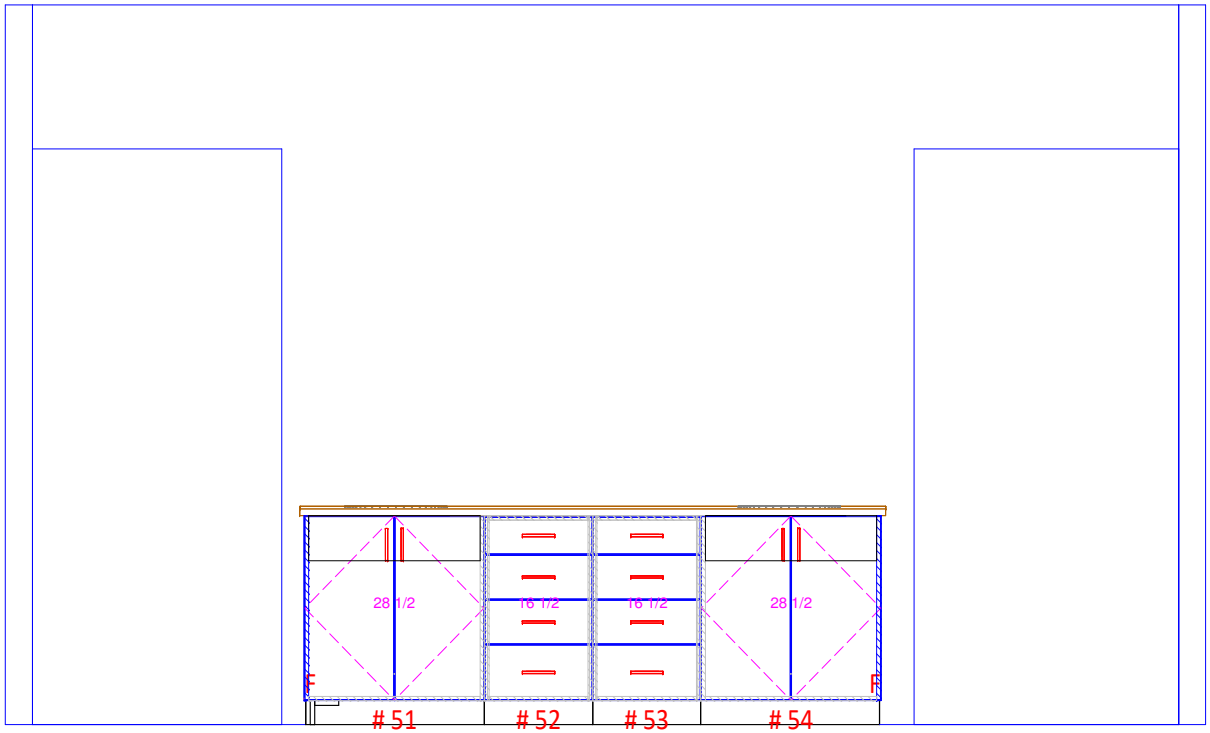

Wall 4
3/8" = 1'


RM#4 - Primary Bath Elev 4

CLOSET CREATIONS	**Closet Creations** 4058 S. River Road St. George, UT 84790 Phone: 435-656-5564 Fax:	**P26-0305** RAC Inc. Craig Engel (435) 229-7360 1267 N 1390 W St. George, UT 84770	**RAC Inc - Rodriguez Res** Rodriguez Residence Oak Valley Estates Lot 5 Kanarraville, UT Design: 05/27/26	**Approval**

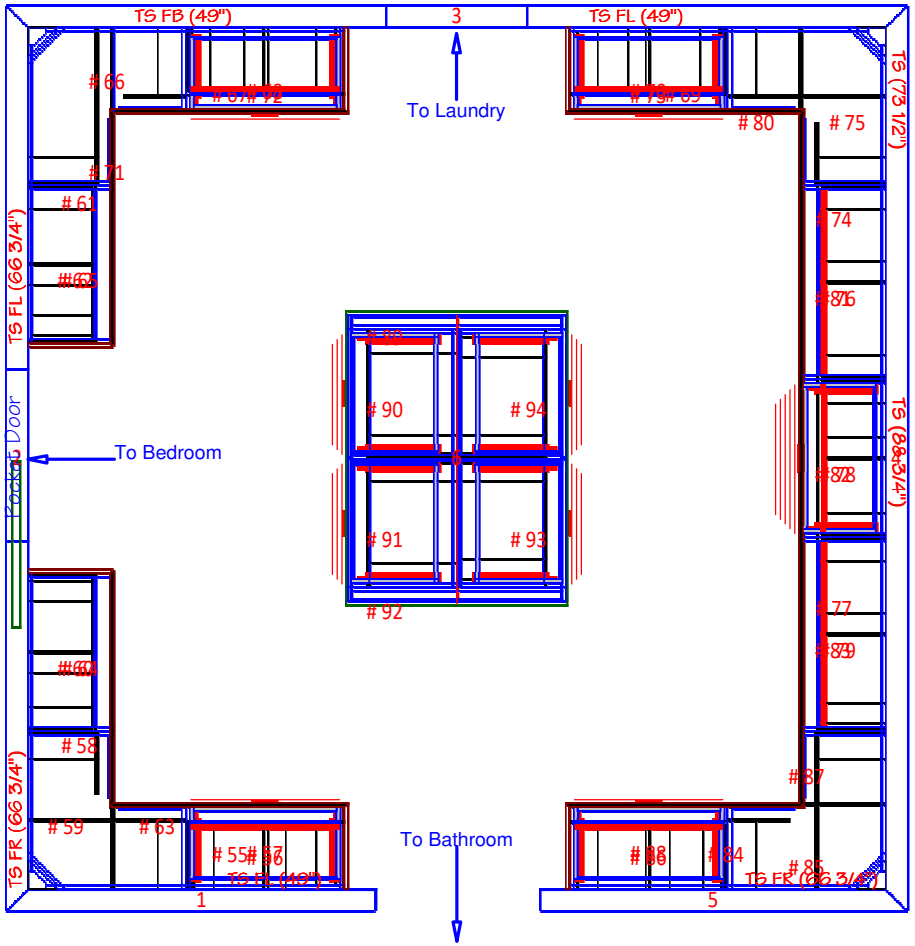


RM#5 - Primary Closet	
Material:	Lochsa Rosewood 1mm
Construction:	Doweled Closet w/ Backs
Drawer Box Style:	5/8 W/Dado Undermount
Door Specs	
Base Door Style:	Slab CC Door, Lochsa Rosewood 1mm
Upper Door Style:	Slab CC Door, Lochsa Rosewood 1mm
Drawer Front Style:	Slab CC Door, Lochsa Rosewood 1mm
Countertop/Moulding	
Countertop:	Supplied By Others, Supplied By Other
Moulding:	Sub Trim 3, Lochsa Rosewood 3/4
Hardware Specs	
Closet Rods:	Chrome Closet Rods Oval
Drawer Guide:	PRO 600
Hinges:	Soft Silentia 120 Degree Euro
Handles:	Metro SN (Stock) STUP822BSN-128

CLOSET CREATIONS	**Closet Creations** 4058 S. River Road St. George, UT 84790 Phone: 435-656-5564 Fax:	**P26-0305** RAC Inc. Craig Engel (435) 229-7360 1267 N 1390 W St. George, UT 84770	**RAC Inc - Rodriguez Res** Rodriguez Residence Oak Valley Estates Lot 5 Kanarraville, UT Design: 05/27/26	**Approval**

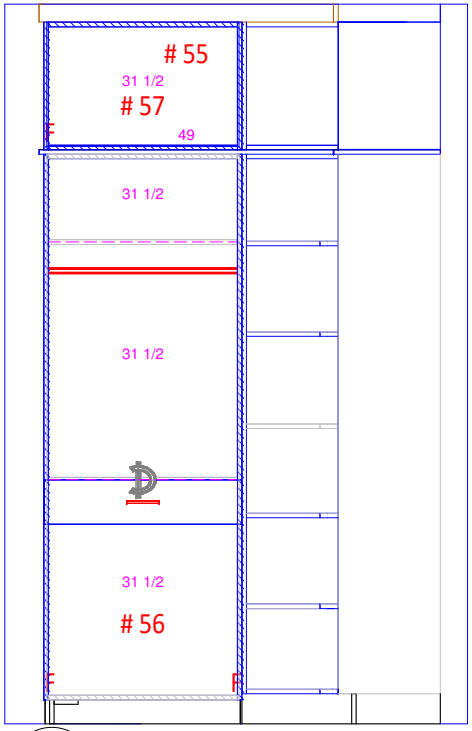


Wall 1
3/8" = 1'
RM#5 - Primary Closet Elev 1

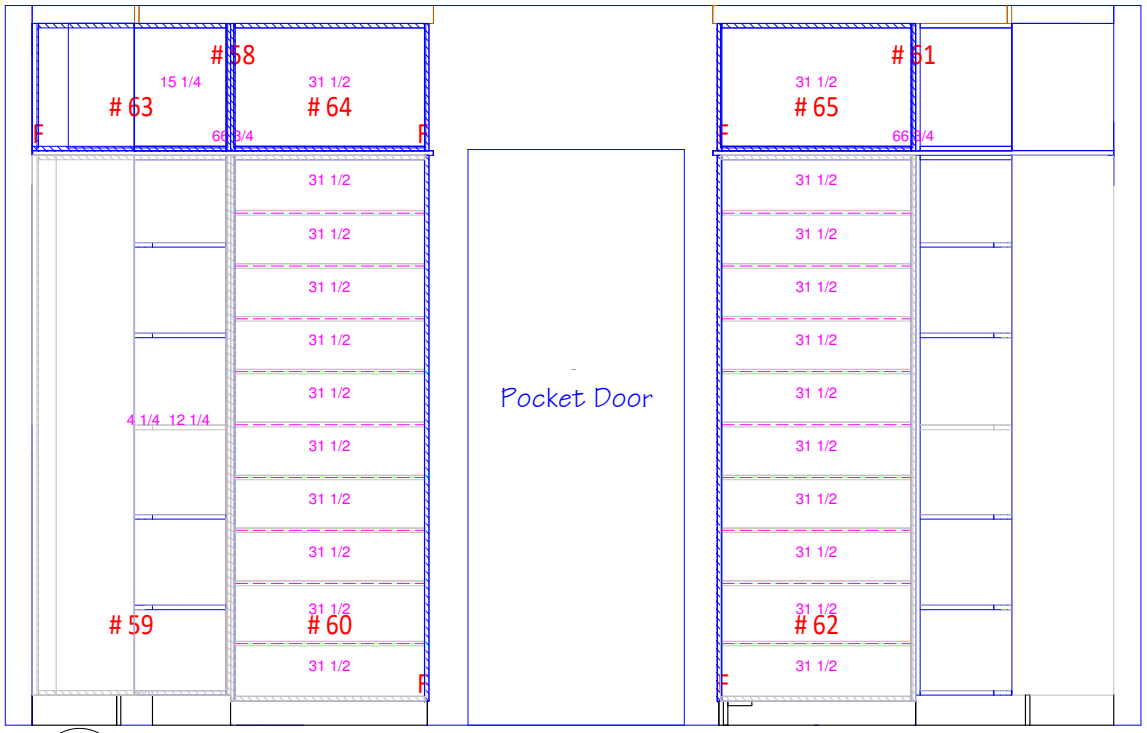


Wall 2
3/8" = 1'
RM#5 - Primary Closet Elev 2

CLOSET CREATIONS	**Closet Creations** 4058 S. River Road St. George, UT 84790 Phone: 435-656-5564 Fax:	**P26-0305** RAC Inc. Craig Engel (435) 229-7360 1267 N 1390 W St. George, UT 84770	**RAC Inc - Rodriguez Res** Rodriguez Residence Oak Valley Estates Lot 5 Kanarraville, UT Design: 05/27/26	**Approval**

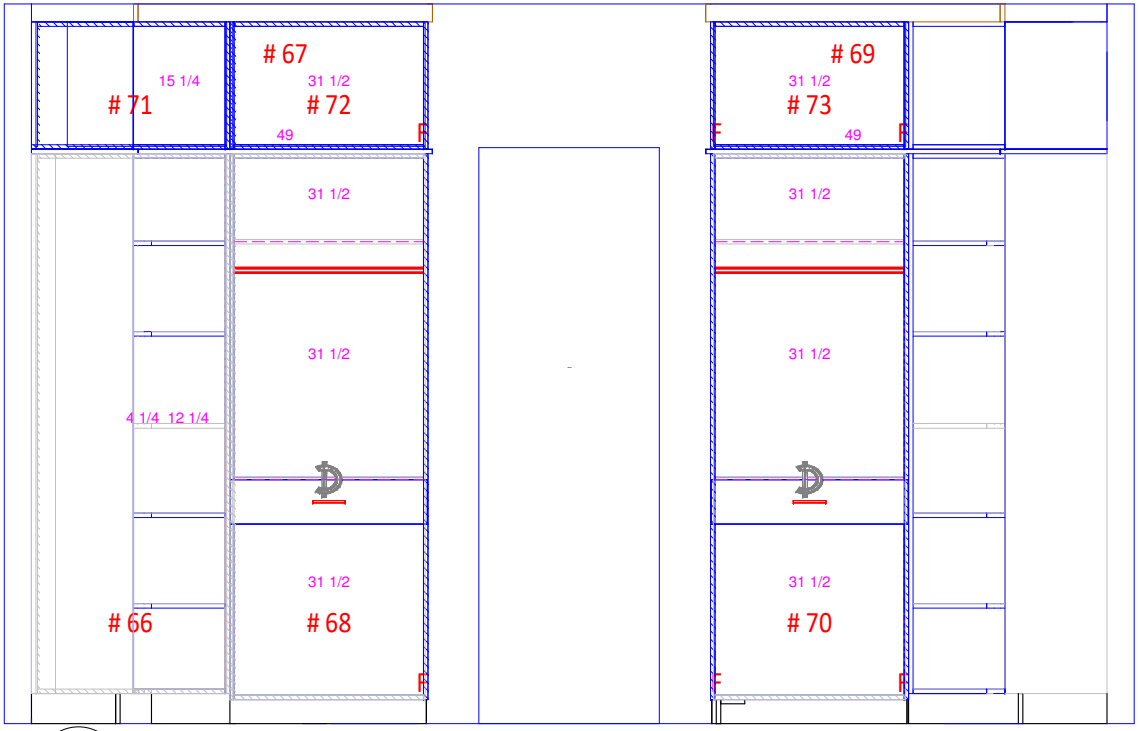


Wall 3
3/8" = 1'
RM#5 - Primary Closet Elev 3

CLOSET CREATIONS	**Closet Creations** 4058 S. River Road St. George, UT 84790 Phone: 435-656-5564 Fax:	**P26-0305** RAC Inc. Craig Engel (435) 229-7360 1267 N 1390 W St. George, UT 84770	**RAC Inc - Rodriguez Res** Rodriguez Residence Oak Valley Estates Lot 5 Kanarraville, UT Design: 05/27/26	**Approval**

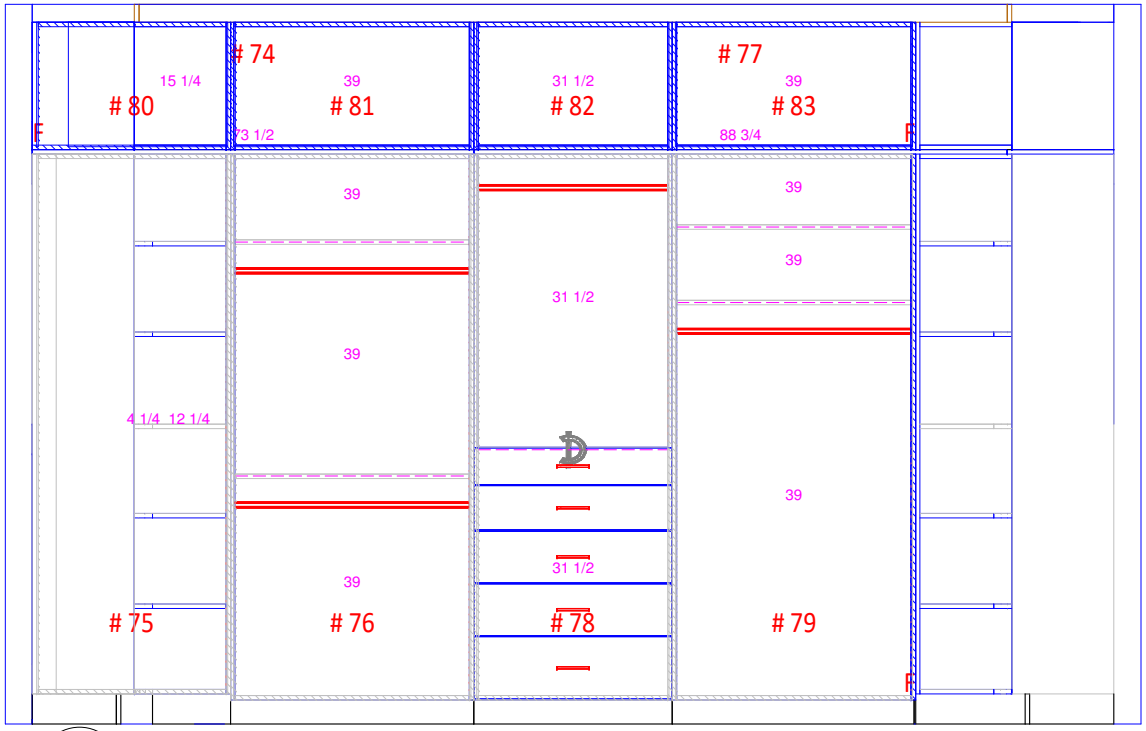

Wall 4 — RM#5 - Primary Closet Elev 4


3/8 " = 1 '

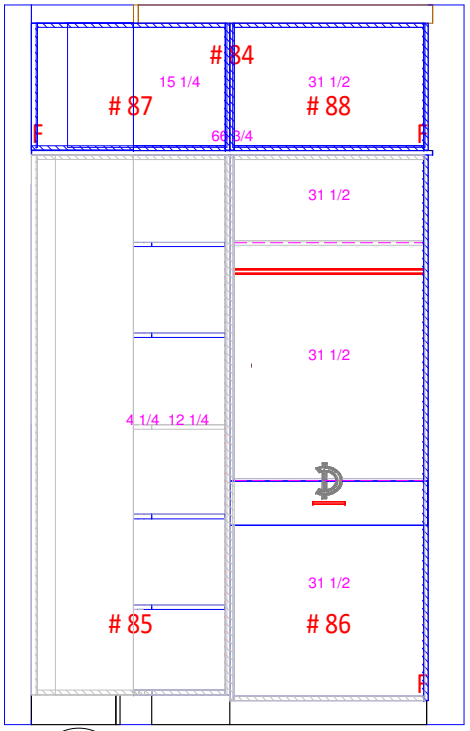



Wall 5 — RM#5 - Primary Closet Elev 5

3/8 " = 1 '

CLOSET CREATIONS	**Closet Creations** 4058 S. River Road St. George, UT 84790 Phone: 435-656-5564 Fax:	**P26-0305** RAC Inc. Craig Engel (435) 229-7360 1267 N 1390 W St. George, UT 84770	**RAC Inc - Rodriguez Res** Rodriguez Residence Oak Valley Estates Lot 5 Kanarraville, UT Design: 05/27/26	**Approval**

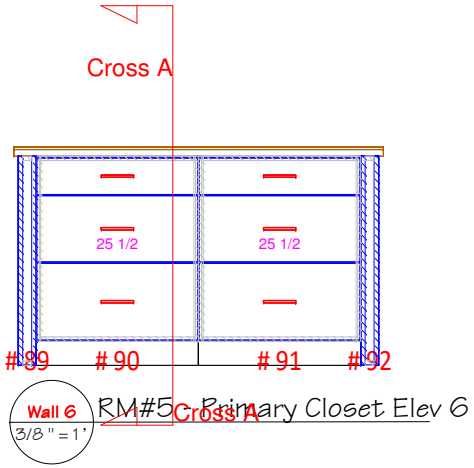

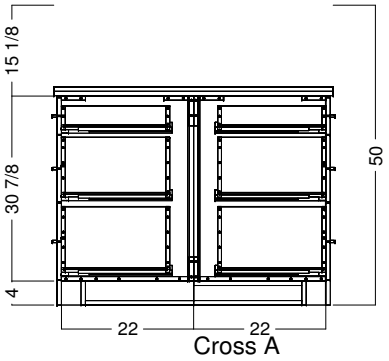

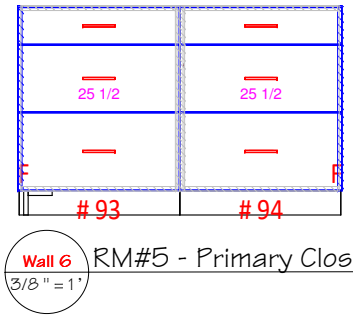


CLOSET CREATIONS	**Closet Creations** 4058 S. River Road St. George, UT 84790 Phone: 435-656-5564 Fax:	**P26-0305** RAC Inc. Craig Engel (435) 229-7360 1267 N 1390 W St. George, UT 84770	**RAC Inc - Rodriguez Res** Rodriguez Residence Oak Valley Estates Lot 5 Kanarraville, UT Design: 05/27/26	**Approval**



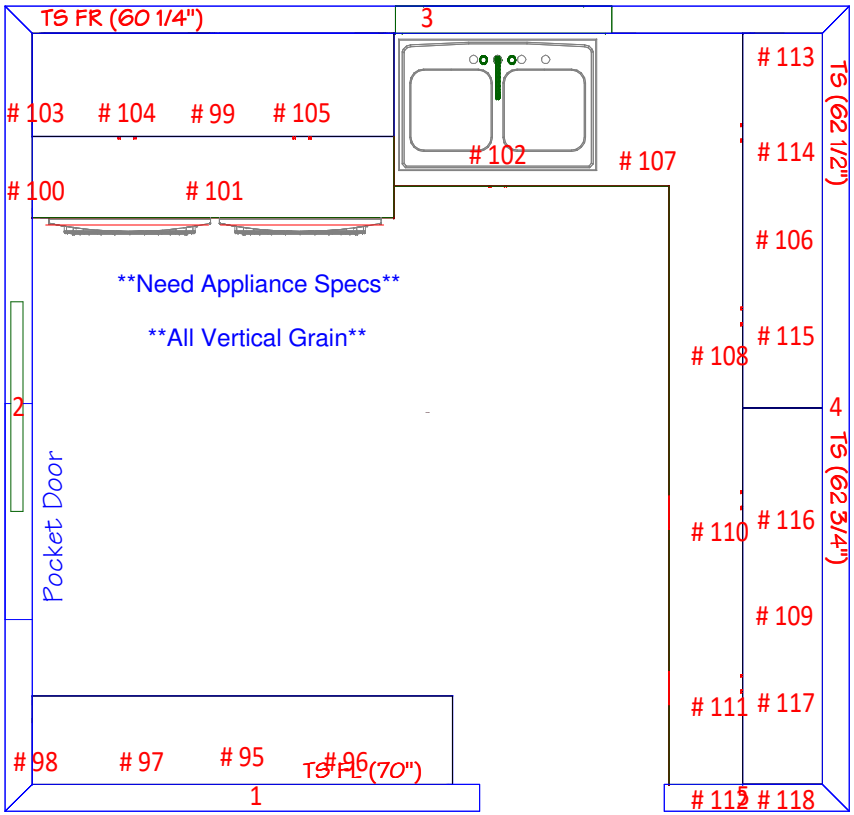


RM#6 - Laundry	
Base Material:	Lochsa Rosewood 1mm, White Int.
Upper Material:	Lochsa Rosewood 1mm, White Int.
Construction:	Cabinets - Doweled
Drawer Box Style:	5/8 W/Dado Undermount
Door Specs	
Base Door Style:	Slab CC Door, Lochsa Rosewood 1mm
Upper Door Style:	Slab CC Door, Lochsa Rosewood 1mm
Drawer Front Style:	Slab CC Door, Lochsa Rosewood 1mm
Countertop/Moulding	
Countertop:	Supplied By Others, Supplied By Other
Moulding:	None, Lochsa Rosewood 3/4
Hardware Specs	
Drawer Guide:	PRO 600
Hinges:	Soft Silentia 120 Degree Euro
Handles:	Metro SN (Stock) STUP822BSN-128

Accessories:
3 Wire Hamper Kits

CLOSET CREATIONS	**Closet Creations** 4058 S. River Road St. George, UT 84790 Phone: 435-656-5564 Fax:	**P26-0305** RAC Inc. Craig Engel (435) 229-7360 1267 N 1390 W St. George, UT 84770	**RAC Inc - Rodriguez Res** Rodriguez Residence Oak Valley Estates Lot 5 Kanarraville, UT Design: 05/27/26	**Approval**

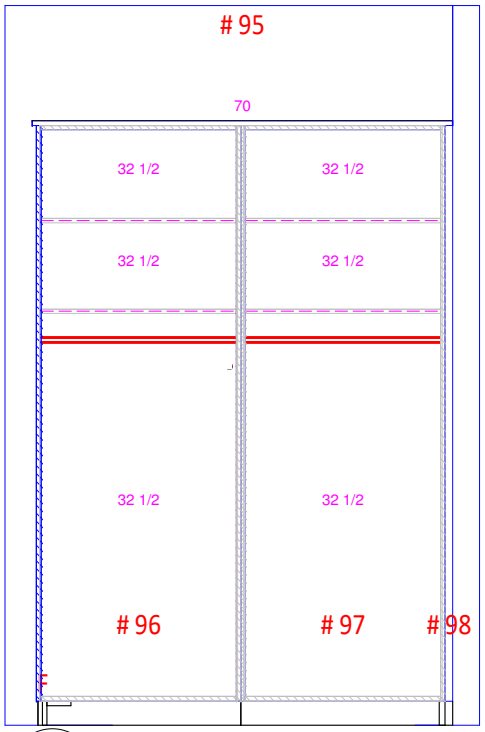


Wall 1
3/8" = 1'
RM#6 - Laundry Elev 1

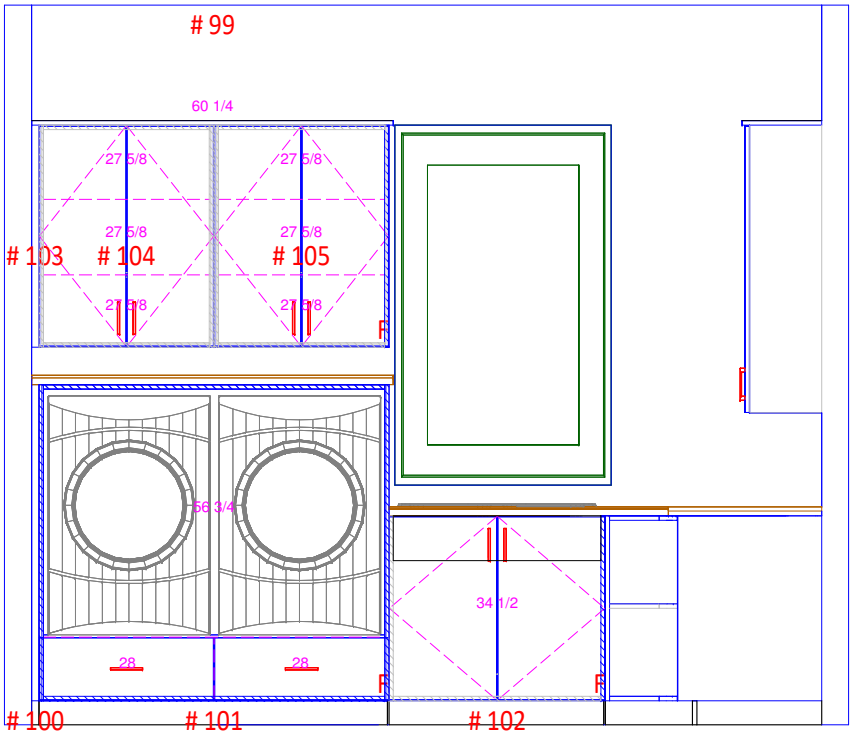

Wall 3
3/8" = 1'
RM#6 - Laundry Elev 3

CLOSET CREATIONS	**Closet Creations** 4058 S. River Road St. George, UT 84790 Phone: 435-656-5564 Fax:	**P26-0305** RAC Inc. Craig Engel (435) 229-7360 1267 N 1390 W St. George, UT 84770	**RAC Inc - Rodriguez Res** Rodriguez Residence Oak Valley Estates Lot 5 Kanarraville, UT Design: 05/27/26	**Approval**

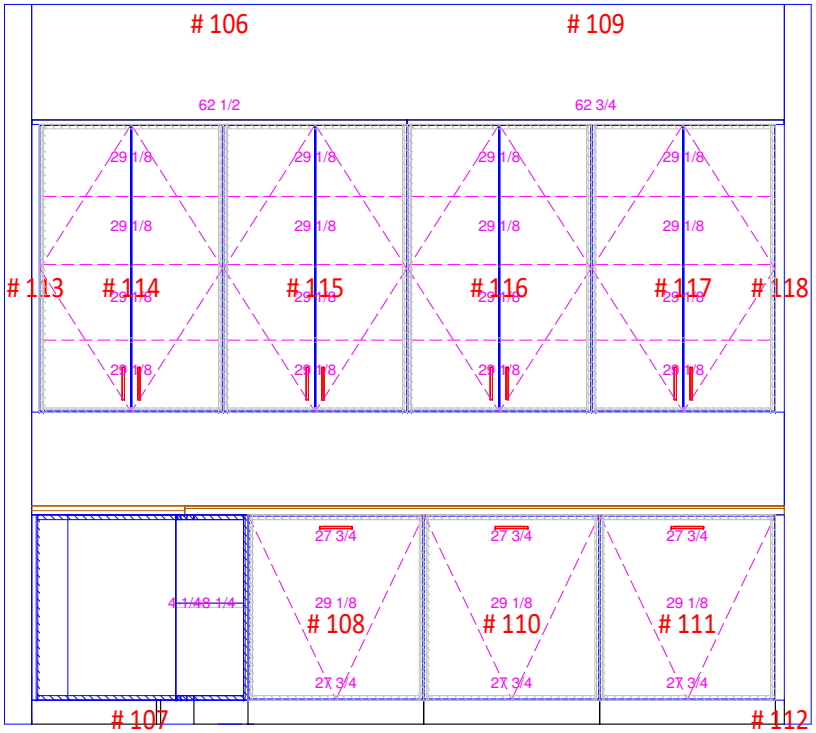


CLOSET CREATIONS	**Closet Creations** 4058 S. River Road St. George, UT 84790 Phone: 435-656-5564 Fax:	**P26-0305** RAC Inc. Craig Engel (435) 229-7360 1267 N 1390 W St. George, UT 84770	**RAC Inc - Rodriguez Res** Rodriguez Residence Oak Valley Estates Lot 5 Kanarraville, UT Design: 05/27/26	**Approval**





CLOSET CREATIONS	**Closet Creations** 4058 S. River Road St. George, UT 84790 Phone: 435-656-5564 Fax:	**P26-0305** RAC Inc. Craig Engel (435) 229-7360 1267 N 1390 W St. George, UT 84770	**RAC Inc - Rodriguez Res** Rodriguez Residence Oak Valley Estates Lot 5 Kanarraville, UT Design: 05/27/26	**Approval**

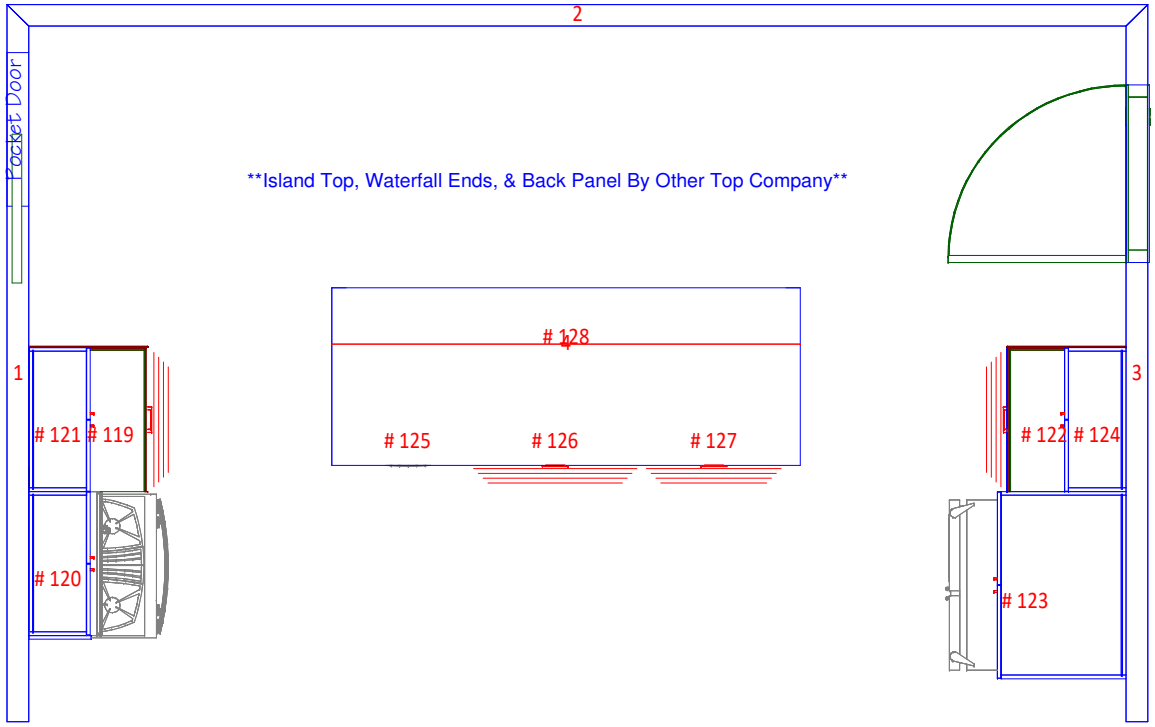

RM#7 - Casita Kitchen	
Base Material:	Lochsa Rosewood 1mm, White Int.
Upper Material:	Lochsa Rosewood 1mm, White Int.
Construction:	Cabinets - Doweled
Drawer Box Style:	5/8 W/Dado Undermount
Door Specs	
Base Door Style:	Slab CC Door, Lochsa Rosewood 1mm
Upper Door Style:	Slab CC Door, Lochsa Rosewood 1mm
Drawer Front Style:	Slab CC Door, Lochsa Rosewood 1mm
Countertop/Moulding	
Countertop:	Supplied By Others, Granite
Moulding:	None, Lochsa Rosewood 3/4
Hardware Specs	
Drawer Guide:	PRO 600
Hinges:	Soft Silentia 120 Degree Euro
Handles:	Metro SN (Stock) STUP822BSN-128

CLOSET CREATIONS


Closet Creations
4058 S. River Road
St. George, UT 84790

Phone: 435-656-5564
Fax:


P26-0305
RAC Inc.
Craig Engel
(435) 229-7360
1267 N 1390 W
St. George, UT 84770

RAC Inc - Rodriguez Res
Rodriguez Residence
Oak Valley Estates Lot 5
Kanarraville, UT
Design:
05/27/26

Approval

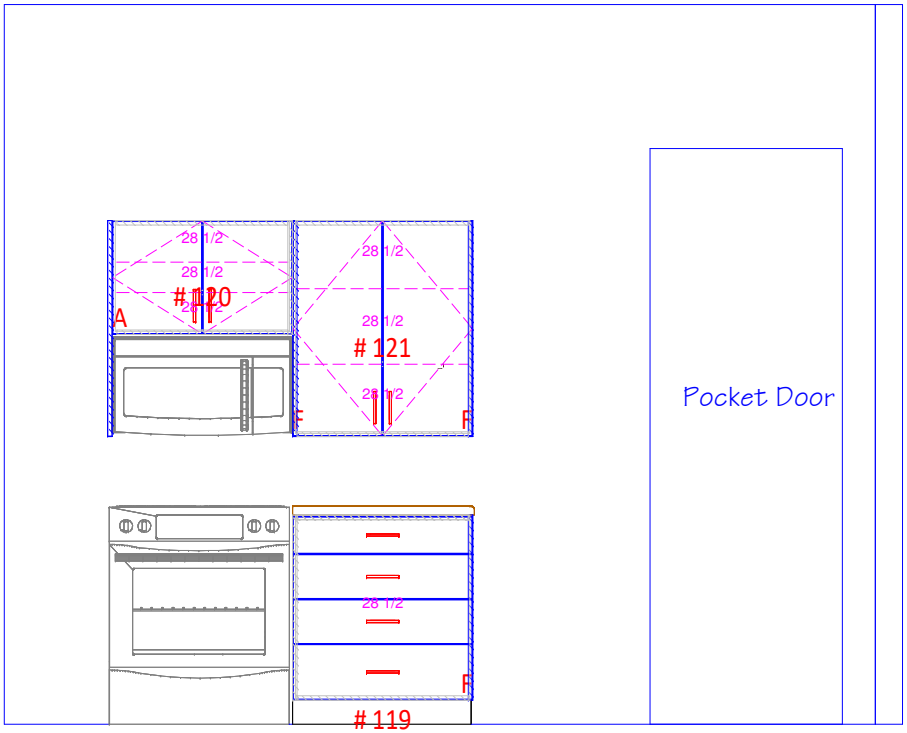

Wall 1
3/8" = 1'
RM#7 - Casita Kitchen Elev 1

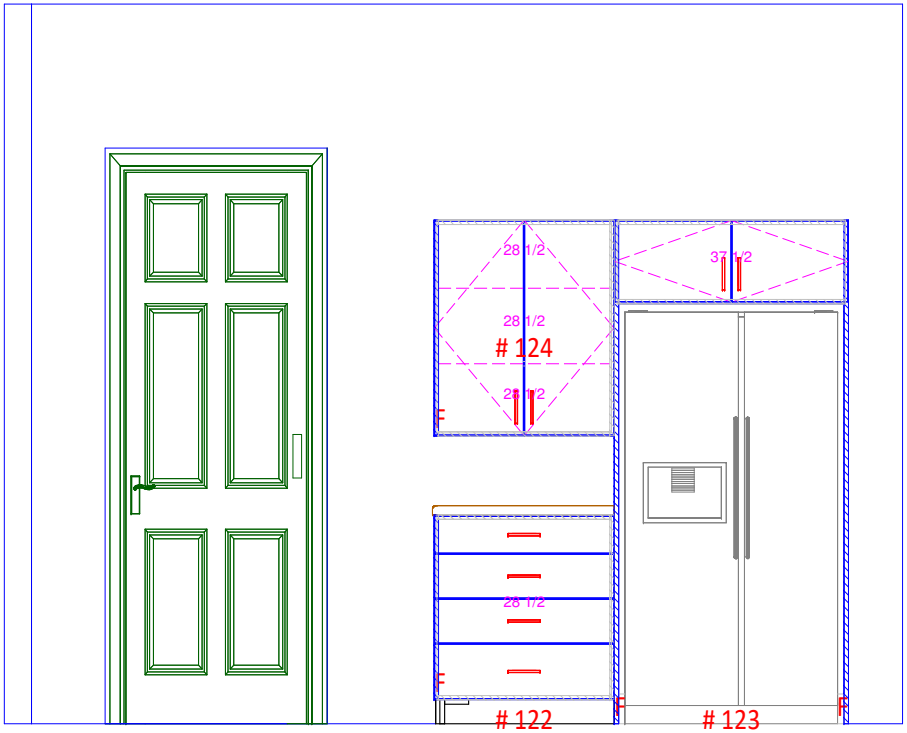


Wall 3
3/8" = 1'
RM#7 - Casita Kitchen Elev 3

CLOSET CREATIONS	**Closet Creations** 4058 S. River Road St. George, UT 84790 Phone: 435-656-5564 Fax:	**P26-0305** RAC Inc. Craig Engel (435) 229-7360 1267 N 1390 W St. George, UT 84770	**RAC Inc - Rodriguez Res** Rodriguez Residence Oak Valley Estates Lot 5 Kanarraville, UT Design: 05/27/26	**Approval**



Island Top, Waterfall Ends, & Back Panel By Other Top Company

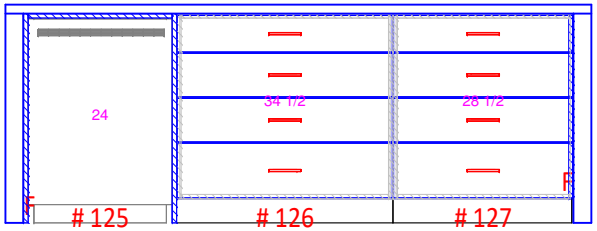


Wall 4
3/8" = 1'


RM#7 - Casita Kitchen Elev 4



CLOSET CREATIONS	**Closet Creations** 4058 S. River Road St. George, UT 84790 Phone: 435-656-5564 Fax:	**P26-0305** RAC Inc. Craig Engel (435) 229-7360 1267 N 1390 W St. George, UT 84770	**RAC Inc - Rodriguez Res** Rodriguez Residence Oak Valley Estates Lot 5 Kanarraville, UT Design: 05/27/26	**Approval**

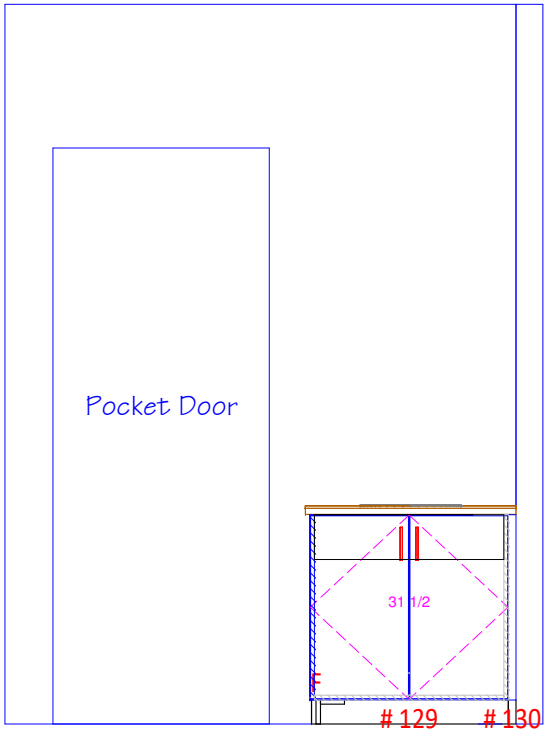

Wall 1
3/8 " = 1 '
RM#8 - Casita Bath Elev 1

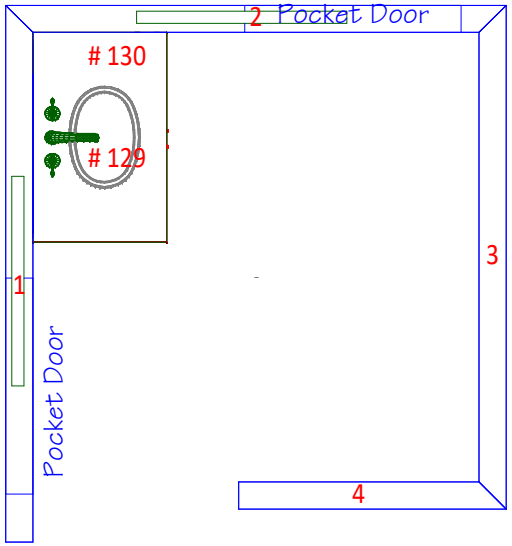

RM#8 - Casita Bath	
Base Material:	Lochsa Rosewood 1mm, White Int.
Upper Material:	Lochsa Rosewood 1mm, White Int.
Construction:	Cabinets - Doweled
Drawer Box Style:	None
Door Specs	
Base Door Style:	Slab CC Door, Lochsa Rosewood 1mm
Upper Door Style:	Slab CC Door, Lochsa Rosewood 1mm
Drawer Front Style:	None, None
Countertop/Moulding	
Countertop:	Supplied By Others, Supplied By Other
Moulding:	None, Lochsa Rosewood 3/4
Hardware Specs	
Drawer Guide:	PRO 600
Hinges:	Soft Silentia 120 Degree Euro
Handles:	Metro SN (Stock) STUP822BSN-128



CLOSET CREATIONS


Closet Creations
4058 S. River Road
St. George, UT 84790

Phone: 435-656-5564
Fax:


P26-0305
RAC Inc.
Craig Engel
(435) 229-7360
1267 N 1390 W
St. George, UT 84770

RAC Inc - Rodriguez Res
Rodriguez Residence
Oak Valley Estates Lot 5
Kanarraville, UT
Design:
05/27/26

Approval

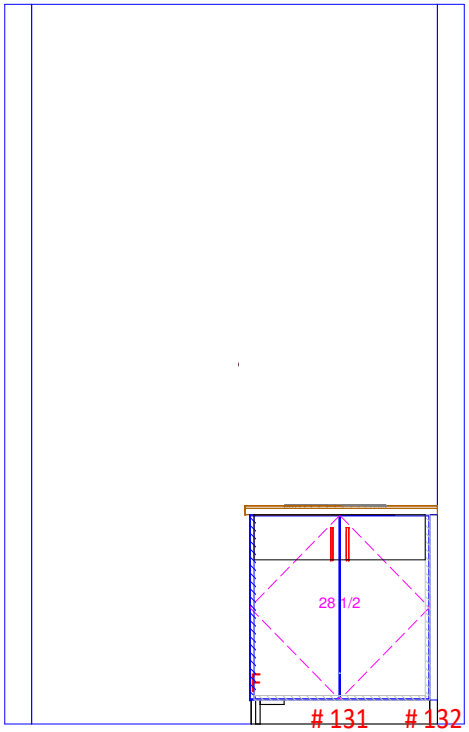


Wall 4
3/8 " = 1 '
RM#9 - Basement Powder Elev 4

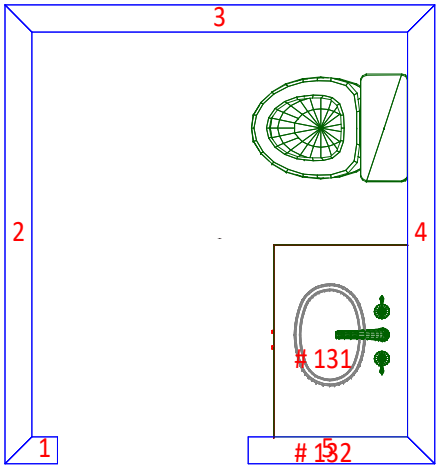




RM#9 - Basement Powder	
Base Material:	Lochsa Rosewood 1mm, White Int.
Upper Material:	Lochsa Rosewood 1mm, White Int.
Construction:	Cabinets - Doweled
Drawer Box Style:	None
Door Specs	
Base Door Style:	Slab CC Door, Lochsa Rosewood 1mm
Upper Door Style:	Slab CC Door, Lochsa Rosewood 1mm
Drawer Front Style:	None, None
Countertop/Moulding	
Countertop:	Supplied By Others, Supplied By Other
Moulding:	None, Lochsa Rosewood 3/4
Hardware Specs	
Drawer Guide:	None
Hinges:	Soft Silentia 120 Degree Euro
Handles:	Metro SN (Stock) STUP822BSN-128

CLOSET CREATIONS	**Closet Creations** 4058 S. River Road St. George, UT 84790 Phone: 435-656-5564 Fax:	**P26-0305** RAC Inc. Craig Engel (435) 229-7360 1267 N 1390 W St. George, UT 84770	**RAC Inc - Rodriguez Res** Rodriguez Residence Oak Valley Estates Lot 5 Kanarraville, UT Design: 05/27/26	**Approval**

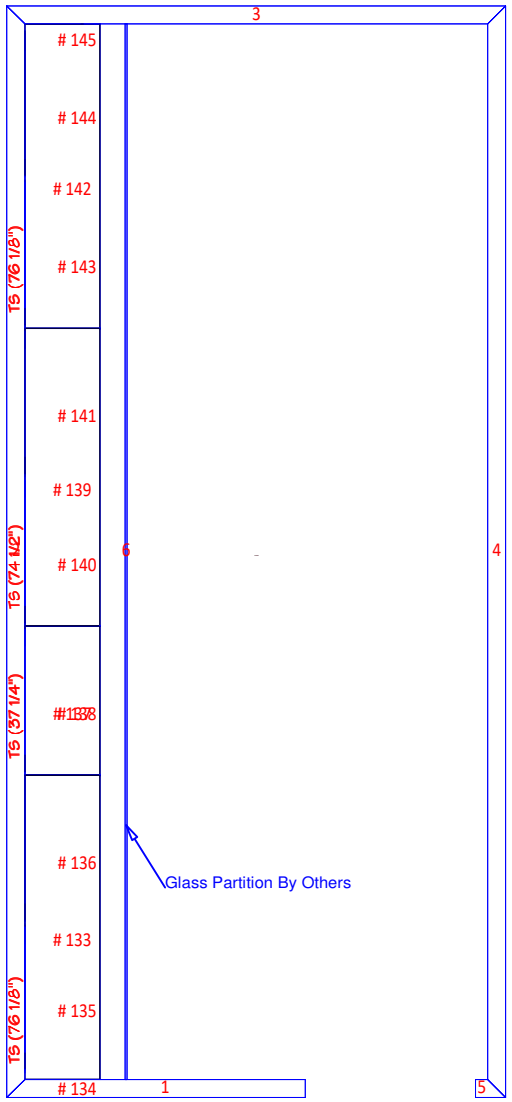

RM#10 - Vault	
Base Material:	Lochsa Rosewood 1mm, White Int.
Upper Material:	Lochsa Rosewood 1mm, White Int.
Construction:	Cabinets - Doweled
Drawer Box Style:	5/8 W/Dado Undermount
Door Specs	
Base Door Style:	Slab CC Door, Lochsa Rosewood 1mm
Upper Door Style:	Slab CC Door, Lochsa Rosewood 1mm
Drawer Front Style:	Slab CC Door, Lochsa Rosewood 1mm
Countertop/Moulding	
Countertop:	Supplied By Others, Supplied By Other
Moulding:	None, Lochsa Rosewood 3/4
Hardware Specs	
Drawer Guide:	PRO 600
Hinges:	Soft Silentia 120 Degree Euro
Handles:	Metro SN (Stock) STUP822BSN-128

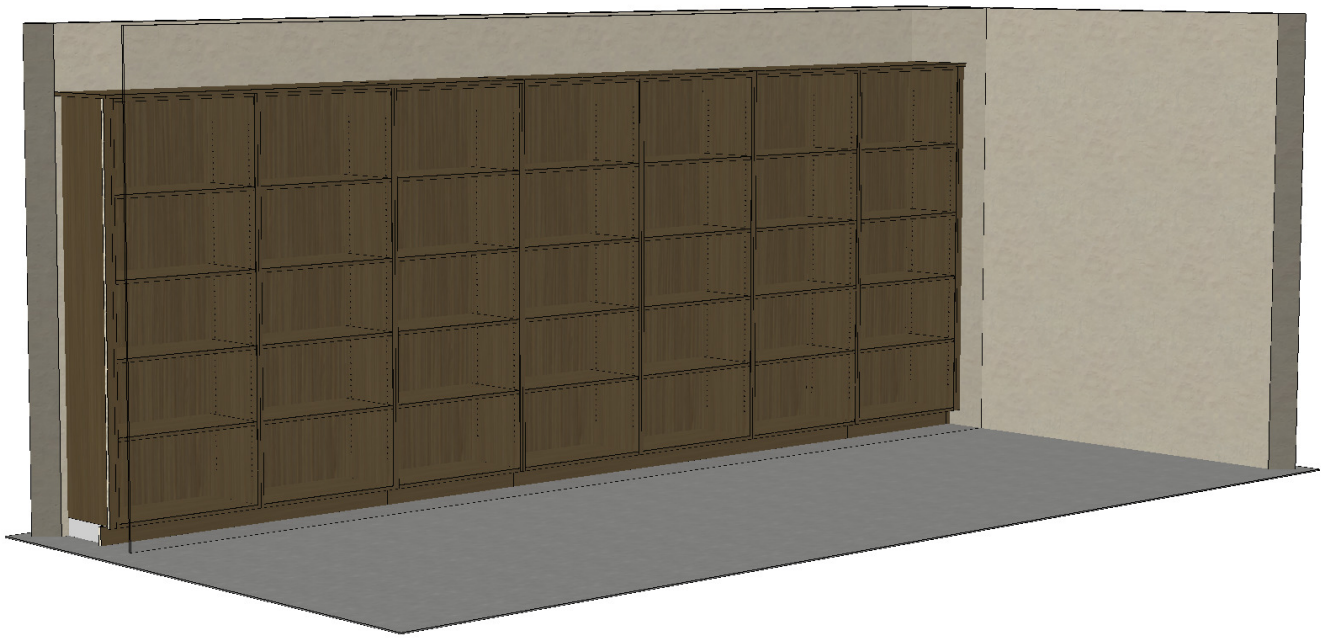

CLOSET CREATIONS

Closet Creations
4058 S. River Road
St. George, UT 84790

Phone: 435-656-5564
Fax:

P26-0305
RAC Inc.
Craig Engel
(435) 229-7360
1267 N 1390 W
St. George, UT 84770

RAC Inc - Rodriguez Res
Rodriguez Residence
Oak Valley Estates Lot 5
Kanarraville, UT
Design:
05/27/26


Approval




Wall 2
3/8 " = 1 '

RM#10 - Vault Elev 2


CLOSET CREATIONS	**Closet Creations** 4058 S. River Road St. George, UT 84790 Phone: 435-656-5564 Fax:	**P26-0305** RAC Inc. Craig Engel (435) 229-7360 1267 N 1390 W St. George, UT 84770	**RAC Inc - Rodriguez Res** Rodriguez Residence Oak Valley Estates Lot 5 Kanarraville, UT Design: 05/27/26	**Approval**

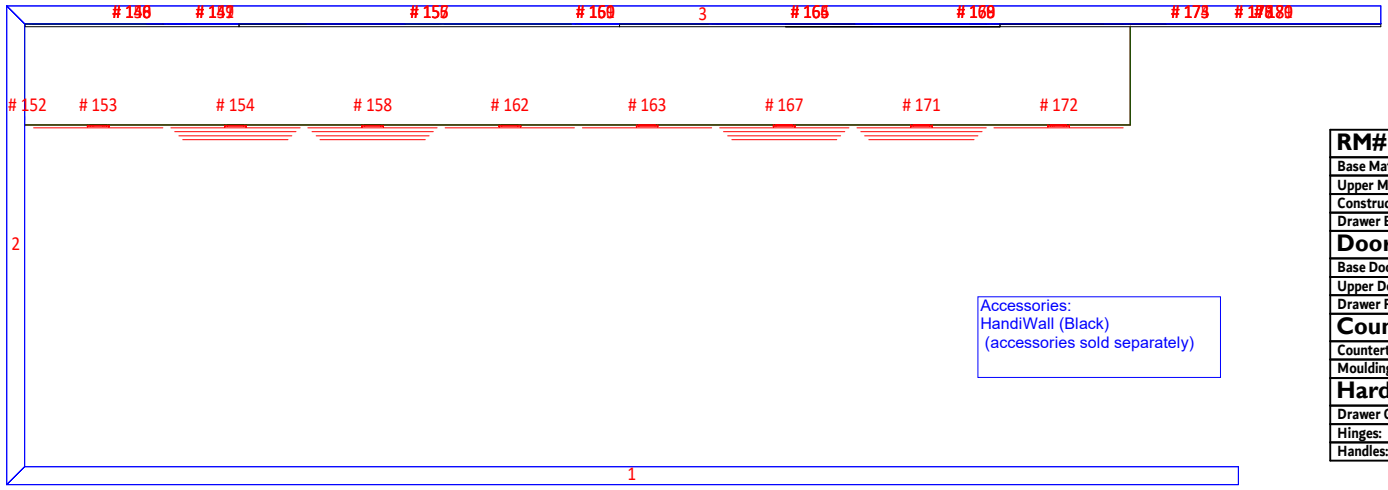

RM#11 - Armory	
Base Material:	Lochsa Rosewood 1mm, White Int.
Upper Material:	Lochsa Rosewood 1mm, White Int.
Construction:	Cabinets - Doweled
Drawer Box Style:	5/8 W/Dado Undermount
Door Specs	
Base Door Style:	Slab CC Door, Lochsa Rosewood 1mm
Upper Door Style:	Slab CC Door, Lochsa Rosewood 1mm
Drawer Front Style:	Slab CC Door, Lochsa Rosewood 1mm
Countertop/Moulding	
Countertop:	Butcher Block Beech 1 3/8, Butcher Bloc
Moulding:	None, Lochsa Rosewood 3/4
Hardware Specs	
Drawer Guide:	PRO 600
Hinges:	Soft Silentia 120 Degree Euro
Handles:	Metro SN (Stock) STUP822BSN-128

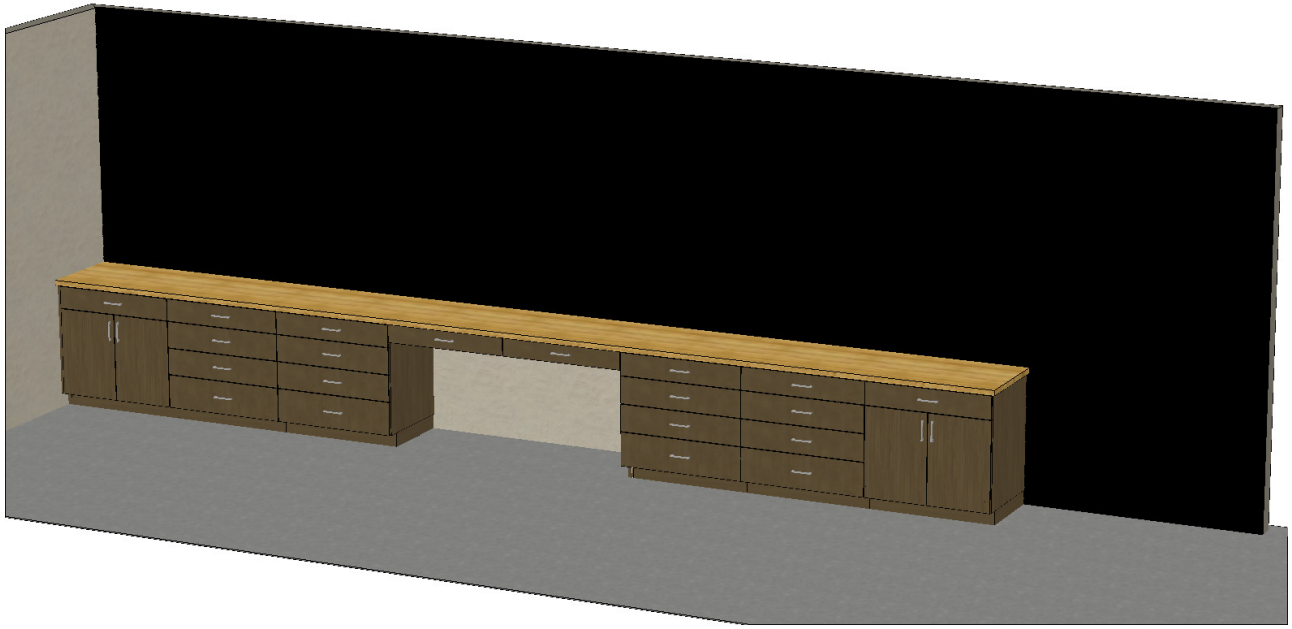


CLOSET CREATIONS	**Closet Creations** 4058 S. River Road St. George, UT 84790 Phone: 435-656-5564 Fax:	**P26-0305** RAC Inc. Craig Engel (435) 229-7360 1267 N 1390 W St. George, UT 84770	**RAC Inc - Rodriguez Res** Rodriguez Residence Oak Valley Estates Lot 5 Kanarraville, UT Design: 05/27/26	**Approval**

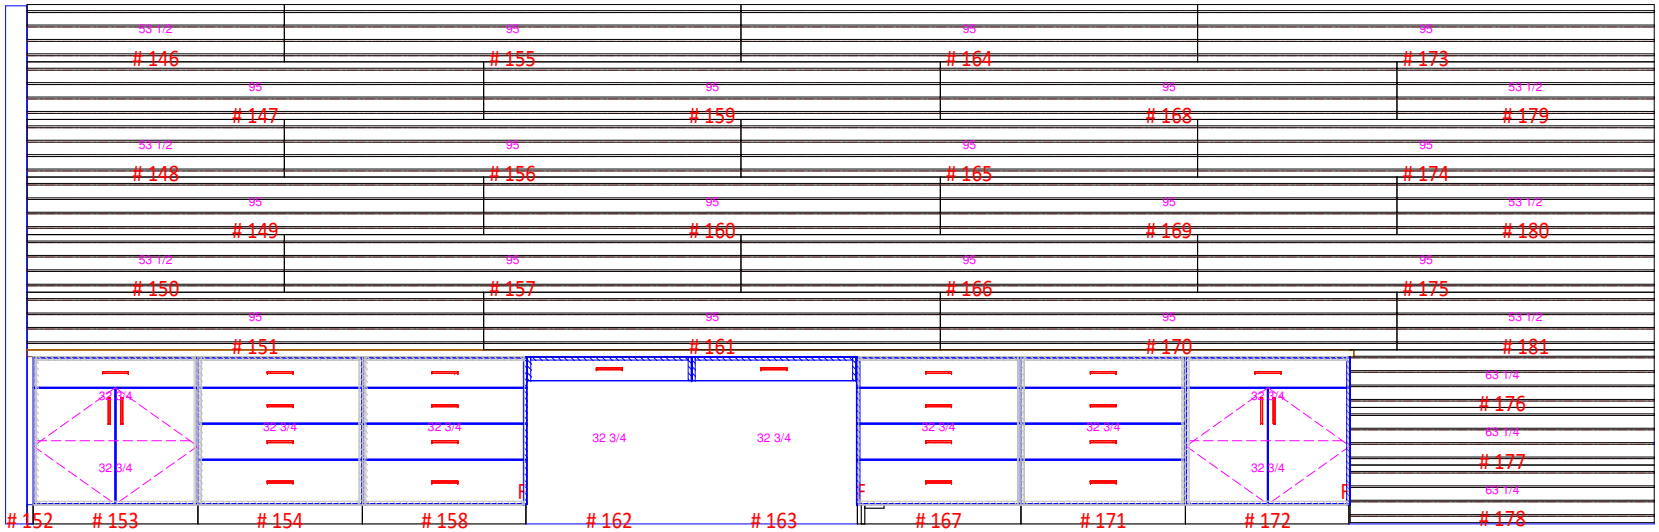


Wall 3
1:40

RM#11 - Armory Elev 3

CLOSET CREATIONS	**Closet Creations** 4058 S. River Road St. George, UT 84790 Phone: 435-656-5564 Fax:	**P26-0305** RAC Inc. Craig Engel (435) 229-7360 1267 N 1390 W St. George, UT 84770	**RAC Inc - Rodriguez Res** Rodriguez Residence Oak Valley Estates Lot 5 Kanarraville, UT Design: 05/27/26	**Approval**

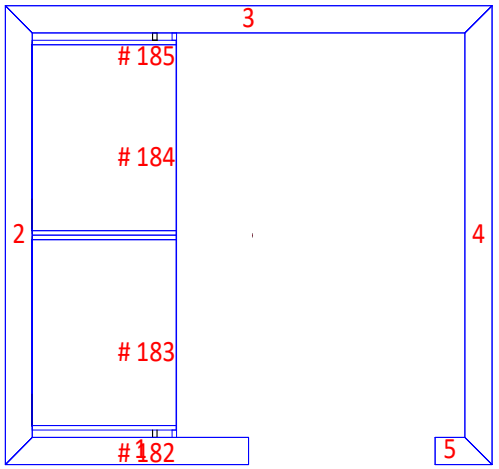

RM#12 - Basement Storage	
Material:	Lochsa Rosewood 1mm
Construction:	Standard Closet
Drawer Box Style:	None
Door Specs	
Base Door Style:	None, None
Upper Door Style:	None, None
Drawer Front Style:	None, None
Countertop/Moulding	
Countertop:	None, None
Moulding:	None, None
Hardware Specs	
Closet Rods:	None
Drawer Guide:	None
Hinges:	None
Handles:	None

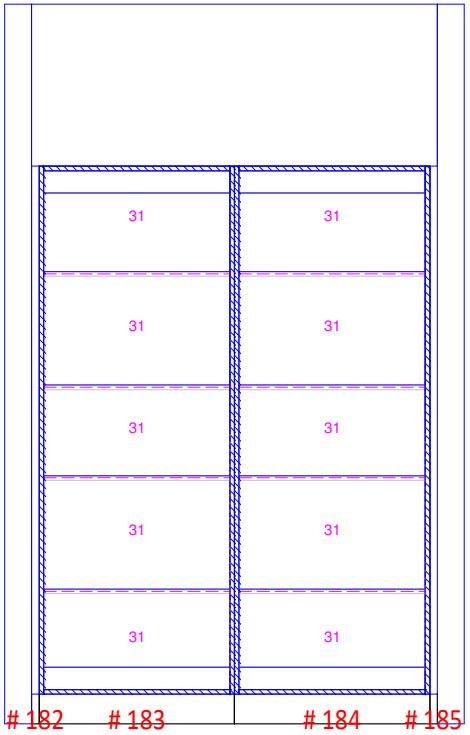



Wall 2
3/8" = 1'
RM#12 - Basement Storage Elev 2




CLOSET CREATIONS	**Closet Creations** 4058 S. River Road St. George, UT 84790 Phone: 435-656-5564 Fax:	**P26-0305** RAC Inc. Craig Engel (435) 229-7360 1267 N 1390 W St. George, UT 84770	**RAC Inc - Rodriguez Res** Rodriguez Residence Oak Valley Estates Lot 5 Kanarraville, UT Design: 05/27/26	**Approval**

RM#13 - Coat Closet	
Material:	Lochsa Rosewood 1mm
Construction:	Standard Closet
Drawer Box Style:	None
Door Specs	
Base Door Style:	None, None
Upper Door Style:	None, None
Drawer Front Style:	None, None
Countertop/Moulding	
Countertop:	None, None
Moulding:	None, None
Hardware Specs	
Closet Rods:	Chrome Closet Rods Oval
Drawer Guide:	None
Hinges:	None
Handles:	None

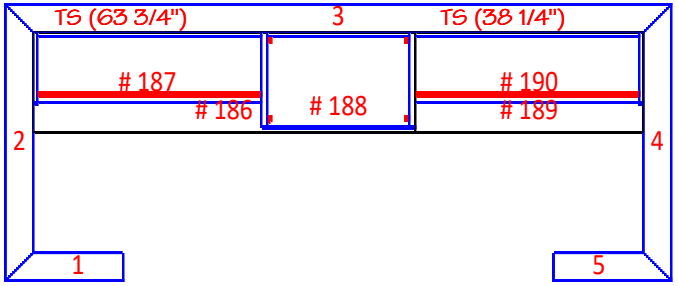


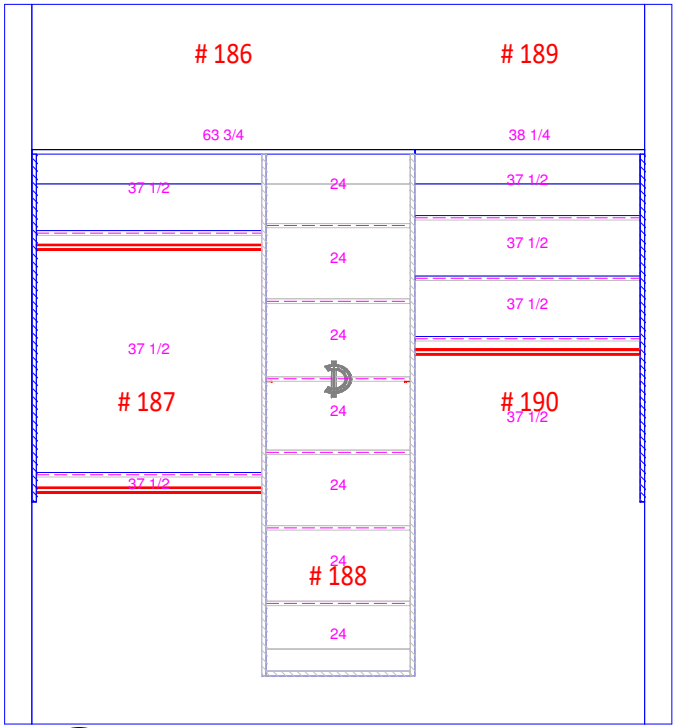

Wall 3
3/8" = 1'
RM#13 - Coat Closet Elev 3

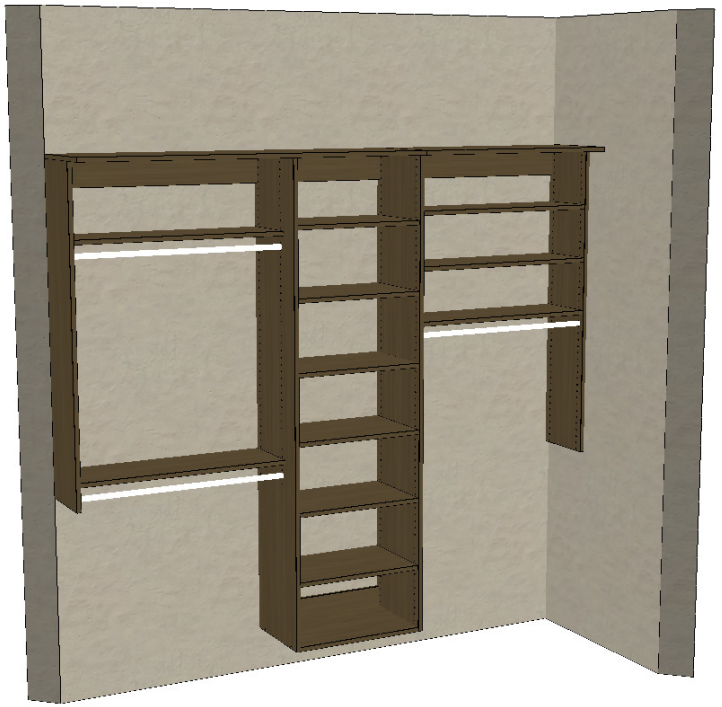


CLOSET CREATIONS	**Closet Creations** 4058 S. River Road St. George, UT 84790 Phone: 435-656-5564 Fax:	**P26-0305** RAC Inc. Craig Engel (435) 229-7360 1267 N 1390 W St. George, UT 84770	**RAC Inc - Rodriguez Res** Rodriguez Residence Oak Valley Estates Lot 5 Kanarraville, UT Design: 05/27/26	**Approval**

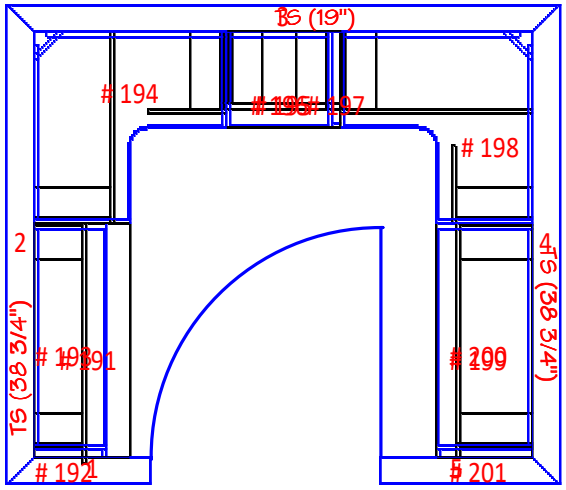


RM#14 - Pantry	
Material:	Lochsa Rosewood 1mm
Construction:	Standard Closet
Drawer Box Style:	None
Door Specs	
Base Door Style:	None, None
Upper Door Style:	None, None
Drawer Front Style:	None, None
Countertop/Moulding	
Countertop:	None, None
Moulding:	None, None
Hardware Specs	
Closet Rods:	None
Drawer Guide:	None
Hinges:	None
Handles:	None


CLOSET CREATIONS	**Closet Creations** 4058 S. River Road St. George, UT 84790 Phone: 435-656-5564 Fax:	**P26-0305** RAC Inc. Craig Engel (435) 229-7360 1267 N 1390 W St. George, UT 84770	**RAC Inc - Rodriguez Res** Rodriguez Residence Oak Valley Estates Lot 5 Kanarraville, UT Design: 05/27/26	**Approval**

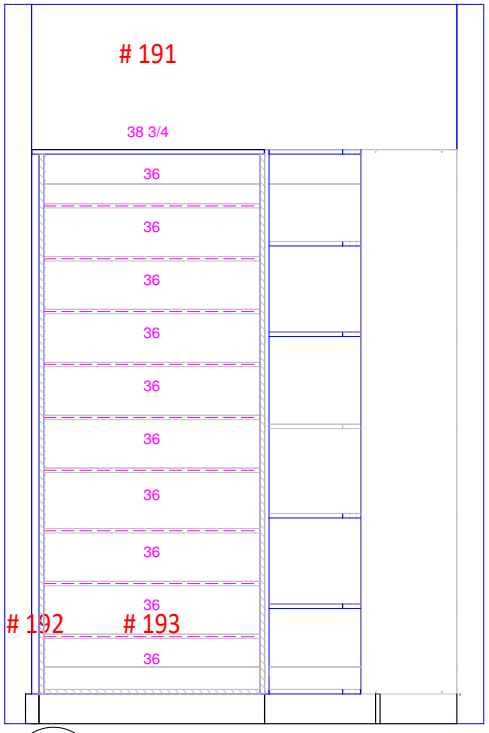

Wall 2 3/8" = 1' RM#14 - Pantry Elev 2

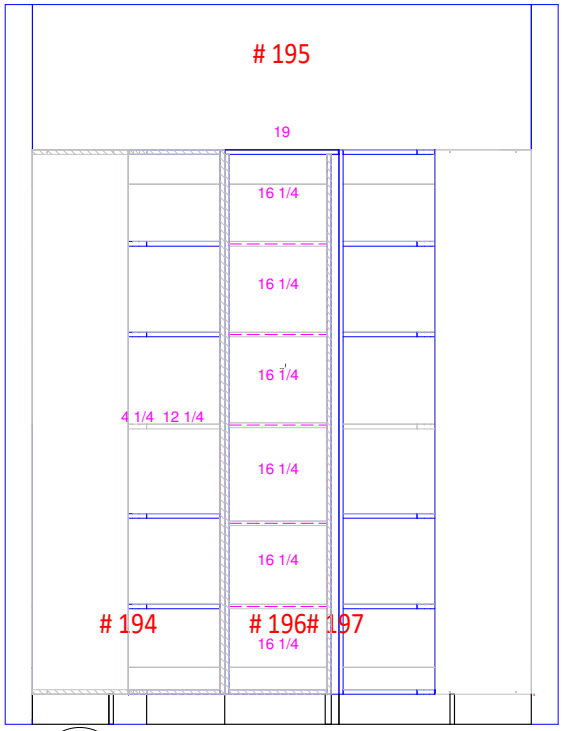

Wall 3 3/8" = 1' RM#14 - Pantry Elev 3

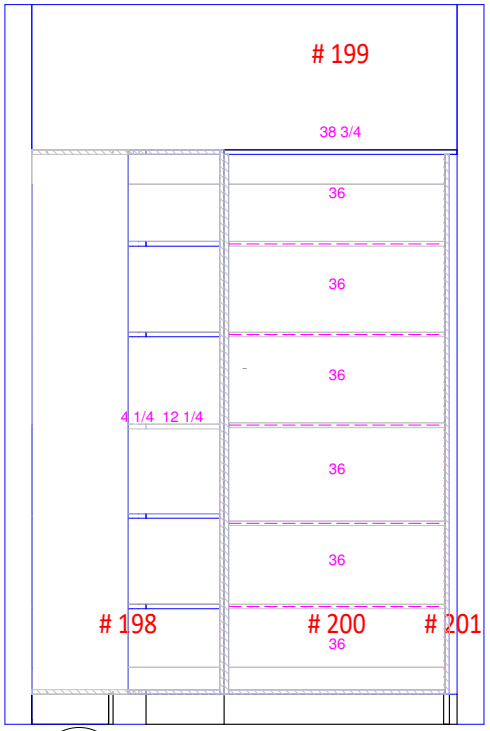


Wall 4 3/8" = 1' RM#14 - Pantry Elev 4

CLOSET CREATIONS	**Closet Creations** 4058 S. River Road St. George, UT 84790 Phone: 435-656-5564 Fax:	**P26-0305** RAC Inc. Craig Engel (435) 229-7360 1267 N 1390 W St. George, UT 84770	**RAC Inc - Rodriguez Res** Rodriguez Residence Oak Valley Estates Lot 5 Kanarraville, UT Design: 05/27/26	**Approval**






CLOSET CREATIONS	**Closet Creations** 4058 S. River Road St. George, UT 84790 Phone: 435-656-5564 Fax:	**P26-0305** RAC Inc. Craig Engel (435) 229-7360 1267 N 1390 W St. George, UT 84770	**RAC Inc - Rodriguez Res** Rodriguez Residence Oak Valley Estates Lot 5 Kanarraville, UT Design: 05/27/26	**Approval**

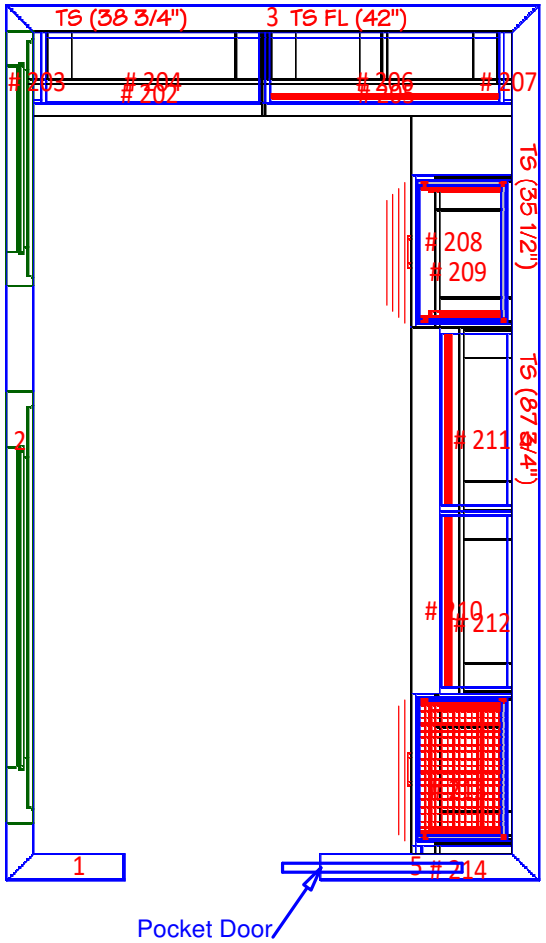


RM#15 - Casita Closet	
Material:	Lochsa Rosewood 1mm
Construction:	Standard Closet
Drawer Box Style:	5/8 W/Dado Undermount
Door Specs	
Base Door Style:	Slab CC Door, Lochsa Rosewood 1mm
Upper Door Style:	Slab CC Door, Lochsa Rosewood 1mm
Drawer Front Style:	Slab CC Door, Lochsa Rosewood 1mm
Countertop/Moulding	
Countertop:	Supplied By Others, Supplied By Other
Moulding:	None, Lochsa Rosewood 3/4
Hardware Specs	
Closet Rods:	Chrome Closet Rods Oval
Drawer Guide:	PRO 600
Hinges:	Soft Silentia 120 Degree Euro
Handles:	Metro SN (Stock) STUP822BSN-128

Accessories:
Wire Hamper Kit

CLOSET CREATIONS	**Closet Creations** 4058 S. River Road St. George, UT 84790 Phone: 435-656-5564 Fax:	**P26-0305** RAC Inc. Craig Engel (435) 229-7360 1267 N 1390 W St. George, UT 84770	**RAC Inc - Rodriguez Res** Rodriguez Residence Oak Valley Estates Lot 5 Kanarraville, UT Design: 05/27/26	**Approval**

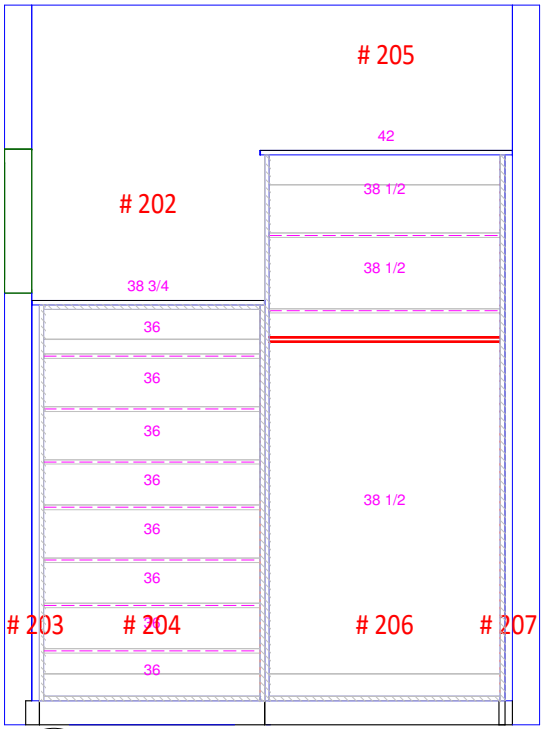

Wall 3
3/8 " = 1 '
RM#15 - Casita Closet Elev 3

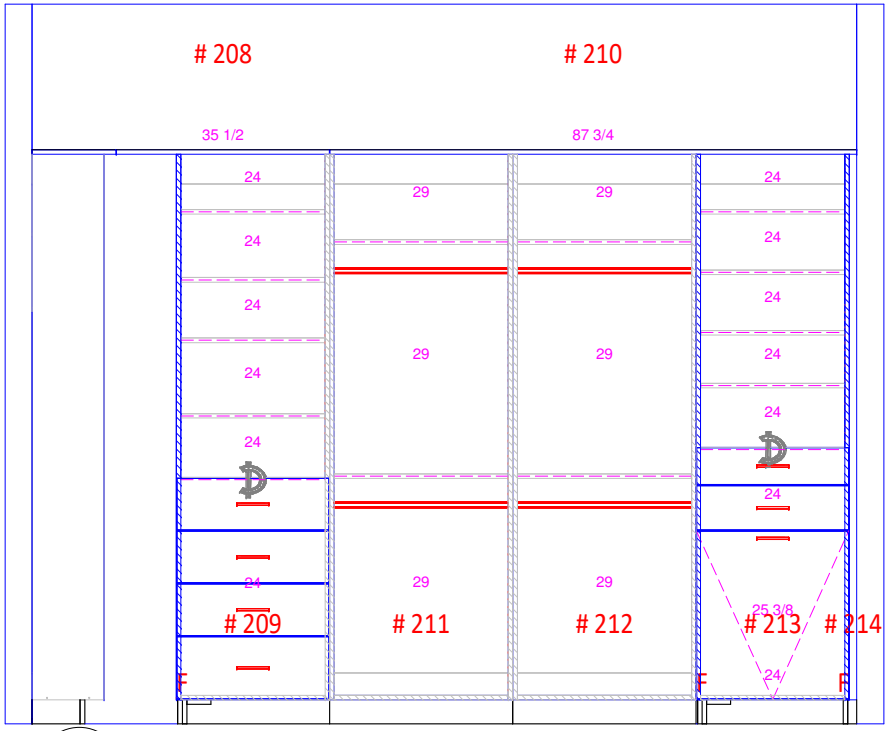


Wall 4
3/8 " = 1 '
RM#15 - Casita Closet Elev 4


CLOSET CREATIONS	**Closet Creations** 4058 S. River Road St. George, UT 84790 Phone: 435-656-5564 Fax:	**P26-0305** RAC Inc. Craig Engel (435) 229-7360 1267 N 1390 W St. George, UT 84770	**RAC Inc - Rodriguez Res** Rodriguez Residence Oak Valley Estates Lot 5 Kanarraville, UT Design: 05/27/26	**Approval**



CLOSET CREATIONS	**Closet Creations** 4058 S. River Road St. George, UT 84790 Phone: 435-656-5564 Fax:	**P26-0305** RAC Inc. Craig Engel (435) 229-7360 1267 N 1390 W St. George, UT 84770	**RAC Inc - Rodriguez Res** Rodriguez Residence Oak Valley Estates Lot 5 Kanarraville, UT Design: 05/27/26	**Approval**

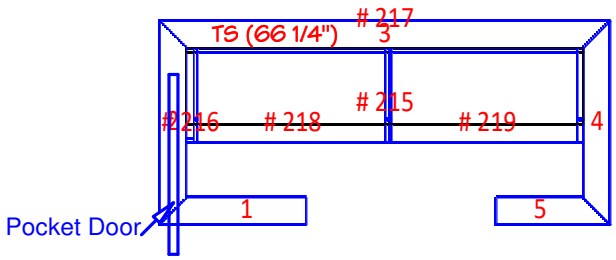


RM#16 - Primary Linen	
Material:	Lochsa Rosewood 1mm
Construction:	Standard Closet
Drawer Box Style:	None
Door Specs	
Base Door Style:	None, None
Upper Door Style:	None, None
Drawer Front Style:	None, None
Countertop/Moulding	
Countertop:	None, None
Moulding:	None, None
Hardware Specs	
Closet Rods:	None
Drawer Guide:	None
Hinges:	None
Handles:	None

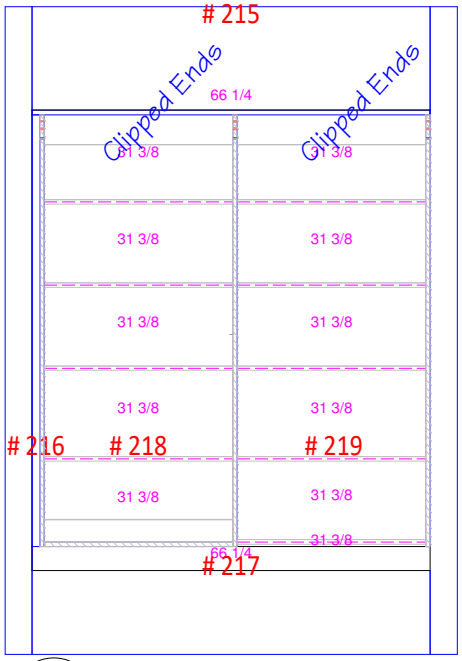


Wall 3
3/8 " = 1 '
RM#16 - Primary Linen Elev 3




CLOSET CREATIONS	**Closet Creations** 4058 S. River Road St. George, UT 84790 Phone: 435-656-5564 Fax:	**P26-0305** RAC Inc. Craig Engel (435) 229-7360 1267 N 1390 W St. George, UT 84770	**RAC Inc - Rodriguez Res** Rodriguez Residence Oak Valley Estates Lot 5 Kanarraville, UT Design: 05/27/26	**Approval**

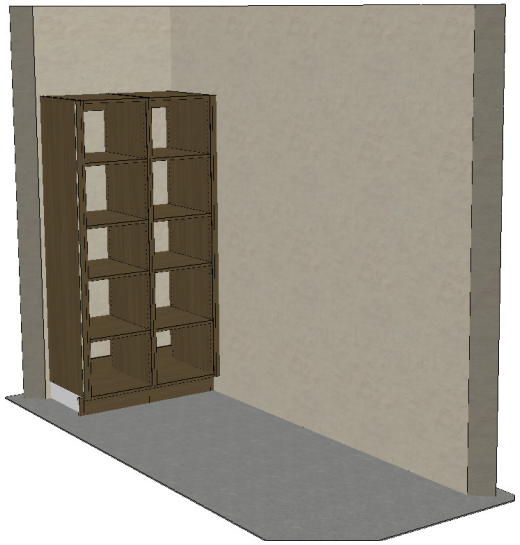

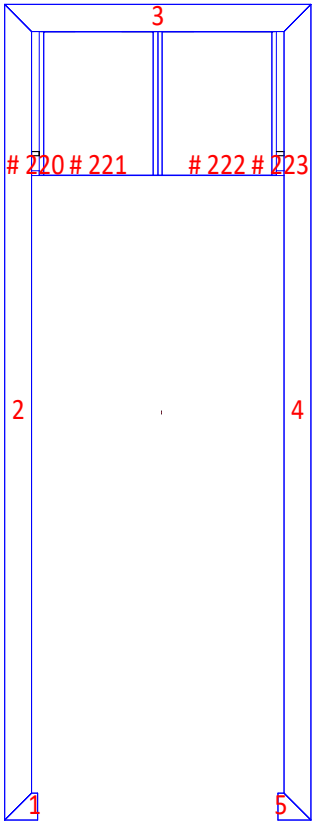


RM#17 - Balcony Storage	
Material:	Lochsa Rosewood 1mm
Construction:	Standard Closet
Drawer Box Style:	None
Door Specs	
Base Door Style:	None, None
Upper Door Style:	None, None
Drawer Front Style:	None, None
Countertop/Moulding	
Countertop:	None, None
Moulding:	None, None
Hardware Specs	
Closet Rods:	None
Drawer Guide:	None
Hinges:	None
Handles:	None

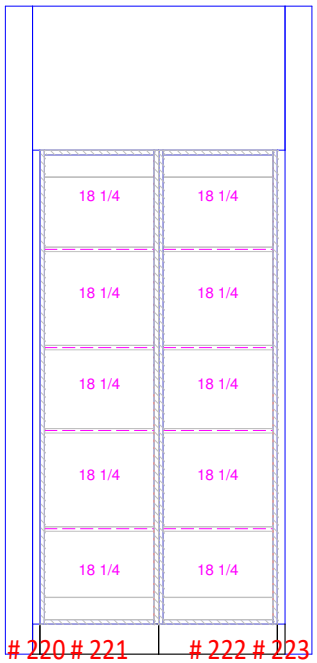


Wall 3
3/8 " = 1 '
RM#17 - Balcony Storage Elev 3

CLOSET CREATIONS	**Closet Creations** 4058 S. River Road St. George, UT 84790 Phone: 435-656-5564 Fax:	**P26-0305** RAC Inc. Craig Engel (435) 229-7360 1267 N 1390 W St. George, UT 84770	**RAC Inc - Rodriguez Res** Rodriguez Residence Oak Valley Estates Lot 5 Kanarraville, UT Design: 05/27/26	**Approval**

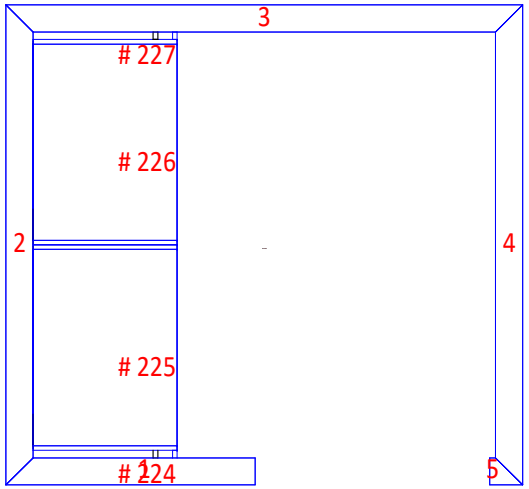

RM#18 - Outdoor Storage	
Material:	Lochsa Rosewood 1mm
Construction:	Standard Closet
Drawer Box Style:	None
Door Specs	
Base Door Style:	None, None
Upper Door Style:	None, None
Drawer Front Style:	None, None
Countertop/Moulding	
Countertop:	None, None
Moulding:	None, None
Hardware Specs	
Closet Rods:	None
Drawer Guide:	None
Hinges:	None
Handles:	None

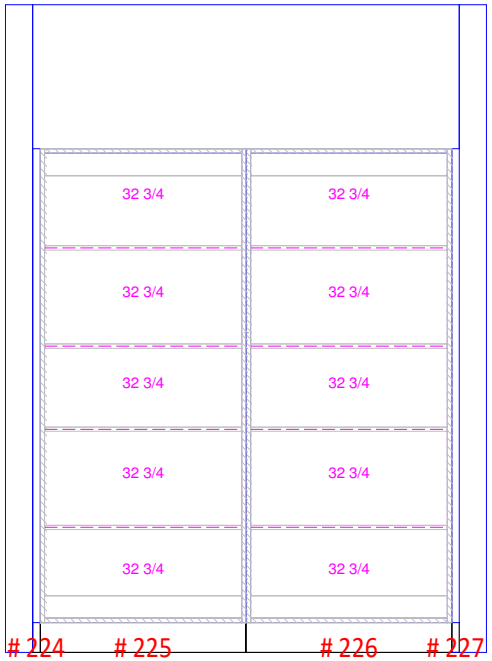

Wall 2
3/8 " = 1 '

RM#18 - Outdoor Storage Elev 2



CLOSET CREATIONS	**Closet Creations** 4058 S. River Road St. George, UT 84790 Phone: 435-656-5564 Fax:	**P26-0305** RAC Inc. Craig Engel (435) 229-7360 1267 N 1390 W St. George, UT 84770	**RAC Inc - Rodriguez Res** Rodriguez Residence Oak Valley Estates Lot 5 Kanarraville, UT Design: 05/27/26	**Approval**