

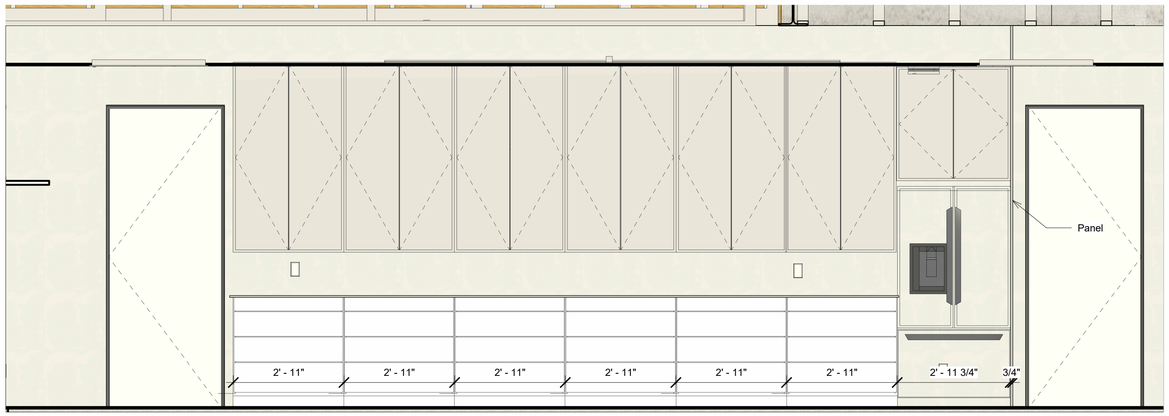



6 Cab Pantry
1/2" = 1'-0"

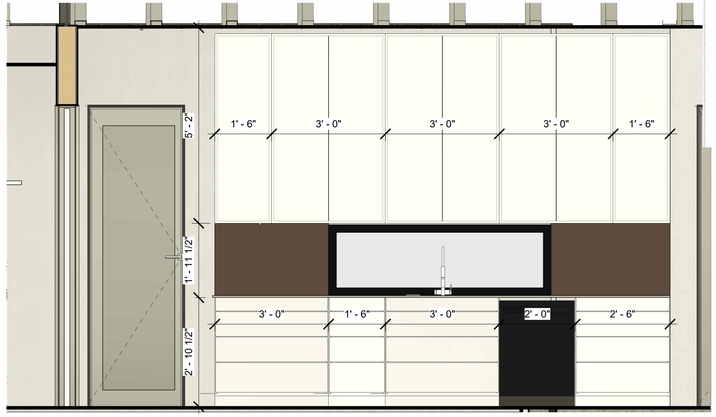


1 Cab Kitchen -2
1/2" = 1'-0"

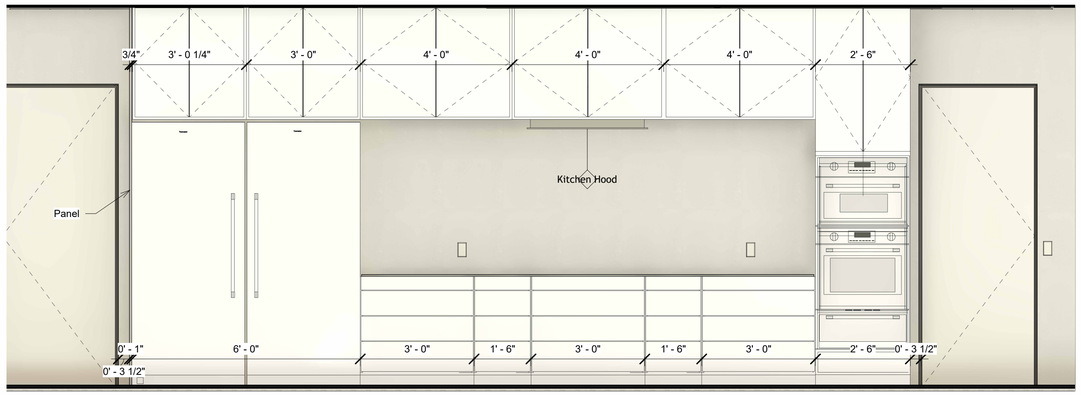

3 Cab KItchen-1
1/2" = 1'-0"

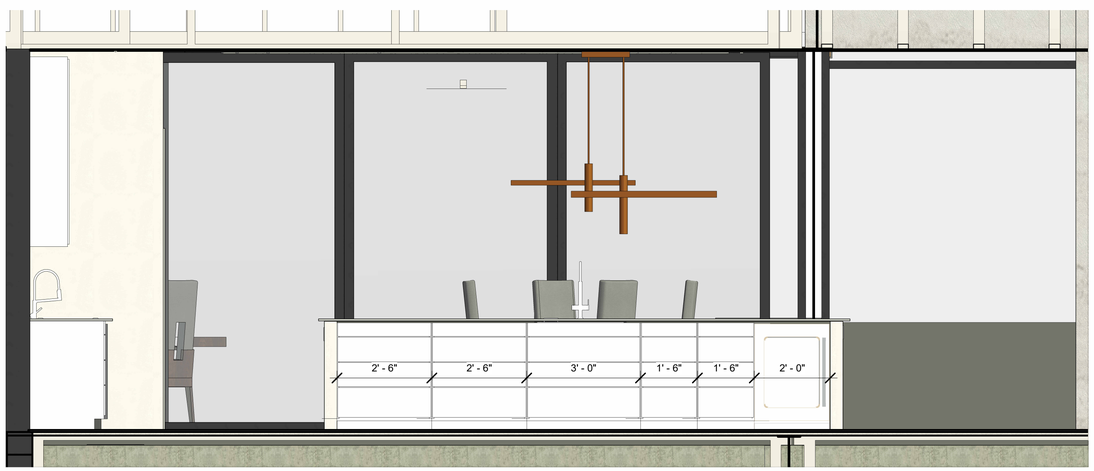

2 Cab Kitchen ISL-1
1/2" = 1'-0"

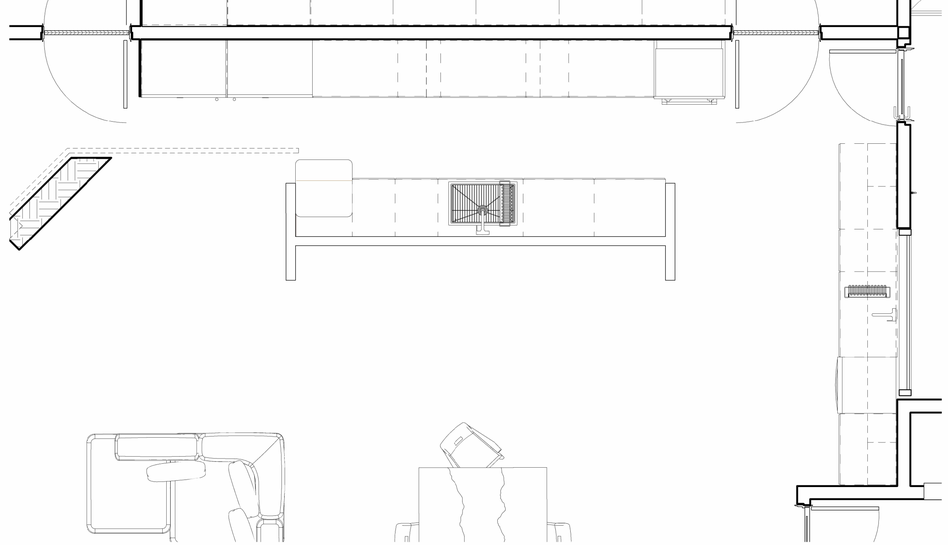

10 2-Main Copy 1
3/8" = 1'-0"

RAC Development

Consultant Craig Engel
Firm RAC Development
Address 1267 N.. 1390 W . St. George UT
Phone (435) 229-7360
Fax
e-mail racinc19@gmail.com

Consultant
Firm
Address
Phone
Fax
e-mail

Consultant
Firm
Address
Phone
Fax
e-mail

Consultant
Firm
Address
Phone
Fax
e-mail

Consultant
Firm
Address
Phone
Fax
e-mail

No.	Description	Date

Mr. & Mrs. Rodriguez

Oak Valley Estates #5

Cabinets Main

Project number	Project Number
Date	Issue Date
Drawn by	Author
Checked by	Checker

A901

Scale As indicated

9/15/2026 9:25:39 PM