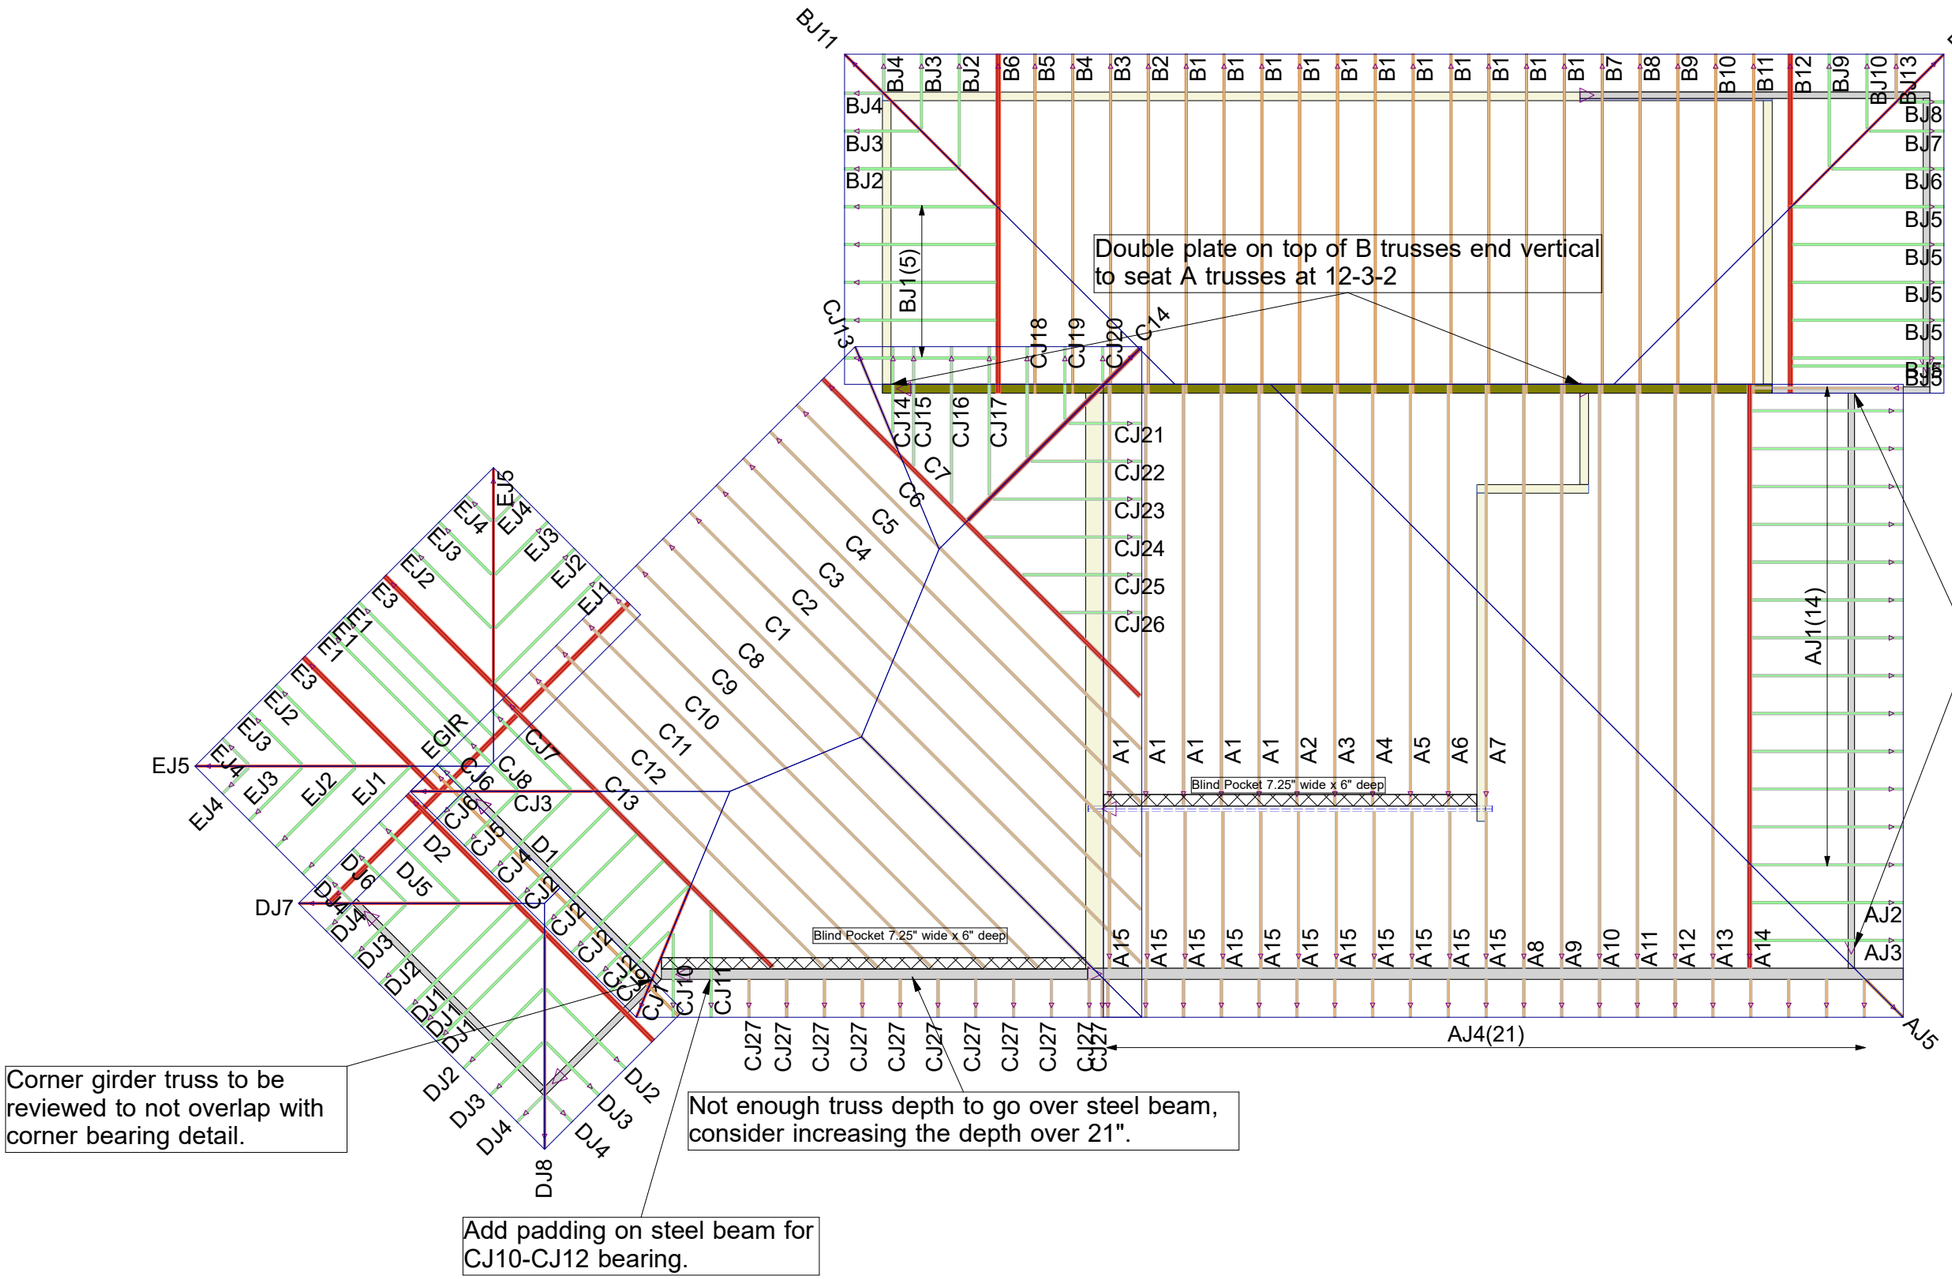


Preliminary Truss Placement Drawing
Not for construction

1177 E Venture Dr.
St. George UT 84790
United States
Office:
(801) 222-3300

SUNPRO

Order # 254084-R

Rodriguez Residence
RAC Inc.

LOT 5 Oak Valley Estates, Kannerville, UT

Sales Rep: Chris Zimmerschied (208) 965-0004
Designer: Sam Garcia

Roof Truss Design Criteria
Building Code = ASCE716, IRC 2021
Flat Roof Snow Load = 30.0 lb/ft²
Top Chord Dead Load = 12.0 lb/ft²
Bottom Chord Dead Load = 7.0 lb/ft²

Issued Date: 4/2/2026

DO NOT CUT OR MODIFY TRUSSES
without authorization from Sunpro Corporation. Please contact your sales representative prior to any modification and/or repairs that may need to be made. Any back charges as a result of damage or modifications made without the consent of Sunpro Building Materials will not be honored. Refer to BCSI-B1 sheet for HANDLING, INSTALLING, RESTRAINING AND BRACING OF TRUSSES. Truss layout is for placement only, refer to truss drawings for spacing, bracing, multi-ply nailing and bearing requirements.