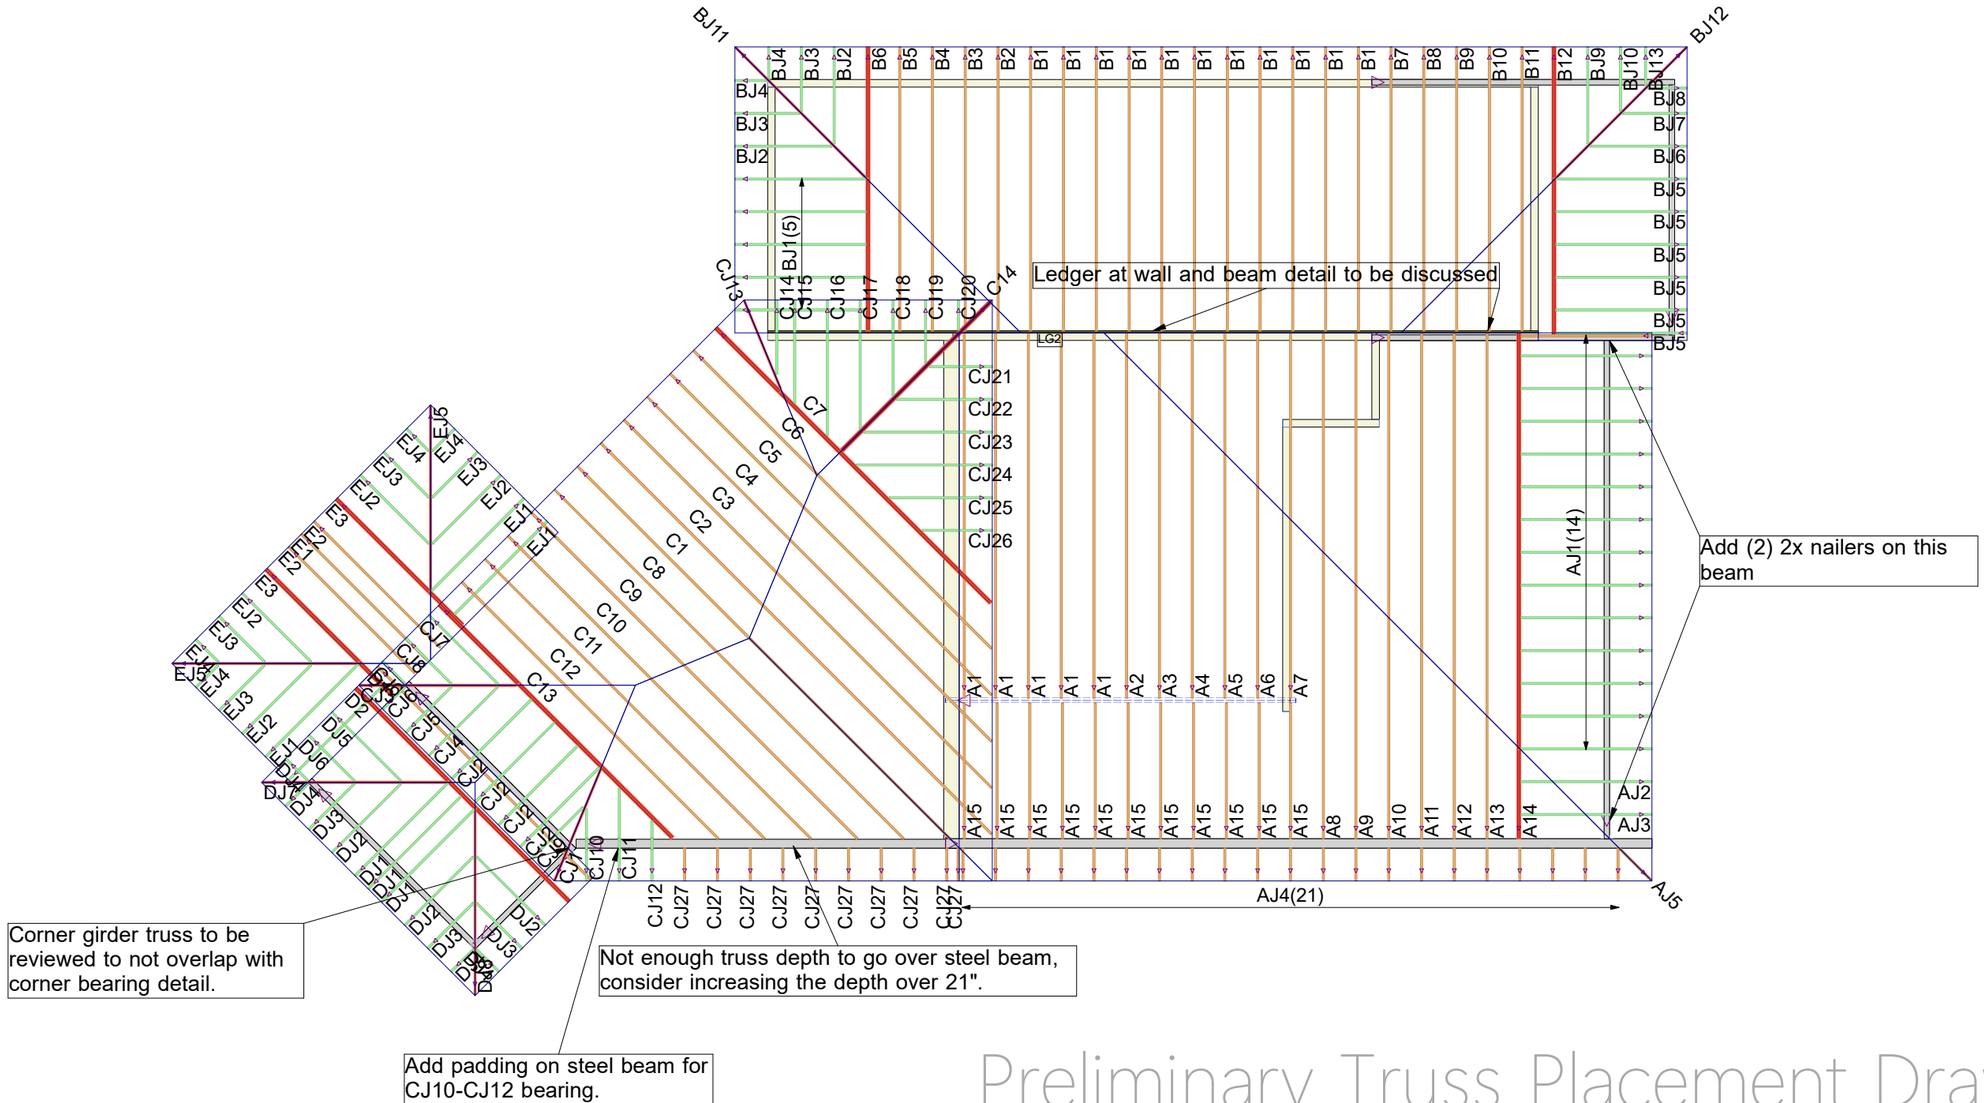



Preliminary Truss Placement Drawing
Not for construction

**DO NOT CUT OR MODIFY TRUSSES**

**without authorization from SUNPRO. Please contact your sales representative prior to any modification and/or repairs that may need to be made. Any back charges as a result of damage or modifications made without the consent of Sunroc Building Materials will not be honored. Refer to BCSI-B1 sheet for HANDLING, INSTALLING, RESTRAINING AND BRACING OF TRUSSES. Truss layout is for placement only, refer to truss drawings for spacing, bracing, multi-ply nailing and bearing requirements.**

| Roof Truss Design Criteria |
|---|
| Building Code = ASCE716, IRC 2021 |
| Top Chord Snow Load = 30.0 lb/ft² |
| TC Const Live Load = 0.0 lb/ft² |
| Top Chord Dead Load = 11.0 lb/ft² |
| Bottom Chord Dead Load = 7.0 lb/ft² |
| Deflection LL = L/360 TL = L/240 |

**Issued Date: 3/9/2026**

# Rodriguez Residence

RAC Inc.

LOT 5 Oak Valley Estates, Kannerville, UT

Sales Rep: Chris Zimmerschied (208) 965-0004
Designer: Sam Garcia

SUNPRO
1177 E Venture Dr, St George UT 84790
Office (801) 222-3300

**Order # 254084-R**