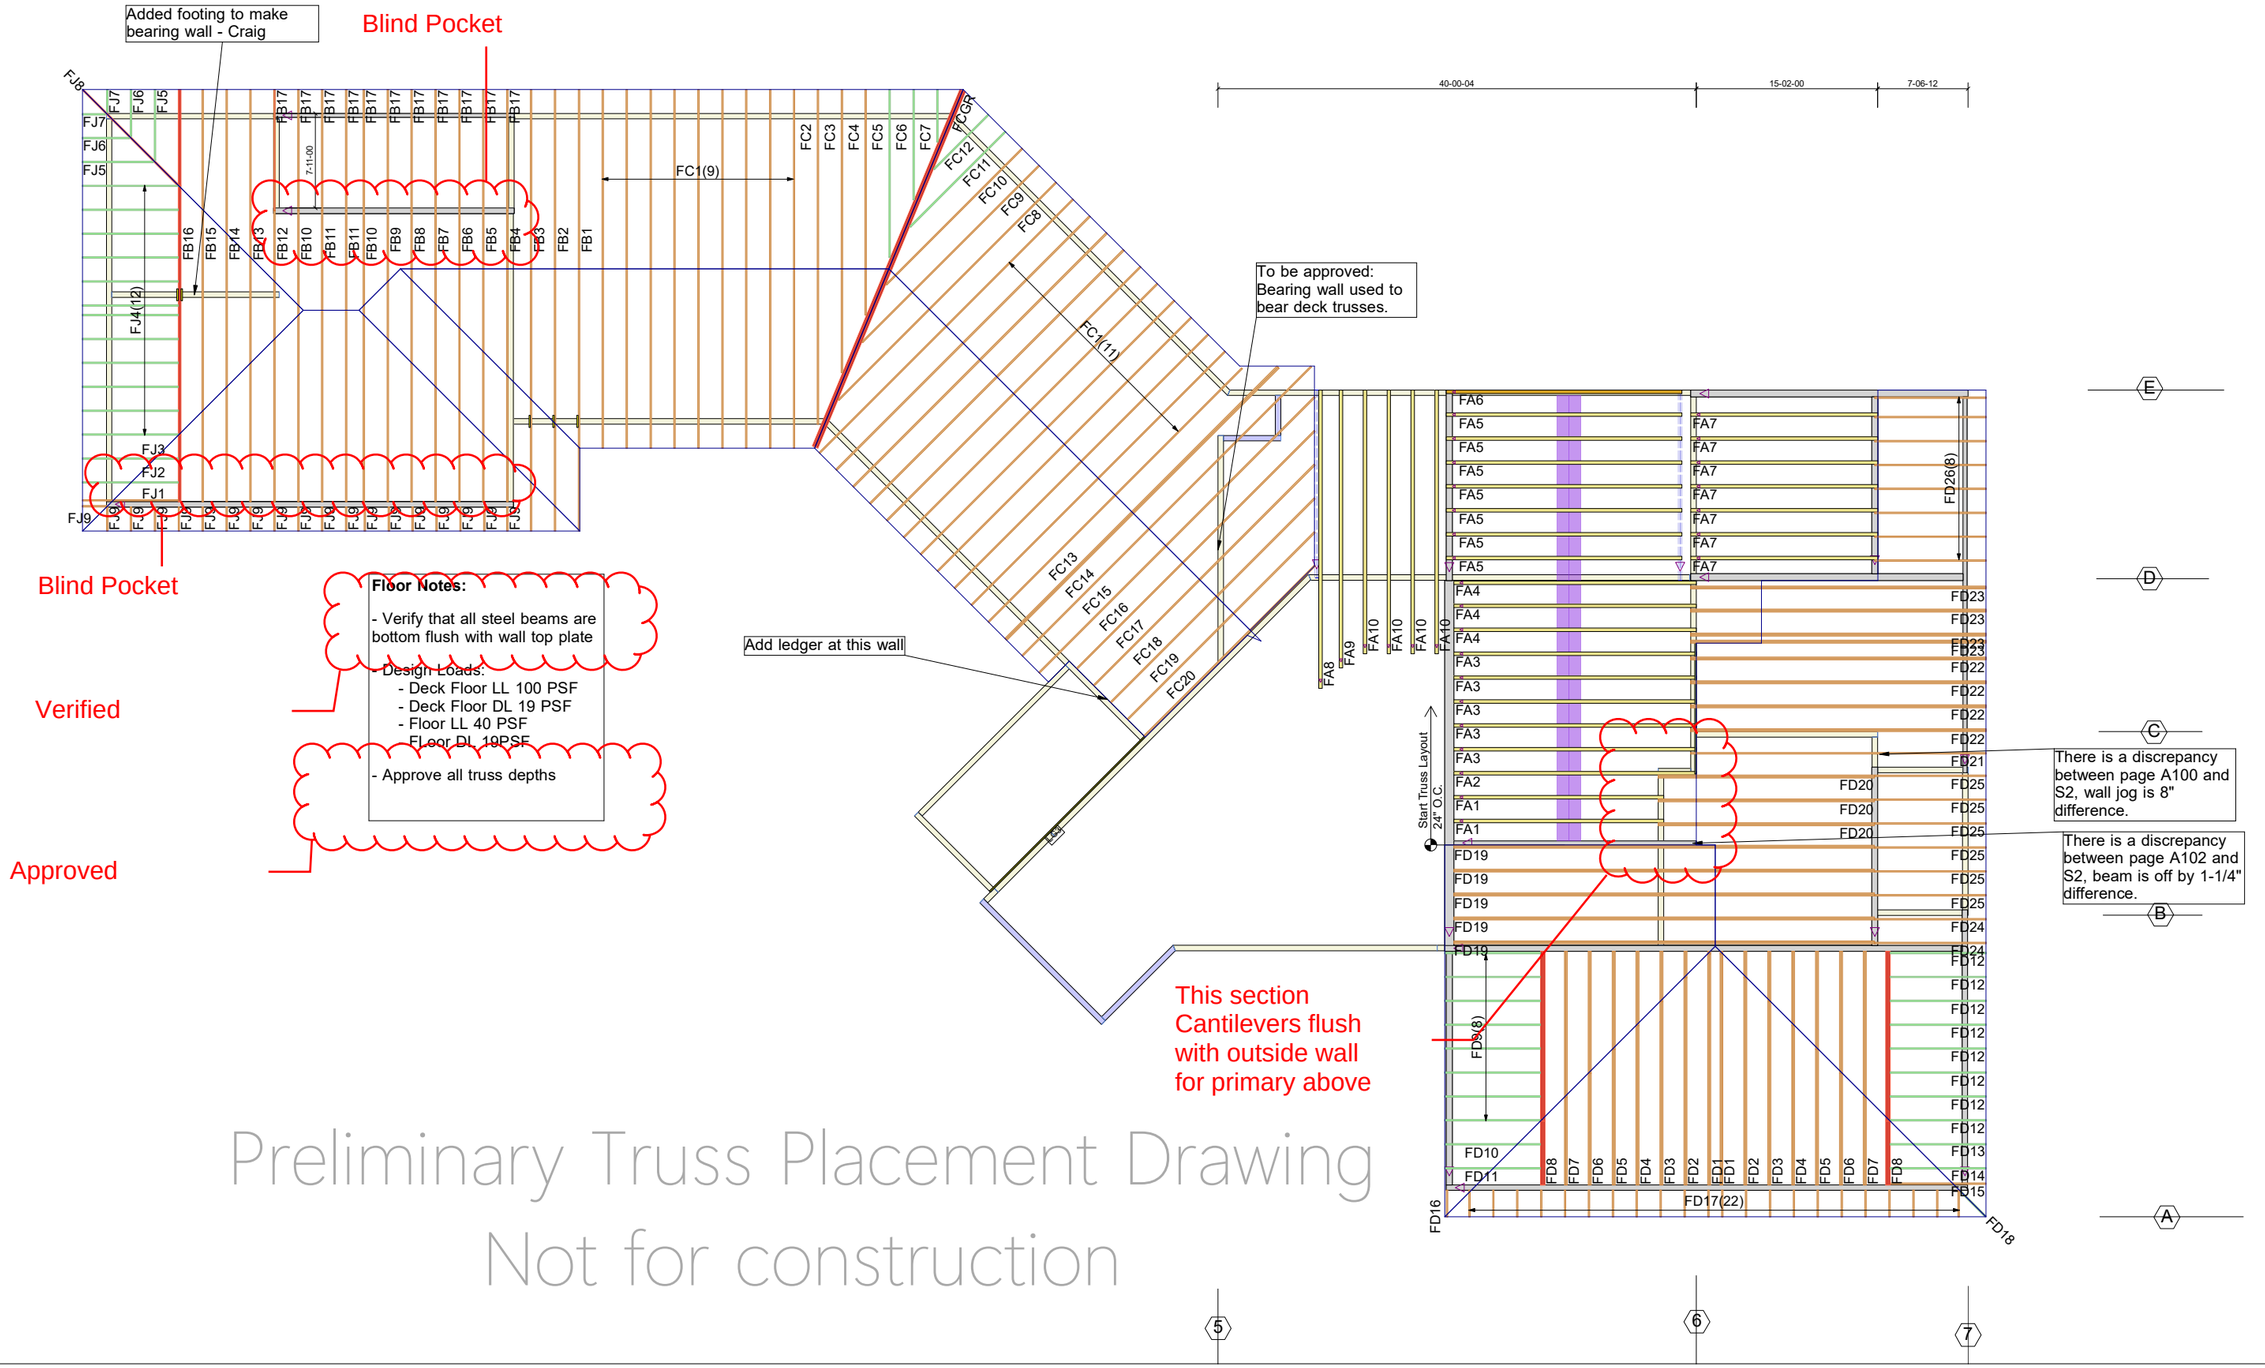


Preliminary Truss Placement Drawing
Not for construction

DO NOT CUT OR MODIFY TRUSSES

without authorization from SUNPRO. Please contact your sales representative prior to any modification and/or repairs that may need to be made. Any back charges as a result of damage or modifications made without the consent of Sunroc Building Materials will not be honored. Refer to BCSI-B1 sheet for HANDLING, INSTALLING, RESTRAINING AND BRACING OF TRUSSES. Truss layout is for placement only, refer to truss drawings for spacing, bracing, multi-ply nailing and bearing requirements.

Floor Truss Design Criteria
Building Code = ASCE716, IRC 2021
Top Chord Live Load = 40.0 lb/ft²
Top Chord Dead Load = 11.0 lb/ft²
Bottom Chord Dead Load = 7.0 lb/ft²
Deflection LL = L/360 TL = L/240

Issued Date: 3/9/2026

Rodriguez Residence

RAC Inc.

LOT 5 Oak Valley Estates, Kannerville, UT

Sales Rep: Chris Zimmerschied (208) 965-0004
Designer: Sam Garcia

SUNPRO
1177 E Venture Dr, St George UT 84790
Office (801) 222-3300

Order # 254084-UF