



Consultant Craig Engel
Firm RAC Development
Address 1267 N. 1390 W. St. George UT
Phone (435) 229-7360
Fax
e-mail racinc19@gmail.com

Consultant
Firm
Address
Phone
Fax
e-mail

Consultant
Firm
Address
Phone
Fax
e-mail

Consultant
Firm
Address
Phone
Fax
e-mail


Consultant
Firm
Address
Phone
Fax
e-mail

[illegible]



Mr. & Mrs. Rodriguez Oak Valley Estates #5 Plumbing

Project number	Project Number
Date	Issue Date
Drawn by	Author
Checked by	Checker
P100	
Scale	As indicated

3/9/2026 8:55:41 AM

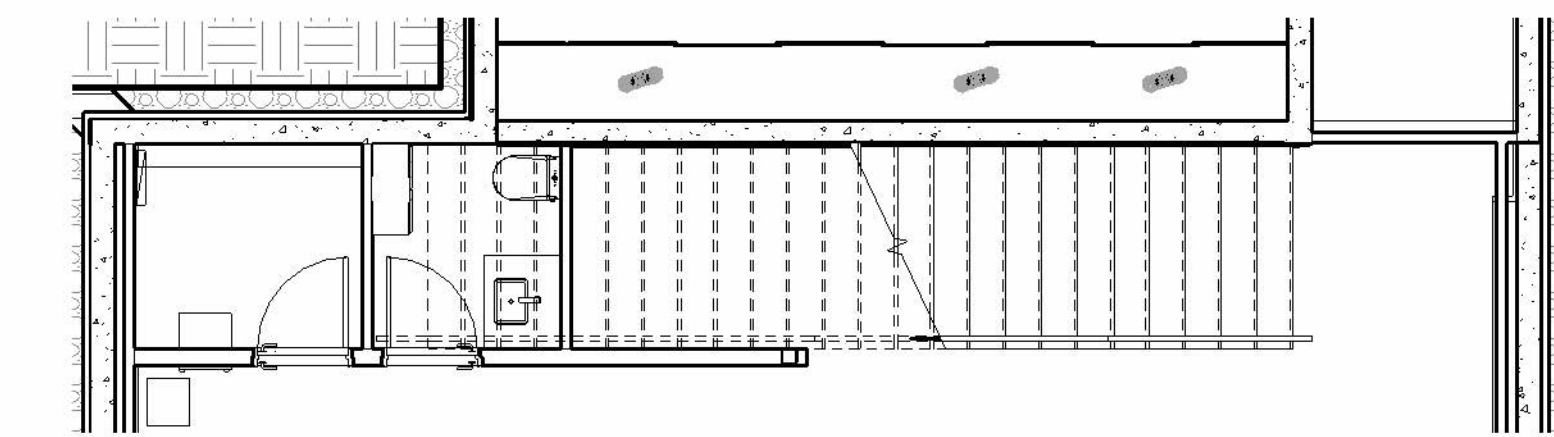


③ 4-Lower Plumbing
3/16" = 1'-0"

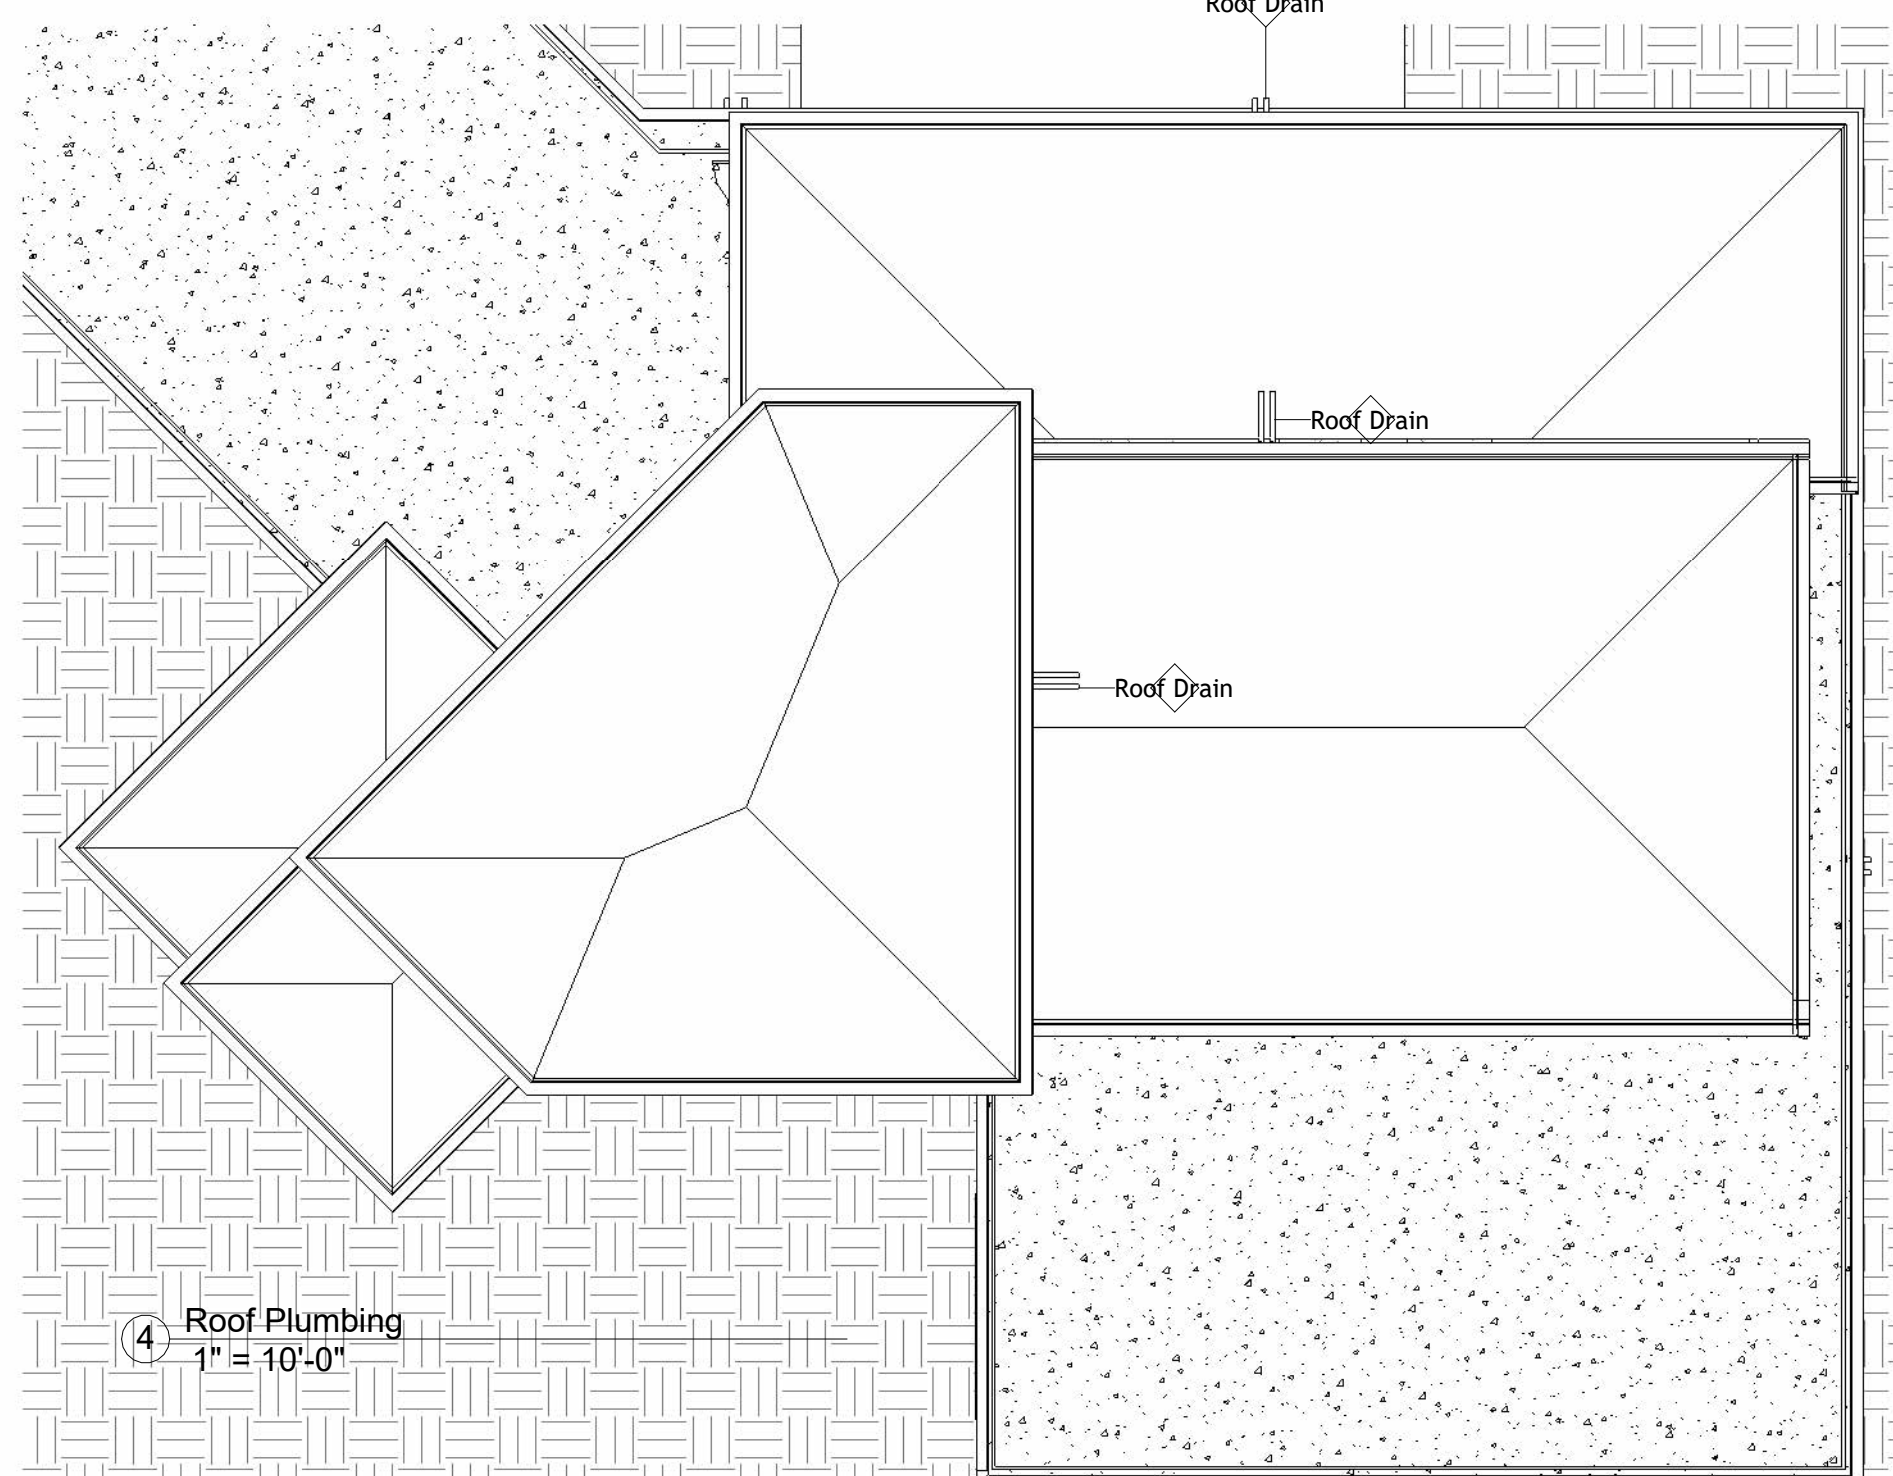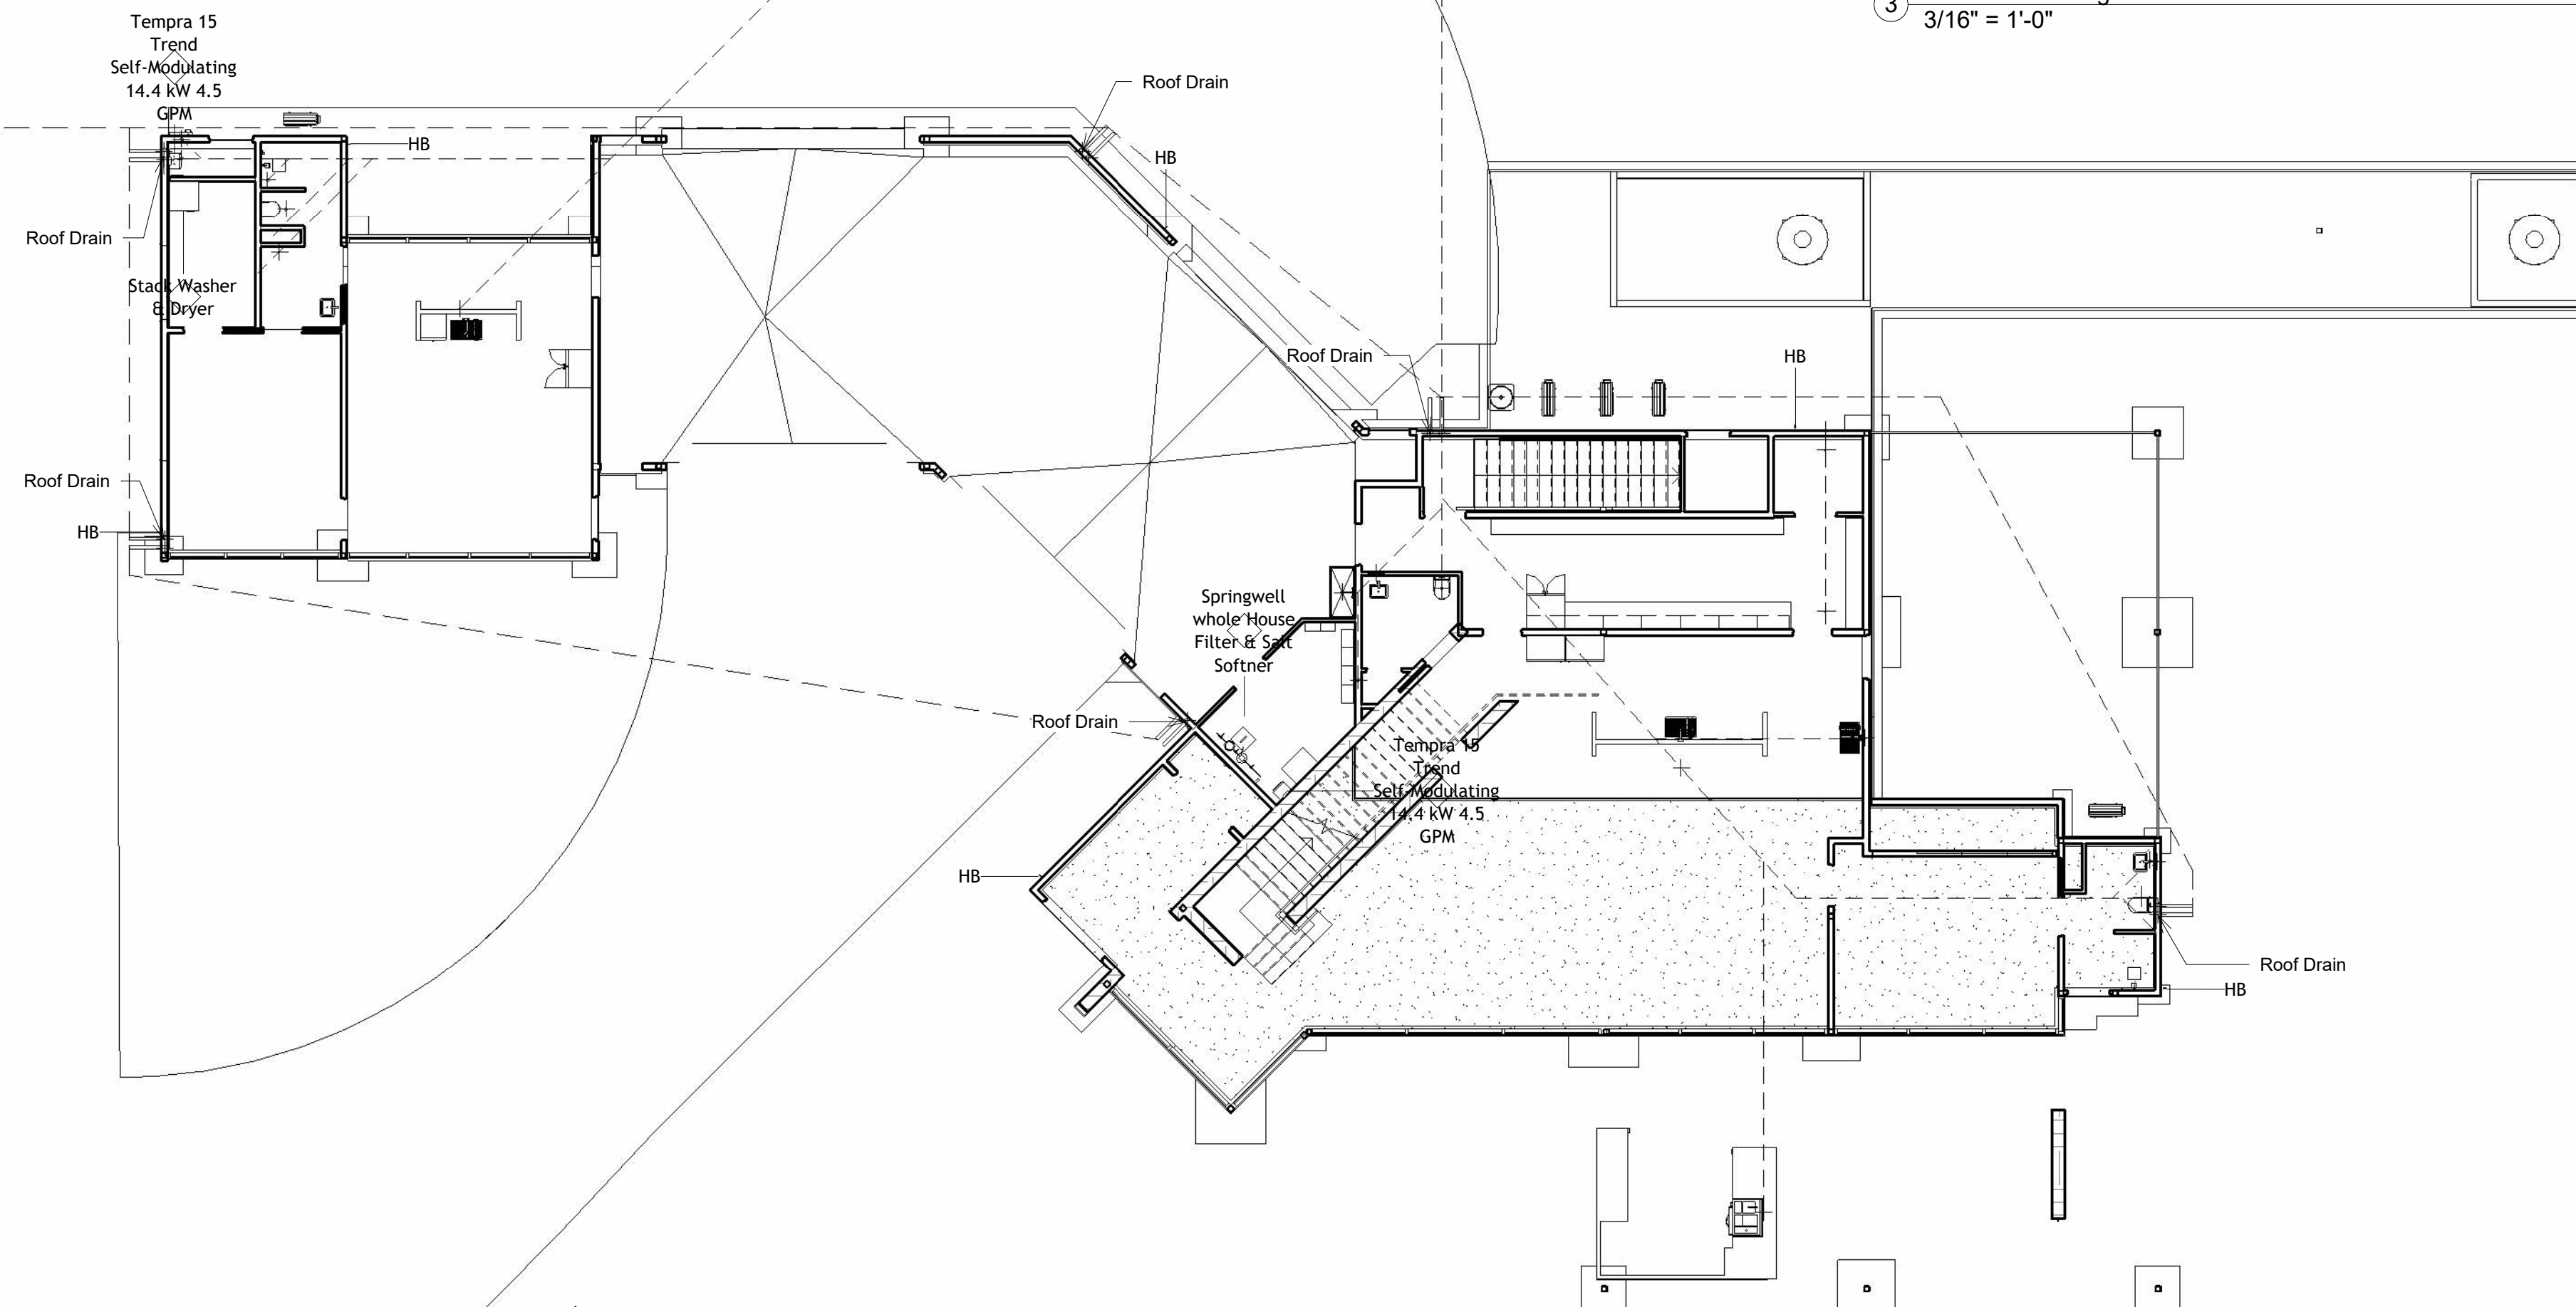

④ Roof Plumbing
1" = 10'-0"

Plumbing Fixture Schedule			
Manufacturer	Model	Count	Level
Homary	Simple Single Waterfall Handle Single-Hole Bathroom Brass Sink Faucet with Pop-Up Drain Assembly Kit Included in Black	1	Basement
KOHLER Co.	K-8189-7	1	Basement
Winner	Smart Toilet	1	Basement
Gessi	Vita	1	Main
GrandJoy	Shower Set	2	Main
Hansgrohe	72861TXX	2	Main
Homary	Simple Single Waterfall Handle Single-Hole Bathroom Brass Sink Faucet with Pop-Up Drain Assembly Kit Included in Black	3	Main
Hose Bib	Hose Bib	7	Main
KOHLER Co.	K-5409-NA	3	Main
KOHLER Co.	K-8189-7	3	Main
Winner	Smart Toilet	3	Main
Aquatica	Corella	1	12
GrandJoy	Shower Set	2	12
Homary	Simple Single Waterfall Handle Single-Hole Bathroom Brass Sink Faucet with Pop-Up Drain Assembly Kit Included in Black	2	12
Hose Bib	Hose Bib	3	12
KOHLER Co.	K-8189-0	2	12
Sink/Faucet	Laundry	1	12
Tub Filler		1	12
Winner	Smart Toilet	2	12

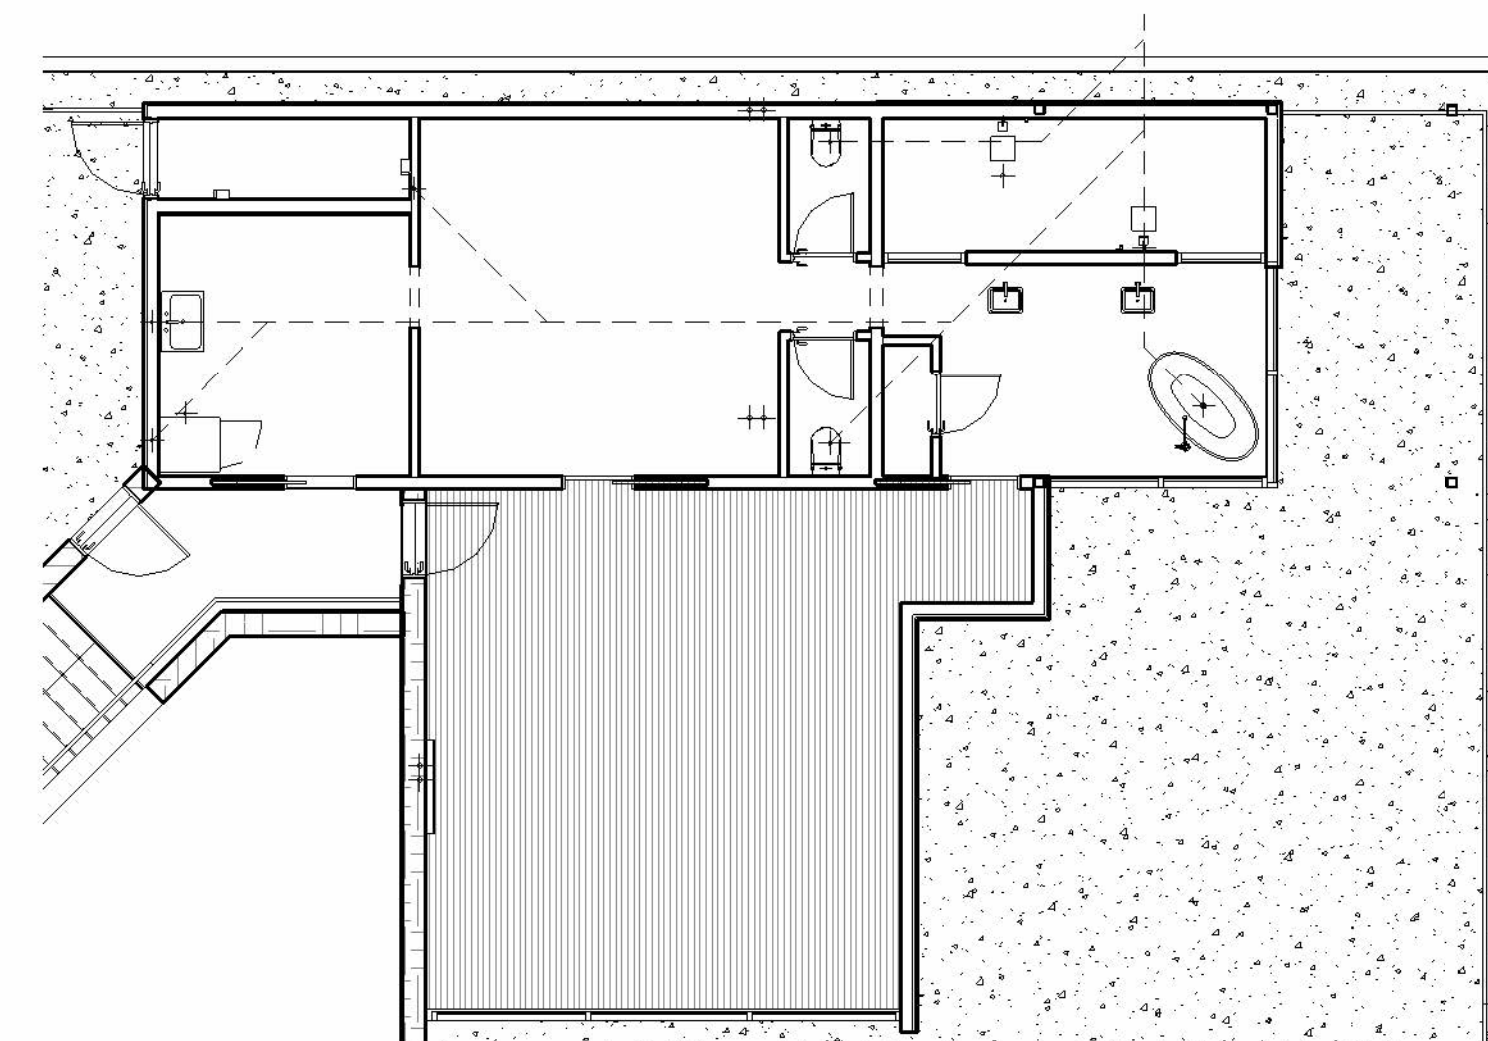

② 3-Upper Plumbing
1/8" = 1'-0"