


Consultant Craig Engel
Firm RAC Development
Address 1267 N.. 1390 W . St. George UT
Phone (435) 229-7360
Fax
e-mail racinc19@gmail.com

Consultant
Firm
Address
Phone
Fax
e-mail


Consultant
Firm
Address
Phone
Fax
e-mail

Consultant
Firm
Address
Phone
Fax
e-mail

Consultant
Firm
Address
Phone
Fax
e-mail

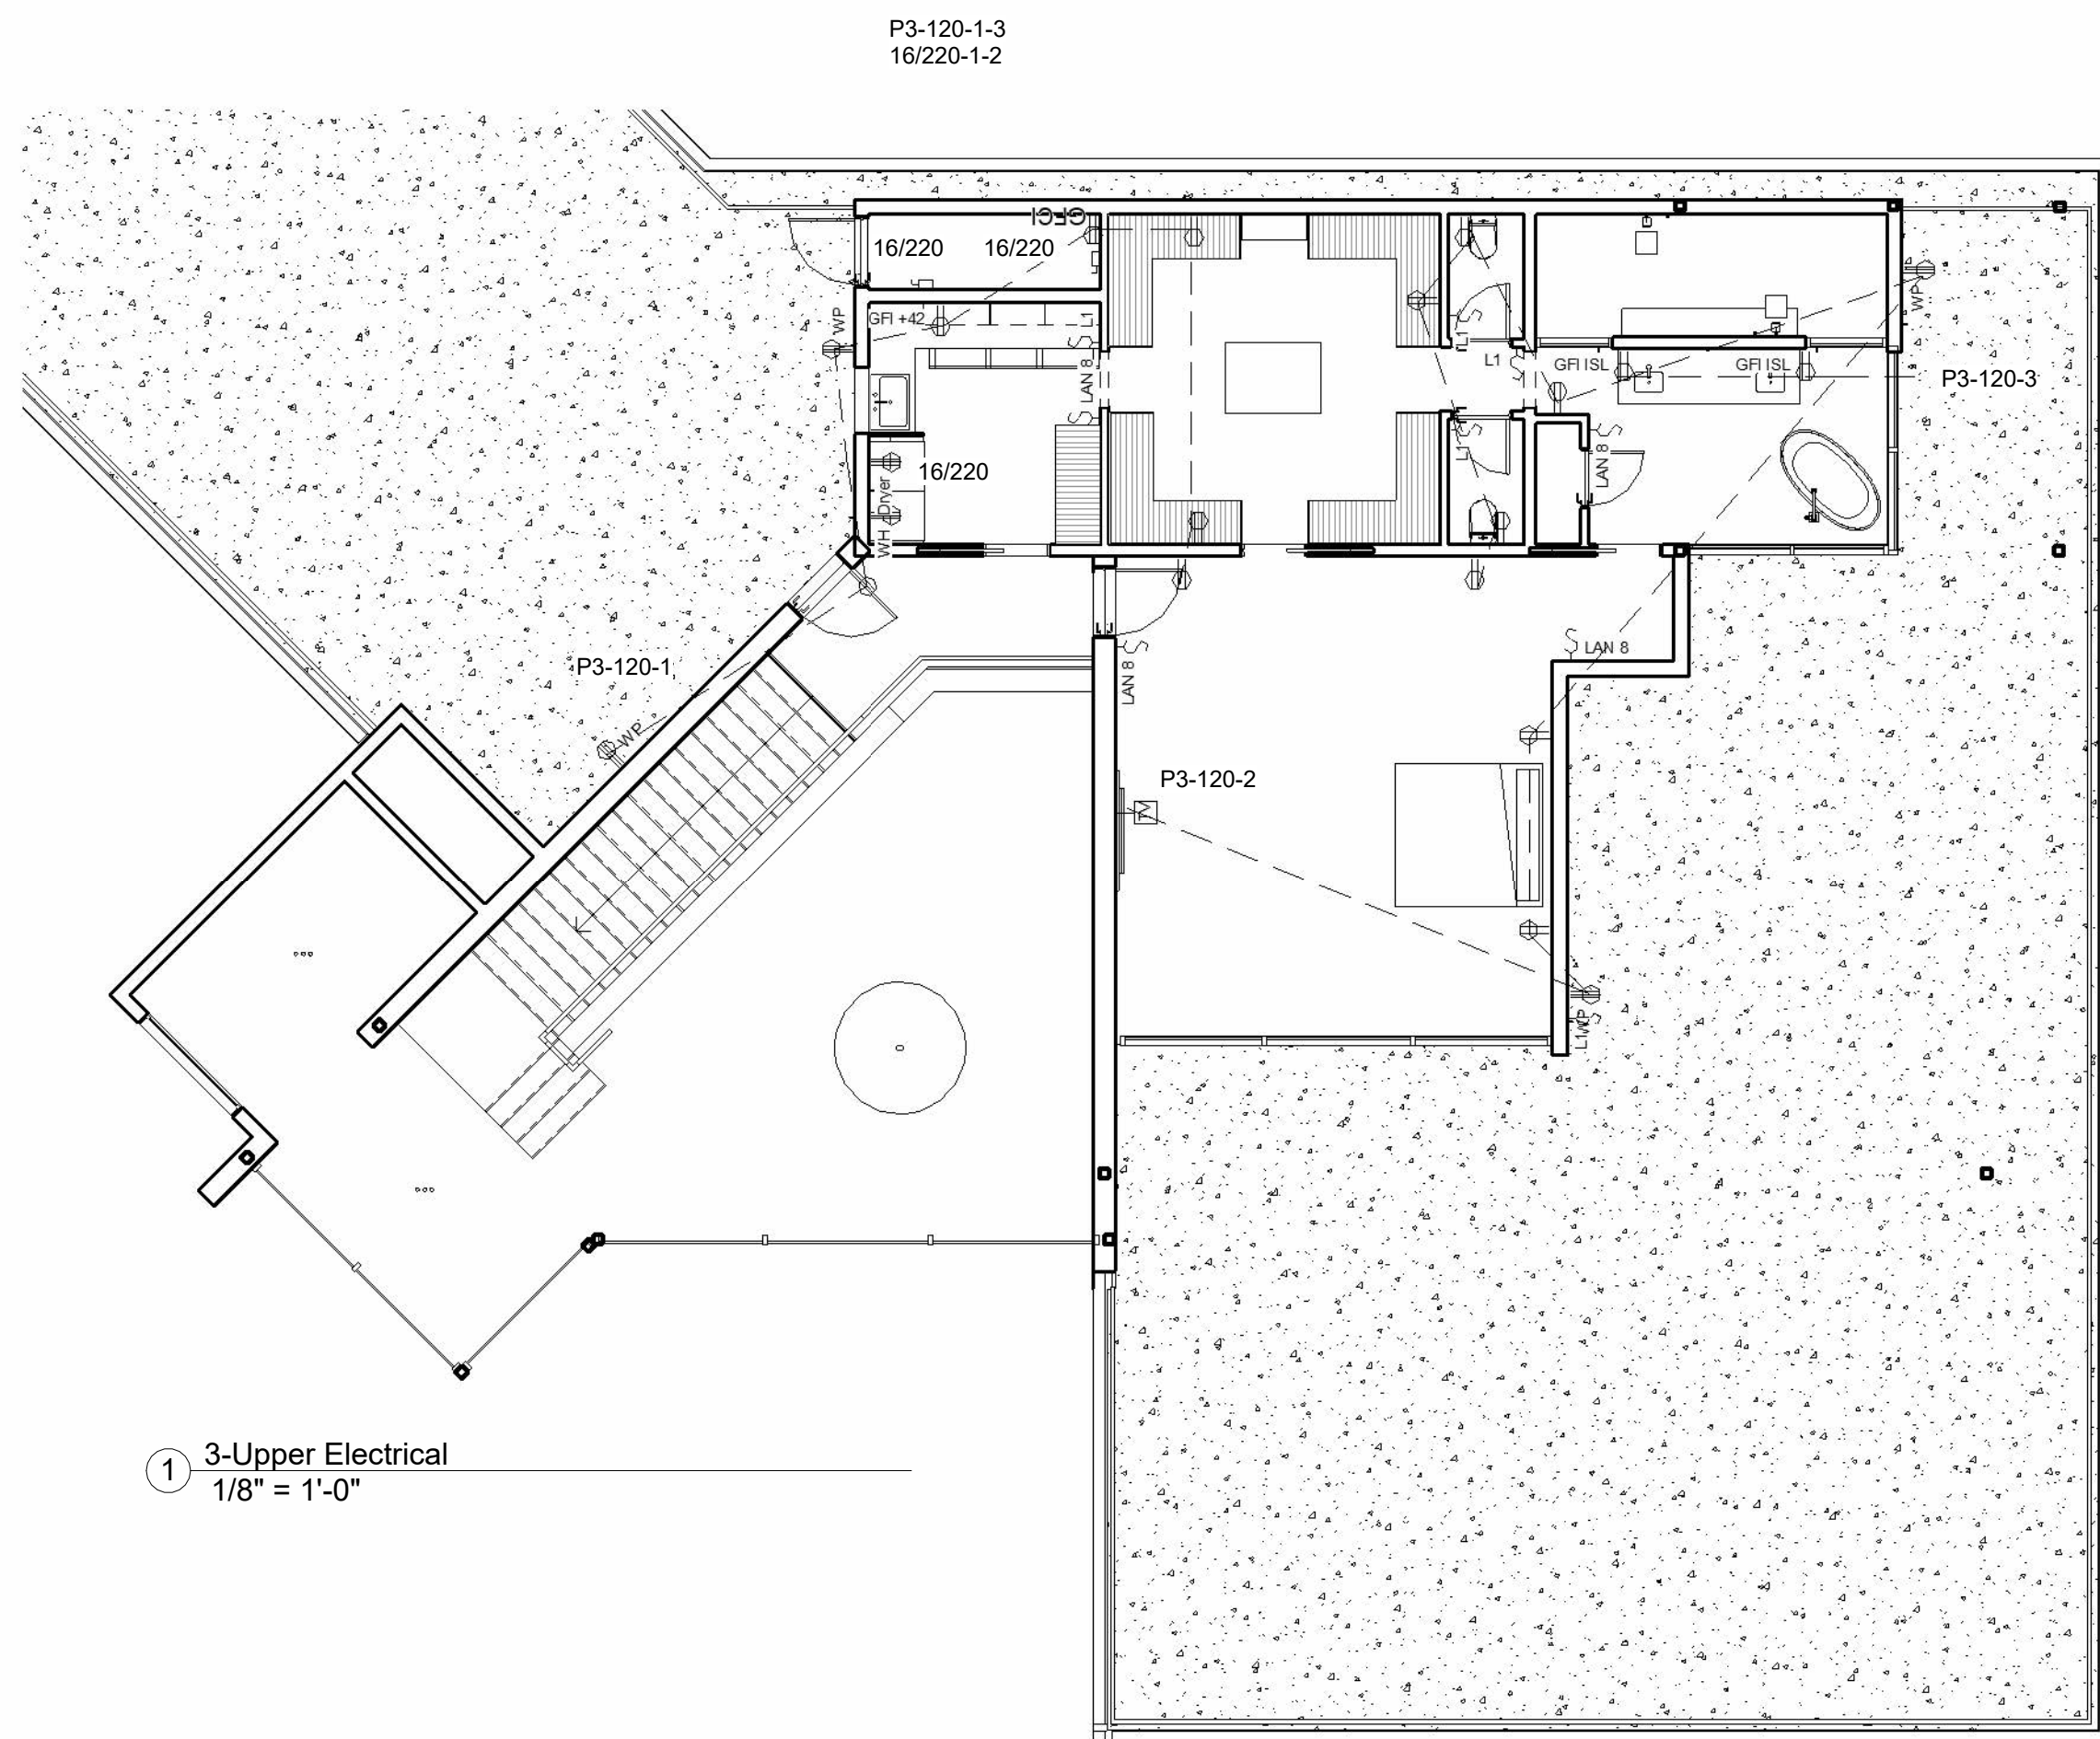

① 3-Upper Electrical
1/8" = 1'-0"

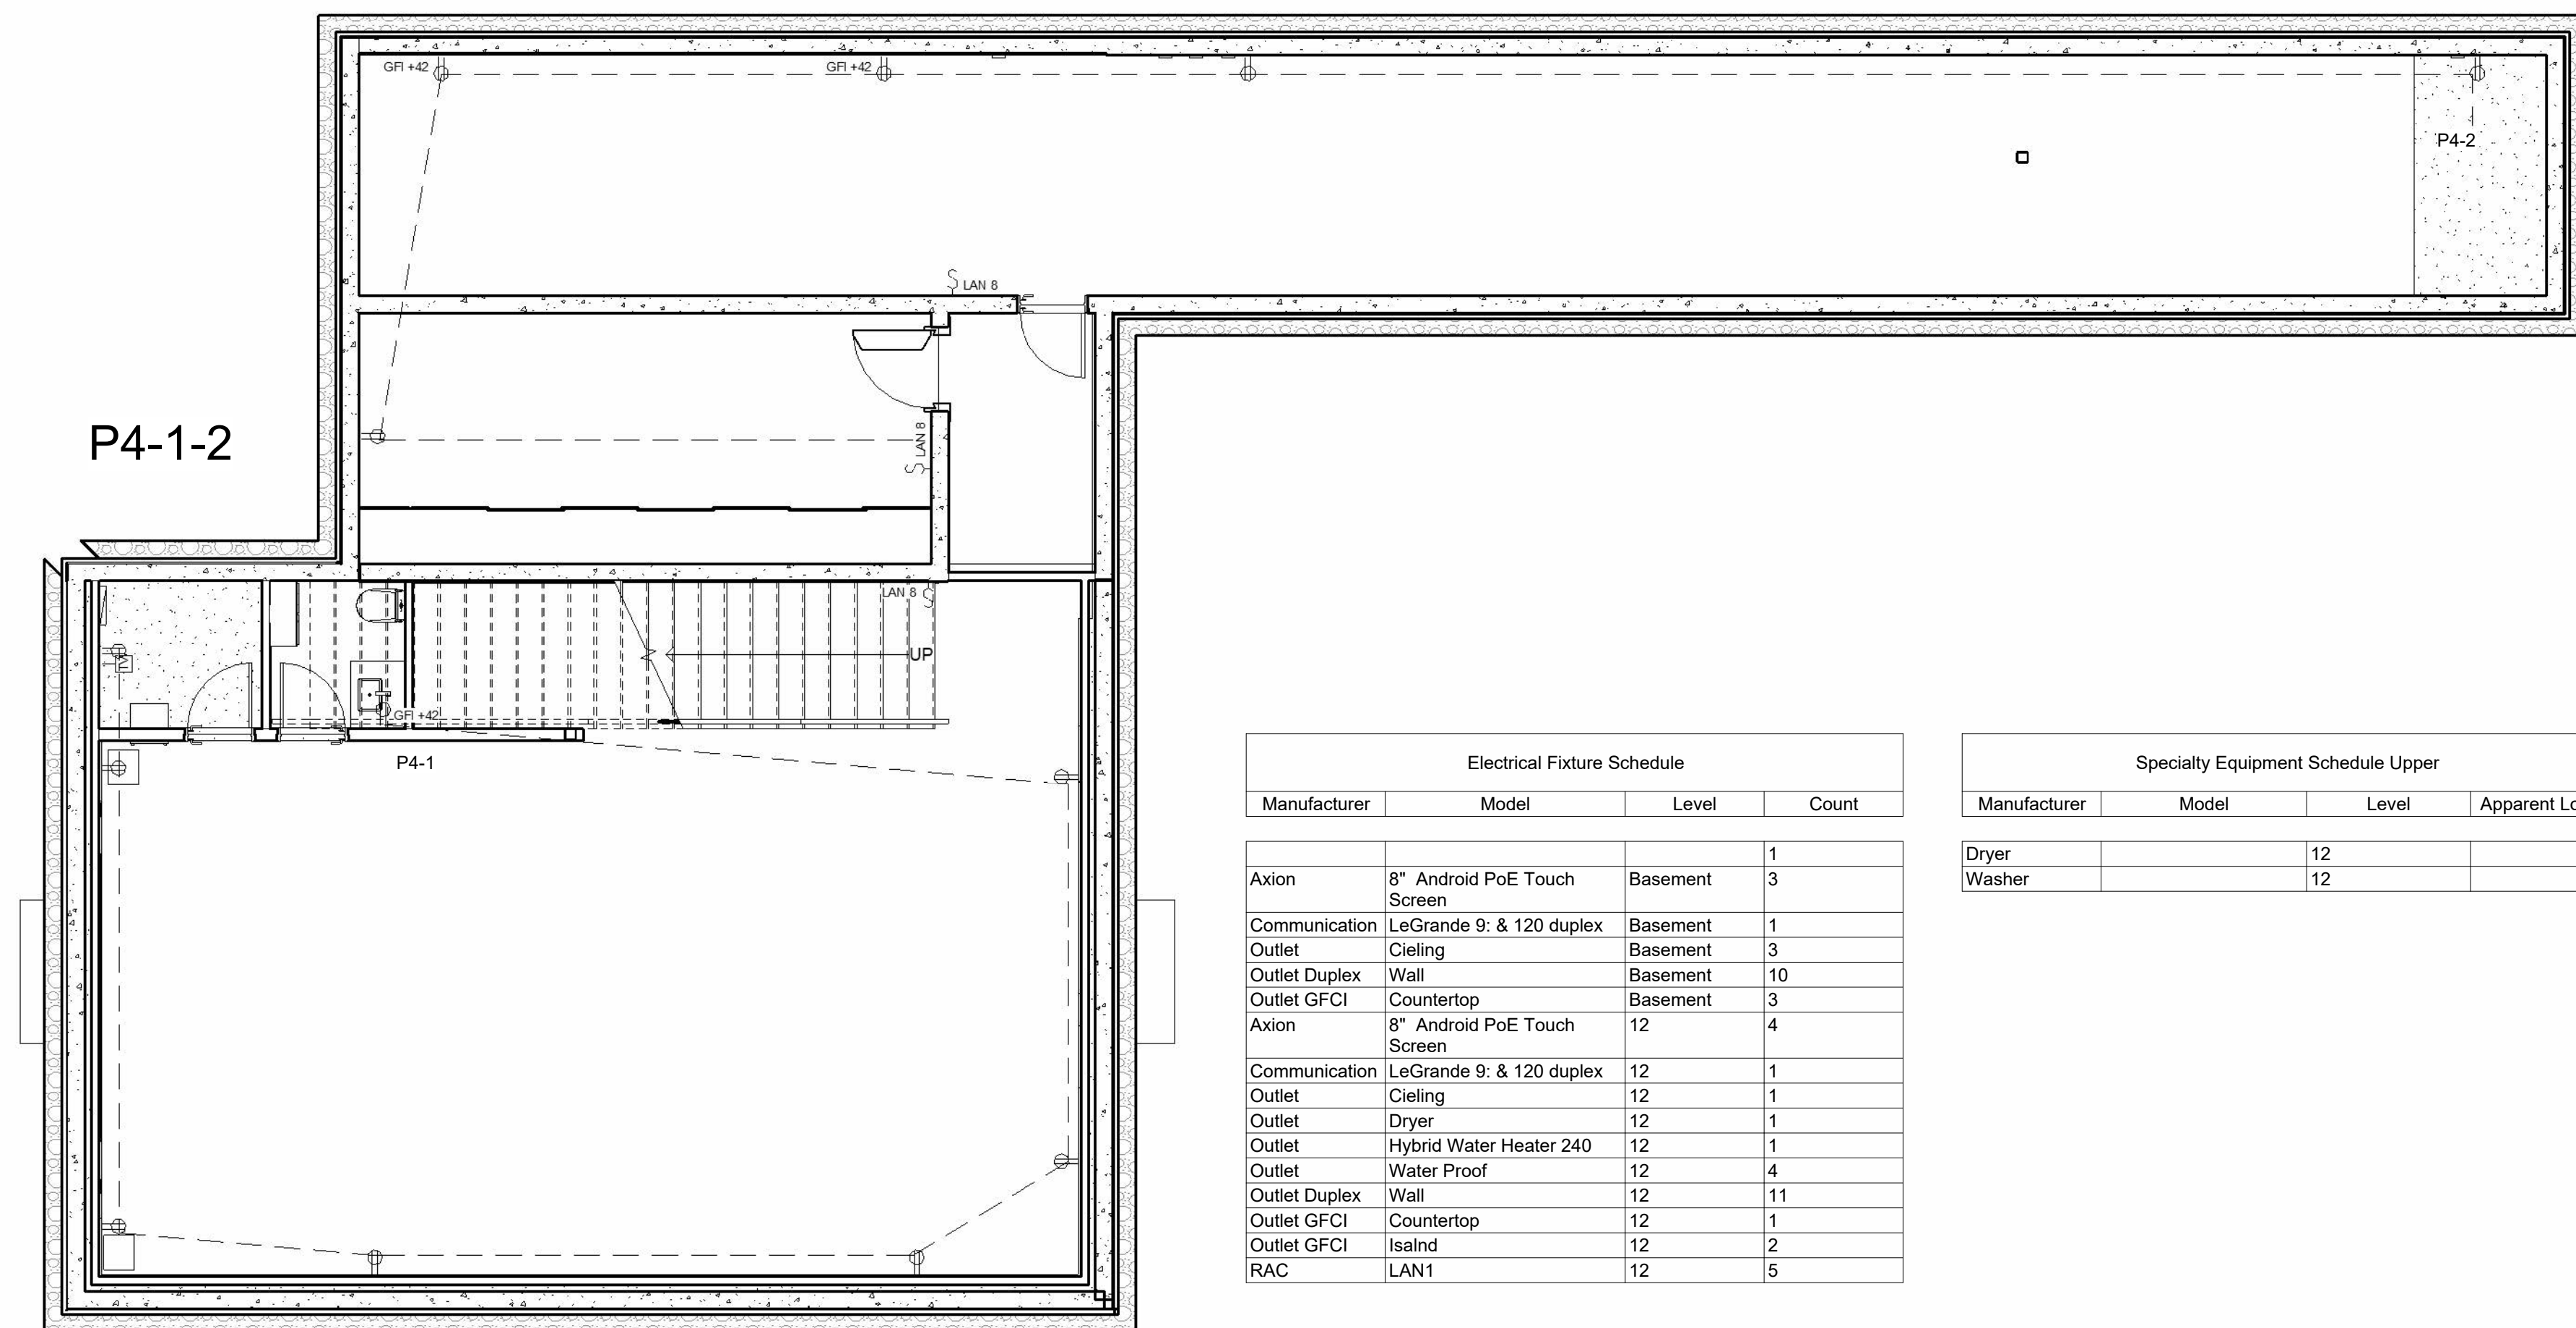

② 4-Lower Electrical
3/16" = 1'-0"

Electrical Fixture Schedule			
Manufacturer	Model	Level	Count
			1
Axion	8" Android PoE Touch Screen	Basement	3
Communication	LeGrande 9: & 120 duplex	Basement	1
Outlet	Ceiling	Basement	3
Outlet Duplex	Wall	Basement	10
Outlet GFCI	Countertop	Basement	3
Axion	8" Android PoE Touch Screen	12	4
Communication	LeGrande 9: & 120 duplex	12	1
Outlet	Ceiling	12	1
Outlet	Dryer	12	1
Outlet	Hybrid Water Heater 240	12	1
Outlet	Water Proof	12	4
Outlet Duplex	Wall	12	11
Outlet GFCI	Countertop	12	1
Outlet GFCI	Isalnd	12	2
RAC	LAN1	12	5

Specialty Equipment Schedule Upper			
Manufacturer	Model	Level	Apparent Load
Dryer		12	
Washer		12	

[illegible]

Mr. & Mrs. Rodriguez
Oak Valley Estates #5
Upper/Lower Electrical

Project number	Project Number
Date	Issue Date
Drawn by	Author
Checked by	Checker

E101

Scale	As indicated
-------	--------------