



Consultant Craig Engel
Firm RAC Development
Address 1267 N.. 1390 W . St. George UT
Phone (435) 229-7360
Fax
e-mail racinc19@gmail.com

Consultant
Firm
Address
Phone
Fax
e-mail

Consultant
Firm
Address
Phone
Fax
e-mail

Consultant
Firm
Address
Phone
Fax
e-mail

Consultant
Firm
Address
Phone
Fax
e-mail


[illegible]

Mr. & Mrs. Rodriguez
Oak Valley Estates #5
Upper/Lower Electrical Ceiling

Project number	Project Number
Date	Issue Date
Drawn by	Author
Checked by	Checker

E103

Scale	$3/16" = 1'-0"$
-------	-----------------

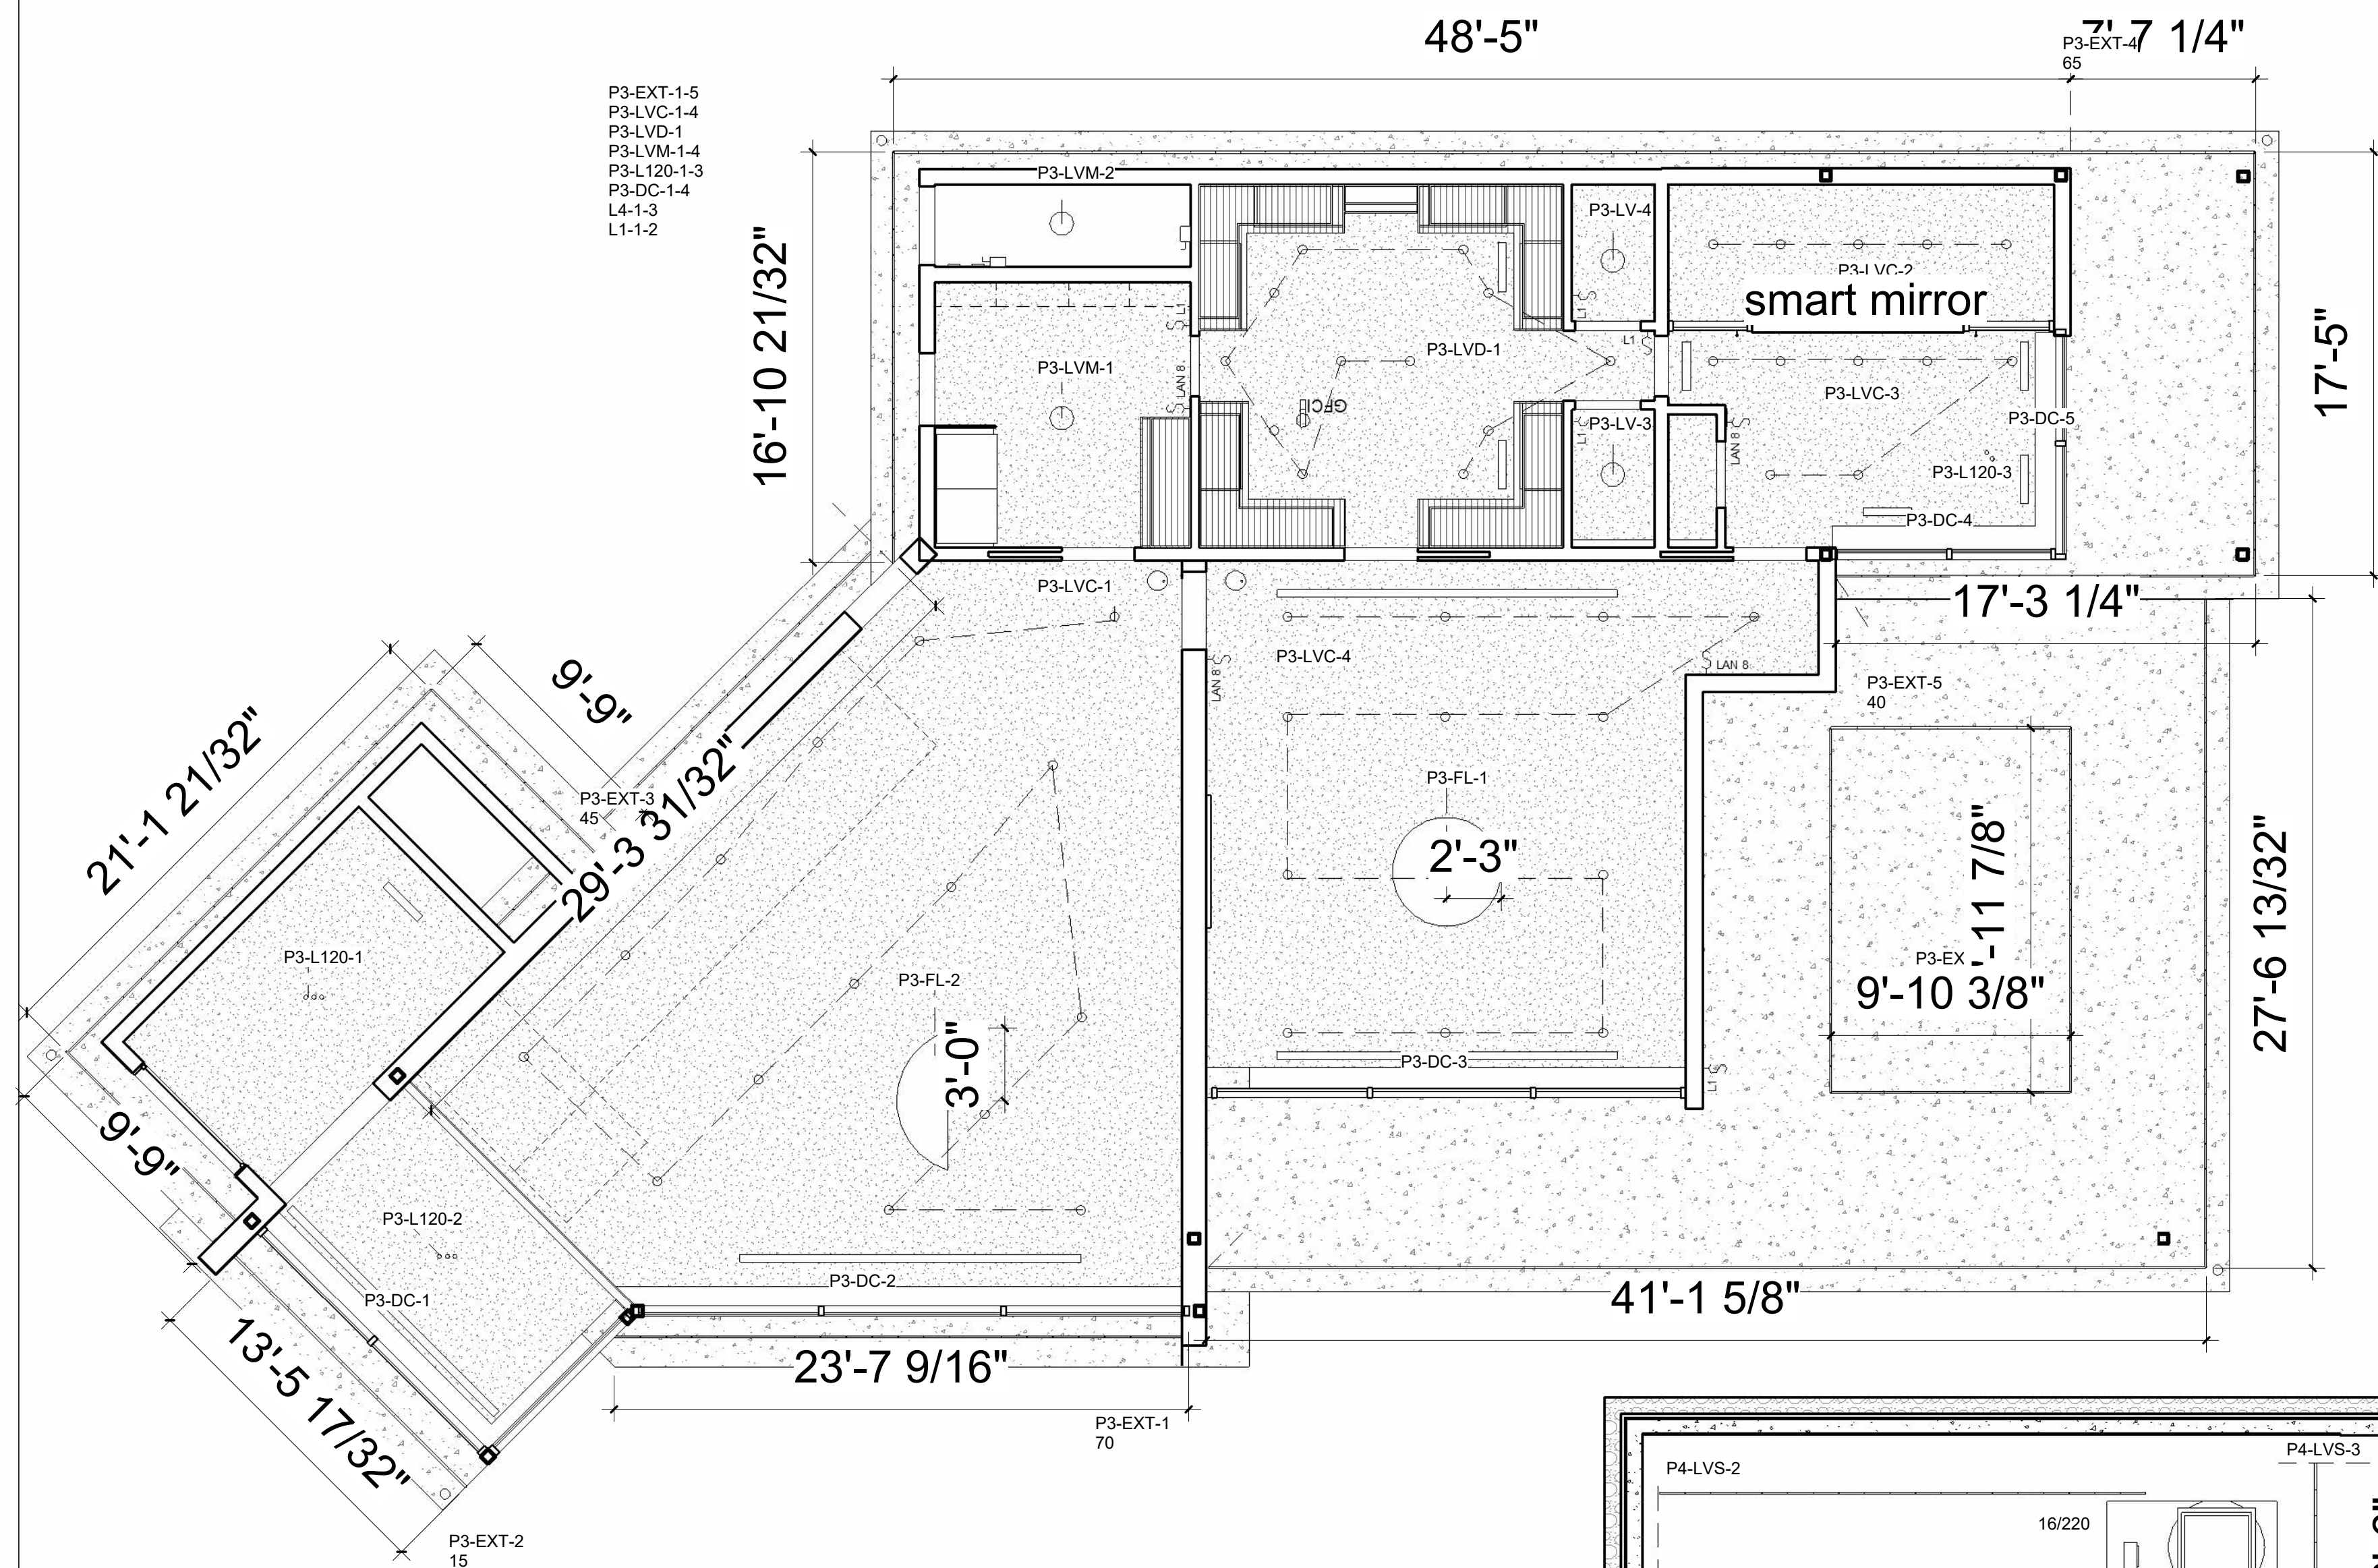

1 Upper Ceiling Electrical
3/16" = 1'-0"

Lighting Fixture Upper/Lower							
Manufacturer	Model	Mark	Wattage	Count	Circuit Number	Panel	Level
Focal Point	3.5" Wash	<varies>	7 W	103			
XAL	Motion Flush	XAL M	12 W	9			
Focal Point	3.5" Wash	FP3.5	7 W	2			Basement
XAL	Motion Flush	XAL M	12 W	1			Basement
FLY Achilles	Modern MinimalistLED Long Strip Indoor Pendant Lights		16 W	2			10
Lightology	A Tubes	LAT	12 W	1			10
Focal Point	3.5" Wash	FP7W	7 W	26			12
XAL	Laundry	<varies>	7 W	4			12
Lightology	A Tubes	<varies>	12 W	3			22

LED Strip Upper/Lower								
3333	Model	Mark	Wattage	Count	Panel	Level	Comments	Keynote

② Lower Ceiling Electrical
3/16" = 1'-0"

